

PLANTA BAIXA — SUBSOLO GOURMET E ÁREA DA PISCINA (FASE 2)

ESCALA 1:50 · cortada a 1,20 m do piso do subsolo gourmet (-3,60) · cotas e níveis em metros (±0,00 = piso acabado do térreo)

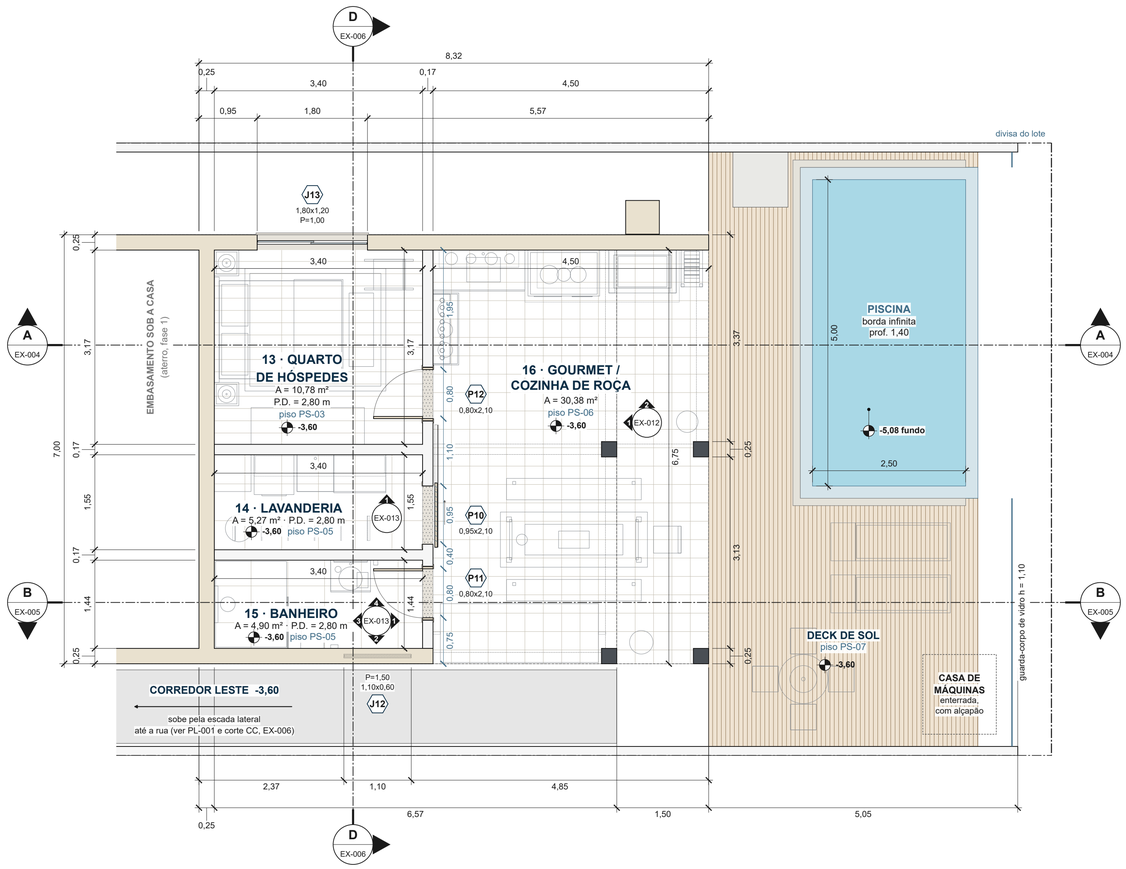

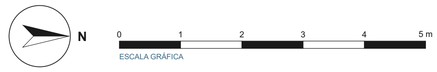

LEGENDA

- Alvenaria cortada (plano a 1,20 m)
- Pedra (embasamento, chaminé, arrimo)
- Concreto (pilar/contenção — referência, ver estrutural)
- Soleira de granito
- Batente, alizar e folha de madeira (portas)
- Esquadria de alumínio e vidro; peitoril com pingadeira
- Projeção acima do corte (laje, viga, aéreo)
- Beiral (projeção da laje de cobertura)
- Mobiliário e equipamentos (indicativo)
- Paginação do piso (juntas)
- P1 — Porta: L x H (vão livre)
- J1 — Janela: L x H e P = peitoril
- EX-0nn — Vista interna das áreas molhadas (1:25) — seta para a parede vista, com o nº da vista; no círculo, a folha de destino (EX-012 e EX-013)
- ±0,00 — Nível de piso acabado (±0,00 = 754,15 m SRTM)
- Cota de amarração de porta (canto → batente)

QUADRO DE ESQUADRIAS DO SUBSOLO GOURMET (Q02)

Cód.	L (m)	H (m)	Peit. (m)	Tipologia	Material	Ambientes	Qtd.	Detalhe
P10	0,95	2,10	0,00	correr veneziana	madeira azul colonial · trilho preto	Lavanderia / Gourmet / cozinha de roça	1	EX-014
P11	0,80	2,10	0,00	giro 1 folha	madeira pintada azul colonial (gourmet de roça)	Banheiro / Gourmet / cozinha de roça	1	EX-014
P12	0,80	2,10	0,00	giro 1 folha	madeira pintada azul colonial (gourmet de roça)	Quarto de hóspedes / Gourmet / cozinha de roça	1	EX-014
J12	1,10	0,60	1,50	maxim-ar	alumínio preto + vidro mini-boreal 4 mm	Banheiro	1	EX-015
J13	1,80	1,20	1,00	correr 2 folhas	alumínio preto + vidro incolor 6 mm	Quarto de hóspedes	1	EX-015

NOTAS E HIPÓTESES

1. FASE 2 (obra posterior à casa). Subsolo gourmet e área da piscina sobre ATERRO compactado. A contenção e o aterro sob a casa (até a laje do térreo) são da fase 1. Contenção, arrimos, drenagem e fundação dos pilares da gourmet dependem do levantamento planialtimétrico, da sondagem e do projeto estrutural.
2. Cotas em metros, de face acabada a face acabada; níveis relativos ao piso acabado do térreo (subsolo gourmet em -3,60; deck da área da piscina em -3,60). P.D. medido do piso acabado à face inferior do forro de madeira ou da laje (mesmo critério dos cortes).
3. Paredes externas do subsolo gourmet em pedra até a laje do térreo; gourmet aberta para o deck (pilares indicados como referência).
4. Piscina: dimensões e profundidade de projeto; casa de máquinas enterrada sob o deck, com alçapão.
5. Escada lateral externa com degraus e patamares conforme NBR 9050 (planta na implantação PL-001; corte CC na EX-006).
6. Guarda-corpo de vidro da área da piscina com 1,10 m acima do deck acabado (NBR 14718).
7. Somente arquitetura: estrutura, contenção e instalações por projetos complementares (terceiros).
8. Cortes AA, BB e DD: ver EX-004 a EX-006.
9. Vistas internas das áreas molhadas: ver EX-012 e EX-013 (1:25; gourmet / cozinha de roça na EX-012, lavanderia e banheiro na EX-013).
10. Esquadrias: portas L x H = vão livre de passagem; janelas L x H = vão acabado; P = peitoril (granito; na J1, a base da moldura grafite com caimento e pingadeira, padrão usual de 11/10/2026), do piso acabado interno ao topo do peitoril. Ver quadro Q02; folhas, ferragens e cores a confirmar com a cliente.
11. Detalhamento das esquadrias: ver EX-014 a EX-016 (portas P10 a P12 na EX-014 e janelas J12 e J13 na EX-015, em 1:25; quadro geral e detalhes típicos em 1:5 e 1:10 na EX-016). Folha de cada esquadria: coluna Detalhe do Q02.
12. Paginação de piso: ver EX-017 (térreo) e EX-018 (subsolo gourmet); planta de forro: ver EX-019.

QUADRO DE AMBIENTES DO SUBSOLO GOURMET (Q01)

Nº	Ambiente	Área (m²)	Perím. (m)	P.D. (m)	Piso	Nível
13	Quarto de hóspedes	10,78	13,14	2,80	PS-03 Porcel. amadeirado 20 x 120	-3,60
14	Lavanderia	5,27	9,90	2,80	PS-05 Porcel. cimentício 60 x 60 acetinado	-3,60
15	Banheiro	4,90	9,68	2,80	PS-05 Porcel. cimentício 60 x 60 acetinado	-3,60
16	Gourmet / cozinha de roça	30,38	22,50	3,37	PS-06 Lajota cerâmica rústica 30 x 30	-3,60
	ÁREA ÚTIL DOS AMBIENTES	51,32				

QUADRO DE ACABAMENTOS DO SUBSOLO GOURMET (Q03)

Ambiente	Piso	Paredes	Teto
Quarto de hóspedes	PS-03 Porcel. amadeirado 20 x 120	reboco + massa + pintura branca; barrado azul colonial h = 1,10 + roda-meio	laje com gesso liso + pintura branca
Lavanderia	PS-05 Porcel. cimentício 60 x 60 acetinado	reboco + massa + pintura branca; azulejo colonial (tanque e bancada)	laje com gesso liso + pintura branca
Banheiro	PS-05 Porcel. cimentício 60 x 60 acetinado	reboco + massa + pintura branca; azulejo colonial no box e barrado h = 1,10	laje com gesso liso + pintura branca
Gourmet / cozinha de roça	PS-06 Lajota cerâmica rústica 30 x 30	reboco + massa + pintura branca; pedra mineira aparente (face interna das paredes de pedra); tijolinho aparente; azulejo colonial atrás da pia	forro de madeira
Deck da área da piscina	PS-07 Deck de madeira (varanda e área da piscina)	—	céu aberto

AVISO: Projeto executivo de ARQUITETURA (somente arquitetura). Implantação, aterro e arrimos dependem do levantamento planialtimétrico; estrutura, contenção e instalações ficam com os projetos complementares (terceiros).

REV.	DATA	DESCRIÇÃO	POR
R04	**08/10/2026**	**Emissão do executivo (Cleber): cotas 2 casas, cobertura EX-003, caixa 1 x 3.000 L e porta PC1**	**KMZERO**
R04	07/10/2026	Revisão 4 ([redacted]lha clara, banheiros e pendentes da suíte	KMZERO
R03	07/10/2026	Revisão 3 (Cleber): entrada pela sala, cozinha nos fundos com a varanda	KMZERO
R02	06/10/2026	Revisão 2 (Cleber): varanda 1,50, subsolo gourmet aterrado, gourmet nos fundos, portas, interiores	KMZERO
R01	06/10/2026	Revisão 1 (Cleber): recuos 1,50, cozinha em U, piso +0,15, cobertura, subsolo gourmet	KMZERO
R00	29/09/2026	Emissão inicial — estudo preliminar	KMZERO

KMZERO | ENGENHARIA · ARQUITETURA

EMPREENDIMENTO	LOCAL	ETAPA
RESIDÊNCIA [redacted]	Rio Espera / MG	**PROJETO EXECUTIVO**

CONTEÚDO DA PRANCHA

PLANTA BAIXA DO SUBSOLO GOURMET E ÁREA DA PISCINA

DESENHO	RESPONSÁVEL TÉCNICO	REGISTRO PROFISSIONAL
KMZERO	Kleber Vieira Martins · Arquitetura	ART/RRT a emitir

REVISÃO	DATA	ESCALA	UNIDADE	CÓDIGO DA PRANCHA
R04	07/10/2026	1:50	metro (m)	**AP-ARQ-EX-002**

Direitos autorais reservados à KMZERO. Cliente: [redacted]