
FACHADA SUL (FRENTE)

ESCALA 1:50 · vista da rua; muro frontal e portões translúcidos (folha própria de muro e portões) · observador ao sul, olhando para o norte

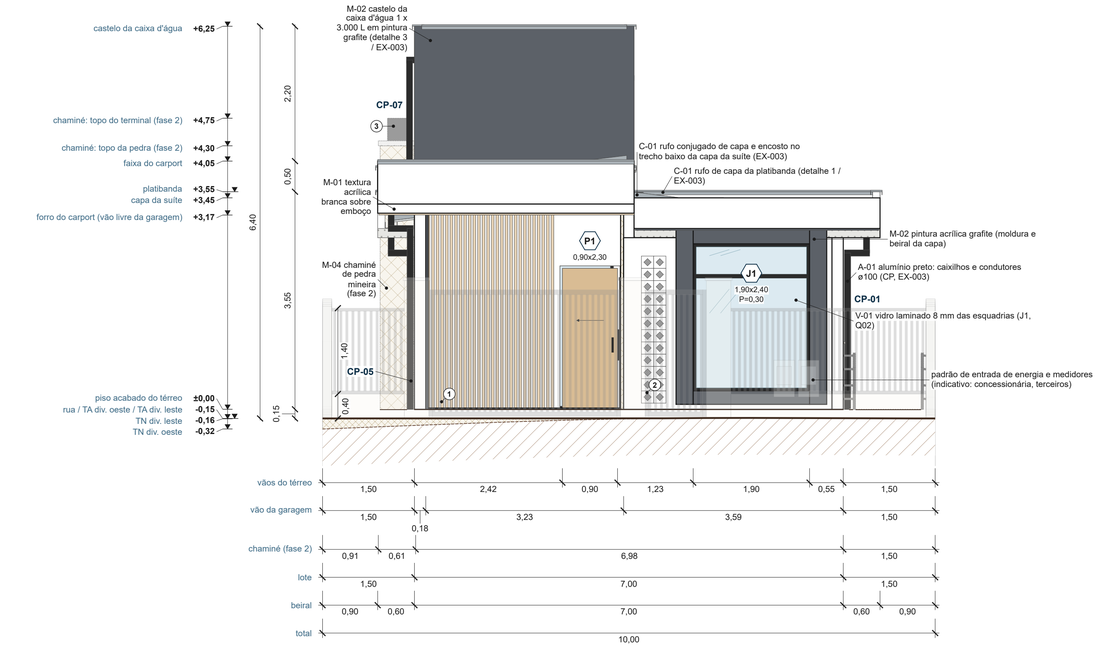


LEGENDA DAS FACHADAS

- Linhas: mais perto do observador = mais forte (0,35 / 0,25 / 0,18 / 0,13 mm)
- Fase 2: esmaecido e contorno tracejado
- Muros, gradil e portões translúcidos (folha própria)
- M-xx — Chamada: código do material (quadro de materiais) e descrição
- 1 — Chamada numerada: texto na lista CHAMADAS NUMERADAS da folha
- Jn — Esquadria: código, L x H (vão) e P = peitoril (quadro Q02)
- Correr: seta no sentido em que a folha abre
- Giro: tracejado com o vértice nas dobradiças
- Maxim-ar: vértice no topo (articulação)
- Basculante: eixo horizontal (traço-ponto)
- Fixa: só vidro e perfis
- Veneziana fixa (VC1)
- Porta de metal vazado (PC1)
- CP-0n — Condutor pluvial aparente (numeração da EX-003)
- Nível (m; ±0,00 = piso acabado do térreo)
- Terreno acabado TA (cheio) e natural TN (tracejado, SRTM)
- Aterro no plano da divisa
- Arrimo de divisa em pedra (indicativo, terceiros)

QUADRO DE MATERIAIS DE FACHADA

Cód.	Amostra	Material / acabamento	Ref. de cor (JSON)
M-01		Textura acrílica branca sobre emboço	Reboco branco (#EDEDE8)
M-02		Pintura acrílica grafite (moldura, frisos, forro da capa)	Fachada grafite (#26292B)
M-04		Pedra natural mineira (embasamento, contenção, pilares do portão, chaminé)	Pedra mineira (#AD9973)
M-05		Painel ripado de madeira (garagem e forro do carport/varanda)	Madeira ripada (#804F2B)
M-06		Cobogó — elemento vazado 20 x 20 x 9 cm	Reboco branco (#EDEDE8)
M-07		Concreto aparente / laje (pilares, arrimos e piscina)	Concreto (#9E9E99)
V-01		Vidro incolor/laminado (esquadrias e guarda-corpo)	Vidro (#9ECCDB)
A-01		Alumínio preto (caixilhos, gradil, portões, corrimão)	Alumínio preto (#0A0A0D)
C-01		Rufo de capa com pingadeira, calha e rufo de encosto em chapa galvanizada pré-pintada (EX-003)	Rufo (#8C9194)
C-02		Granito cinza andorinha polido, 3 cm, com pingadeira (peitoris das janelas e soleira da PC1)	Granito peitoril (#9E9E99)
C-03		Tijolinho aparente (parede de fundo da gourmet, subsolo gourmet, fase 2)	Tijolinho (#9E5438)
C-05		Capa de concreto e terminal metálico (ferro fundido) no topo da chaminé (fase 2)	Ferro fundido (#141414)
C-06		Concreto desempenado, juntas 2,00 x 2,00 (escada lateral externa e corredor leste, fase 2)	Concreto desativado (#BDBAB5)

PLANTA-CHAVE · ESCALA 1:500

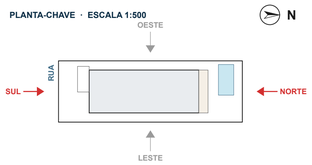


fachadas desta folha em vermelho

CHAMADAS NUMERADAS (no desenho)

1. M-05 painel ripado de madeira (fachada sul)
2. M-06 cobogó 20 x 20 x 9 cm (fachada sul)
3. C-05 capa de concreto e terminal metálico da chaminé (fase 2) (fachada sul)
4. M-04 arrimo de pedra (indicativo: projeto de contenção, terceiros) (fachada norte)
5. V-01 vidro incolor das esquadrias (Q02); laminado 8 mm em J8 (fachada norte)
6. C-06 escada lateral externa e corredor leste em concreto desempenado (fase 2) (fachada norte)
7. C-02 peitoril de granito com pingadeira (fachada norte)
8. C-03 tijolinho aparente ao fundo da gourmet (fachada norte)

FACHADA NORTE (FUNDOS)

ESCALA 1:50 · vista da cidade; subsolo gourmet, área da piscina e escada lateral (fase 2) · observador ao norte, olhando para o sul

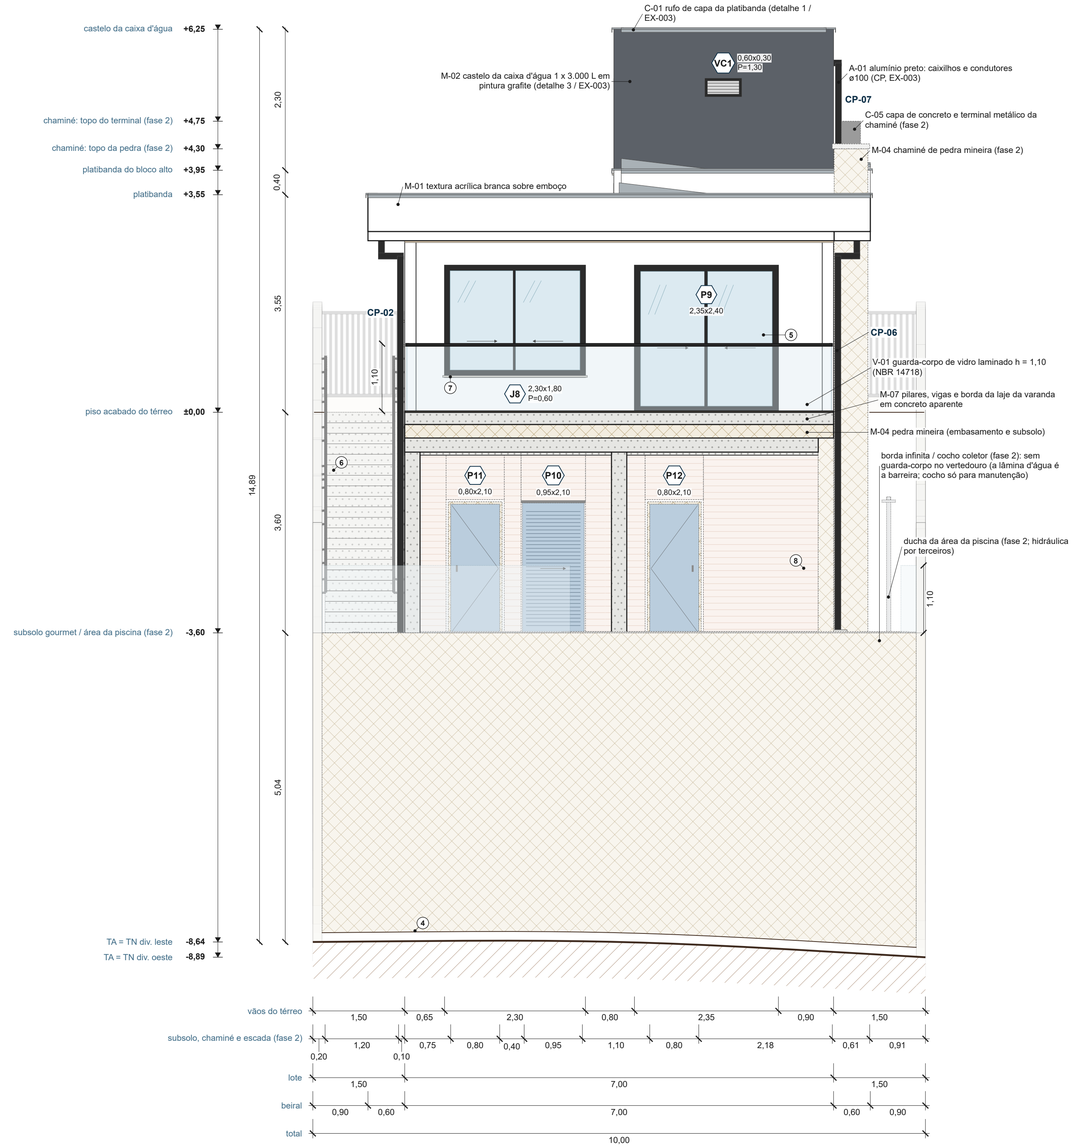

NOTAS GERAIS

1. Somente arquitetura. Estrutura, fundações, contenção e arrimos, impermeabilização e instalações (pluvial, hidráulica, elétrica e padrão de entrada) aparecem como INDICATIVOS: dimensionamento e detalhes nos projetos complementares (terceiros).
2. Cotas em metros com 2 casas; as cadeias fecham o total. Níveis em metros em relação ao piso acabado do térreo: ±0,00 = cota 754,15 (SRTM 30 m; confirmar no levantamento planialtimétrico). Terreno natural (TN, tracejado) do SRTM e terreno acabado (TA, cheio) do projeto, no plano da divisa mais próxima do observador.
3. Materiais conforme o QUADRO DE MATERIAIS DE FACHADA (códigos nas chamadas); a cor de referência é a do modelo (JSON). Cores, texturas e acabamentos finais a confirmar com a cliente (pendência: escolha dos acabamentos).
4. Esquadrias: portas L x H = vão livre de passagem, janelas L x H = vão acabado e P = peitoril, conforme os quadros Q02 das plantas EX-001 e EX-002 (detalhamento nas EX-014 a EX-016); porta PC1 e veneziana VC1 do castelo da caixa d'água conforme a EX-003 (detalhes 3 e 4). Sentido de abertura indicado pelo símbolo (legenda); caixilhos, gradil e portões em alumínio preto (A-01), peitoris de granito com pingadeira (C-02); folhas, ferragens e cores a confirmar com a cliente; folhas das portas (Q02): P1 em madeira; P10, P11 e P12 em azul colonial (fase 2); P9 de correr em alumínio preto (A-01) e vidro (V-01).
5. Ver plantas EX-001 (térreo) e EX-002 (subsolo gourmet e área da piscina), cobertura EX-003 (platibandas, rufos, calhas, condutores CP-01 a CP-07 e castelo) e cortes EX-004 a EX-006.
6. Muros de divisa, arrimos laterais, muro frontal, gradil e portões translúcidos (linha leve) onde escondem a casa: terão folha própria (muros e portões). Arrimos e contenção: indicativos, projeto de contenção (terceiros).
7. Subsolo gourmet, área da piscina, escada lateral e chaminé: FASE 2 (esmaecidos, contorno tracejado). Vão sob a casa, entre a frente e a contenção: aterro compactado até a laje do térreo (fase 1; decisão de 09/10/2026). Chaminé: pedra mineira (M-04) até +4,30, capa de concreto e terminal metálico (C-05) até +4,75.
8. Guarda-corpos de vidro laminado com 1,10 m acima do piso acabado (NBR 14718). Condutores pluviais ø100 aparentes em alumínio preto, numeração da EX-003: dimensionamento no projeto pluvial (terceiros).
9. Padrões usuais adotados em 11/10/2026 (reversíveis): vidro laminado 8 mm de segurança em J1 e J8; J1 com o peitoril na base da moldura grafite (M-02), com caimento e pingadeira, sem granito; borda infinita da piscina (cocho, topo -3,60, fase 2) sem guarda-corpo no vertedouro: a lâmina d'água que verte é a barreira e o cocho é só para manutenção; o guarda-corpo do terraço fica nos trechos laterais (ver EX-004); muros de divisa com 1,80 acima do terreno mais alto dos dois lados, também a leste (escada lateral e corredor leste).

0 1 2 3 4 5 m
ESCALA GRÁFICA

REV.	DATA	DESCRIÇÃO	POR
R04	**08/10/2026**	**Emissão do executivo (Cleber): cotas 2 casas, cobertura EX-003, caixa 1 x 3.000 L e porta PC1**	**KMZERO**
R04	07/10/2026	Revisão 4 [redacted] lha clara, banheiros e pendentes da suíte	KMZERO
R03	07/10/2026	Revisão 3 (Cleber): entrada pela sala, cozinha nos fundos com a varanda	KMZERO
R02	06/10/2026	Revisão 2 (Cleber): varanda 1,50, subsolo gourmet aterrado, gourmet nos fundos, portas, interiores	KMZERO
R01	06/10/2026	Revisão 1 (Cleber): recuos 1,50, cozinha em U, piso +0,15, cobertura, subsolo gourmet	KMZERO
R00	29/09/2026	Emissão inicial — estudo preliminar	KMZERO

KMZERO | ENGENHARIA · ARQUITETURA

EMPREENDIMENTO	LOCAL	ETAPA
RESIDÊNCIA [redacted]	Rio Espera / MG	PROJETO EXECUTIVO

CONTEÚDO DA PRANCHA

FACHADAS SUL (FRENTE) E NORTE (FUNDOS)

DESENHO	RESPONSÁVEL TÉCNICO	REGISTRO PROFISSIONAL
KMZERO	Kleber Vieira Martins · Arquitetura	ART/RRT a emitir

REVISÃO	DATA	ESCALA	UNIDADE	CÓDIGO DA PRANCHA
R04	07/10/2026	1:50	metro (m)	AP-ARQ-EX-007

Direitos autorais reservados à KMZERO. Cliente: [redacted]

AVISO: Projeto executivo de ARQUITETURA (somente arquitetura). Implantação, aterro e arrimos dependem do levantamento planialtimétrico; estrutura, contenção e instalações ficam com os projetos complementares (terceiros).