
LAVANDERIA E BANHEIRO — PLANTA AMPLIADA E VISTAS


N

ESCALA 1:25 · Lavanderia: A = 5,27 m² · P.D. 2,80 · piso PS-05 · N.A. -3,60 · Banheiro: A = 4,90 m² · P.D. 2,80 · piso PS-05 · N.A. -3,60 · planta cortada a 1,20 m do piso acabado · paginação do piso: Lavanderia: equilibrada (oeste-leste: peça no eixo; sul-norte: junta no eixo), peças de 600 x 600 mm; Banheiro: equilibrada (oeste-leste: peça no eixo; sul-norte: junta no vidro), peças de 600 x 600 mm

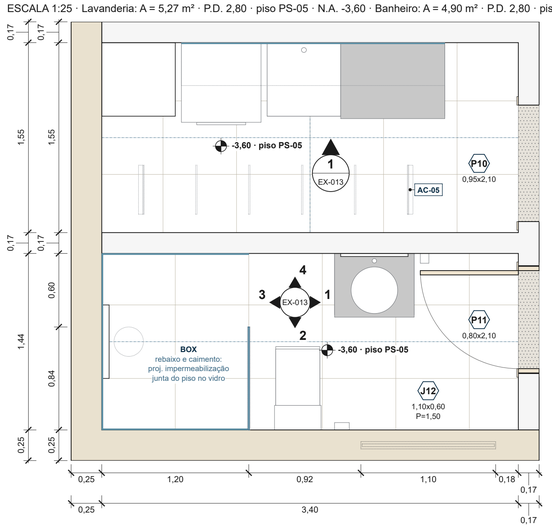


VISTA 1 — LAVANDERIA — parede oeste

ESCALA 1:25 · plano da vista a 0,99 m da parede

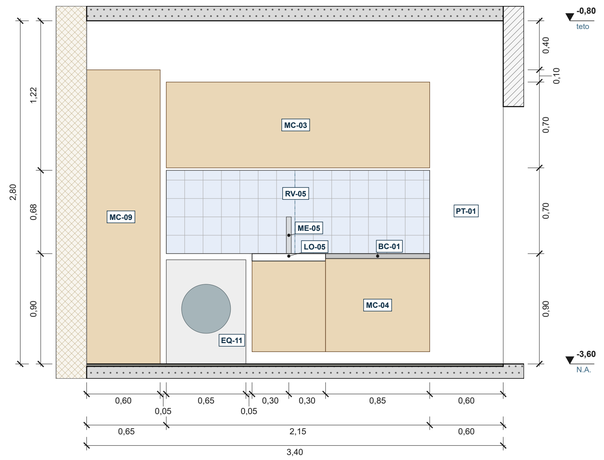


VISTA 1 — BANHEIRO — parede norte

ESCALA 1:25 · plano da vista a 2,17 m da parede

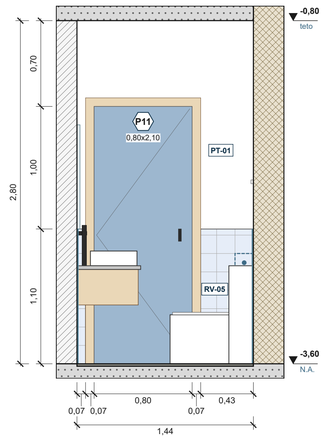


VISTA 2 — BANHEIRO — parede leste

ESCALA 1:25 · plano da vista a 0,91 m da parede

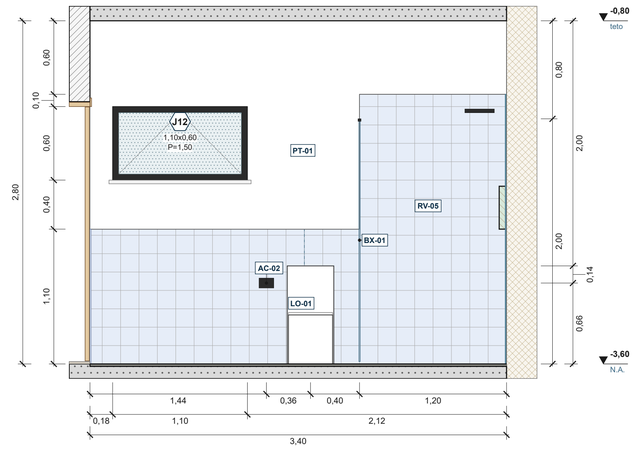


VISTA 3 — BANHEIRO — parede sul

ESCALA 1:25 · plano da vista a 3,38 m da parede

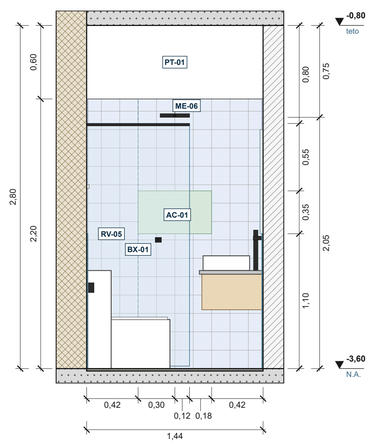

VISTA 4 — BANHEIRO — parede oeste

ESCALA 1:25 · plano da vista a 0,75 m da parede

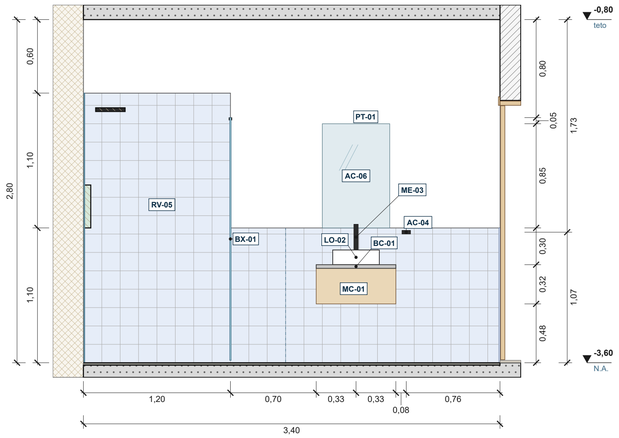

LEGENDA

- Alvenaria cortada
- Laje, viga, pilar cortados (indicativos)
- Pedra / contenção cortada (indicativa)
- Pedra / contenção (indicativa, terceiros)
- Piso acabado (N.A.)
- Revestimento de parede cortado
- Paginação (módulo de referência)
- Vidro do box e das esquadrias
- Louça, bancada, marcenaria, equipamento
- Marcenaria / bancada cortada pelo plano da vista
- Projeção acima do plano de corte da planta
- RV-nn — Código dos quadros desta folha
- J1 — Esquadria: Q02, L x H e P = peitoril
- 1 / EX-013 — Vista: número e folha (seta = visada)
- Eixo / início da paginação
- Início da paginação: 1ª peça inteira
- Nível acabado N.A. (±0,00 = térreo)

QUADRO DE REVESTIMENTOS, PINTURAS E TAMPOS (conferir as peças compradas antes de paginar)

Cód.	Material (texto do Q03 e dos cortes)	Peça (módulo de ref.)	Acabamento	Junta / rejunte	Paginação	Altura do N.A. (m)	Onde
BC-01	bancada em granito	lavanderia: esp. 0,04, prof. 0,62; banheiro: esp. 0,03, prof. 0,52	a definir com a cliente	—	sem saia / frontão (a definir)	Lavanderia: h = 0,90; Banheiro: h = 0,80	Banheiro, Lavanderia
PT-01	reboco + massa + pintura branca	—	a definir com a cliente	—	—	—	Banheiro, Lavanderia
RV-05	azulejo colonial no box e barrado h = 1,10; azulejo colonial (tanque e bancada)	150 x 150 mm (ref. render)	a definir com a cliente	3 mm (azulejo)	prumo — lavanderia V1; banheiro V2, V4: juntas do PS-05; banheiro V1: canto leste; banheiro V3: nicho	Banheiro: h = 2,20; 1,10; Lavanderia: h = 0,90 a 1,58	Banheiro, Lavanderia

QUADRO DE LOUÇAS, METAIS, ACESSÓRIOS, MARCENARIA E EQUIPAMENTOS (layout; modelo e fabricante a definir com a cliente)

Cód.	Peça (descrição genérica)	Medidas do modelo L x P x H (m)	Acabamento (modelo)	Onde
LO-01	bacia sanitária com caixa acoplada	0,38 x 0,68 x 0,80	louça branca	Banheiro
LO-02	cuba de apoio redonda	0,38 x 0,38 x 0,12	louça branca	Banheiro
LO-05	tanque de louça sobre gabinete	0,60 x 0,60 (L x P), borda de 0,84 a 0,90; profundidade da cuba a definir (o modelo tem só a borda)	louça branca	Lavanderia
ME-03	torneira de mesa (lavatório, bica alta)	0,04 x 0,04 x 0,33	preto	Banheiro
ME-05	torneira de mesa (tanque)	0,04 x 0,04 x 0,30	inox	Lavanderia
ME-06	chuveiro, crivo Ø 0,24 (tipo a definir: de parede com braço ou ducha de teto; o modelo tem só o crivo)	0,24 x 0,24 x 0,03	preto	Banheiro
AC-01	nicho no box (vão útil e saliência: ver medidas)	vão 0,60 x 0,35 (L x H), de 1,10 a 1,45; saliente 0,06 no modelo; profundidade a definir	peça saliente verde	Banheiro
AC-02	papeleira de parede	0,12 x 0,06 x 0,08	preto	Banheiro
AC-04	toalheiro de argola / gancho	0,07 x 0,08 x 0,03	preto	Banheiro
AC-05	varal de teto (barras; indicativo)	conjunto 2,24 x 0,40 (L x P), a 2,45 do N.A.	inox	Lavanderia
AC-06	espelho retangular	0,55 x 0,03 x 0,85	LED em cima (indicativo)	Banheiro
BX-01	box: painel fixo de vidro temperado, h = 2,00, e vão livre	0,84 x 2,00 (L x H); espessura a definir	incolor	Banheiro
MC-01	gabinete suspenso de madeira (sob o tampo)	0,65 x 0,50 x 0,29	madeira	Banheiro
MC-03	armário aéreo de madeira	2,15 x 0,35 x 0,70	madeira	Lavanderia
MC-04	móvel de madeira sob o tampo	1,45 x 0,60 x 0,76	madeira	Lavanderia
MC-09	armário / torre de madeira até 2,40	0,60 x 0,60 x 2,40	madeira	Lavanderia
EQ-11	máquina lava e seca (equipamento indicativo)	0,65 x 0,65 x 0,85	a definir	Lavanderia

NOTAS E HIPÓTESES

1. Somente arquitetura: estrutura, contenção, impermeabilização e instalações são INDICATIVAS (projetos complementares, terceiros). Sem pontos de instalação: louças, metais e acessórios só como layout.
2. Cotas em metros com 2 casas, de face acabada a face acabada, fechando o total. Alturas a partir do piso acabado (N.A.: térreo ±0,00; subsolo gourmet -3,60); P.D. até o forro de madeira ou a laje (Q01 e cortes EX-004 a EX-006). Acessórios (papeleira, toalheiro, registro) cotados pelo eixo, na vertical e na horizontal.
3. Pisos PS conforme Q01/Q03 (EX-001/EX-002); RV, PT e BC conforme o quadro desta folha (textos do Q03 e dos cortes EX-004 a EX-006). Paginação de parede: módulo de referência (piso ou render; conferir as peças compradas); juntas de 2 mm nos retificados e 3 mm nos azulejos (fabricante); verticais pela coluna "Paginação" (marcada na vista), horizontais a partir do N.A.
4. Impermeabilização do box, das áreas molhadas e das paredes junto da contenção: projeto específico (NBR 9575, indicativa). Rebaixo, caimento e ralos (linear ou sifonado): hidrossanitário e impermeabilização.
5. Louças, metais, equipamentos e acessórios genéricos: modelo e acabamento a definir com a cliente; conferir os aparelhos comprados antes da marcenaria e das bancadas. Alturas: NBR 9050 como referência (sem barras).
6. Esquadrias: Q02 das EX-001/EX-002 e EX-014 a EX-016 (portas L x H = vão livre de passagem; janelas L x H = vão acabado; P = peitoril). Planos das vistas nas plantas ampliadas; o que o plano corta sai hachurado.
7. Padrões usuais adotados em 11/10/2026 (decisão do Cleber, reversíveis): piso equilibrado — partida no eixo que deixa os maiores recortes, mínimo de 1/3 da peça (também nas paredes), box com junta no vidro; tampo a 0,80 nos banheiros.

PENDÊNCIAS DO MODELO (decisão do Cleber)

8. Banheiro do subsolo gourmet: chuveiro de parede (ME-06) na parede sul (INF-CONT): sem braço nem ducha de teto no modelo (crivo solto a 2,05). Resolver no modelo (braço até a parede ou ducha de teto) e redesenhar as vistas.
9. Banheiro do subsolo gourmet: o "nicho" do modelo é uma peça saliente presa na contenção (não embutir nicho na contenção): levar para a parede interna ou manter saliente.
10. Banheiro do subsolo gourmet: piso do box no modelo em pastilha (padrão do mobiliário) x PS-05 no Q01/Q03: vale o Q03 (piso PS-05); o box encosta na contenção (aterro atrás): impermeabilização e drenagem da contenção antes do revestimento. Sem registro do chuveiro no modelo.

0 — 1 — 2 m

ESCALA GRÁFICA

REV.	DATA	DESCRIÇÃO	POR
R04	**08/10/2026**	**Emissão do executivo (Cleber): cotas 2 casas, cobertura EX-003, caixa 1 x 3.000 L e porta PC1**	**KMZERO**
R04	07/10/2026	Revisão 4 [redacted]lha clara, banheiros e pendentes da suíte	KMZERO
R03	07/10/2026	Revisão 3 (Cleber): entrada pela sala, cozinha nos fundos com a varanda	KMZERO
R02	06/10/2026	Revisão 2 (Cleber): varanda 1,50, subsolo gourmet aterrado, gourmet nos fundos, portas, interiores	KMZERO
R01	06/10/2026	Revisão 1 (Cleber): recuos 1,50, cozinha em U, piso +0,15, cobertura, subsolo gourmet	KMZERO
R00	29/09/2026	Emissão inicial — estudo preliminar	KMZERO

KMZERO | ENGENHARIA · ARQUITETURA

EMPREENDIMENTO	LOCAL	ETAPA
RESIDÊNCIA [redacted]	Rio Espera / MG	**PROJETO EXECUTIVO**

CONTEÚDO DA PRANCHA

VISTAS INTERNAS — LAVANDERIA E BANHEIRO DO SUBSOLO GOURMET

DESENHO	RESPONSÁVEL TÉCNICO	REGISTRO PROFISSIONAL
KMZERO	Kleber Vieira Martins · Arquitetura	ART/RRT a emitir

REVISÃO	DATA	ESCALA	UNIDADE	CÓDIGO DA PRANCHA
R04	07/10/2026	1:25	metro (m)	**AP-ARQ-EX-013**

Direitos autorais reservados à KMZERO. Cliente: [redacted]

AVISO: Projeto executivo de ARQUITETURA (somente arquitetura). Implantação, aterro e arrimos dependem do levantamento planialtimétrico; estrutura, contenção e instalações ficam com os projetos complementares (terceiros).