# QUADRO GERAL DE ESQUADRIAS E DETALHES TÍPICOS

ESCALA 1:5 / 1:10 · quadro geral sem escala · detalhes típicos indicativos com as medidas do modelo · cotas em metros (perfis em mm)


## QUADRO GERAL DE ESQUADRIAS

| Cód. | L (m) | H (m) | Peit. (m) | Tipologia | Material | Vidro | Ambientes | Qtd. | Folha |
|---|---|---|---|---|---|---|---|---|---|
| **TÉRREO** | | | | | | | | | |
| P1 | 0,90 | 2,30 | 0,00 | correr embutida (kit na parede) | madeira maciça (a definir) | — | Garagem / Sala de estar | 1 | EX-014 |
| P2 | 0,80 | 2,10 | 0,00 | correr aparente | madeira maciça · trilho preto aparente | — | Sala de estar / Hall íntimo | 1 | EX-014 |
| P3 | 0,80 | 2,10 | 0,00 | giro 1 folha | madeira semi-oca ou maciça (a definir) | — | Suíte / Hall íntimo | 1 | EX-014 |
| P4 | 0,90 | 2,10 | 0,00 | passagem livre (sem folha) | vão com guarnição de madeira | — | Suíte / Closet | 1 | EX-014 |
| P5 | 0,80 | 2,10 | 0,00 | correr embutida (kit na parede) | madeira maciça (a definir) | — | Closet / Banho da suíte | 1 | EX-014 |
| P6 | 0,80 | 2,10 | 0,00 | giro 1 folha | madeira semi-oca ou maciça (a definir) | — | Copa / Banheiro social | 1 | EX-014 |
| P7 | 0,80 | 2,10 | 0,00 | giro 1 folha | madeira semi-oca ou maciça (a definir) | — | Copa / Quarto 2 | 1 | EX-014 |
| P8 | 0,80 | 2,10 | 0,00 | giro 1 folha | madeira semi-oca ou maciça (a definir) | — | Cozinha / Quarto 3 | 1 | EX-014 |
| P9 | 2,35 | 2,40 | 0,00 | correr, folhas de vidro | vidro temperado incolor 8 mm + alumínio preto | temperado incolor 8 mm | Cozinha / Varanda | 1 | EX-014 |
| J1 | 1,90 | 2,40 | 0,30 | fixa (+ bandeira) | alumínio preto + vidro laminado 8 mm | laminado 8 mm | Suíte | 1 | EX-015 |
| J2 | 2,00 | 1,10 | 1,10 | correr 2 folhas | alumínio preto + vidro incolor 6 mm | incolor 6 mm | Suíte | 1 | EX-015 |
| J3 | 1,00 | 0,60 | 1,50 | basculante | alumínio preto + vidro mini-boreal 4 mm | mini-boreal 4 mm | Closet | 1 | EX-015 |
| J4 | 1,20 | 0,60 | 1,50 | maxim-ar | alumínio preto + vidro mini-boreal 4 mm | mini-boreal 4 mm | Banho da suíte | 1 | EX-015 |
| J5 | 1,20 | 0,60 | 1,50 | maxim-ar | alumínio preto + vidro mini-boreal 4 mm | mini-boreal 4 mm | Banheiro social | 1 | EX-015 |
| J6 | 2,00 | 1,10 | 1,10 | correr 2 folhas | alumínio preto + vidro incolor 6 mm | incolor 6 mm | Quarto 2 | 1 | EX-015 |
| J7 | 2,00 | 1,10 | 1,10 | correr 2 folhas | alumínio preto + vidro incolor 6 mm | incolor 6 mm | Quarto 3 | 1 | EX-015 |
| J8 | 2,30 | 1,80 | 0,60 | correr 2 folhas | alumínio preto + vidro laminado 8 mm | laminado 8 mm | Quarto 3 | 1 | EX-015 |
| J9 | 1,50 | 1,10 | 1,10 | correr 2 folhas | alumínio preto + vidro incolor 6 mm | incolor 6 mm | Cozinha | 1 | EX-015 |
| J10 | 1,80 | 1,10 | 1,10 | correr 2 folhas | alumínio preto + vidro incolor 6 mm | incolor 6 mm | Copa | 1 | EX-015 |
| J11 | 2,40 | 1,70 | 0,60 | correr 2 folhas + fixo inferior | alumínio preto + vidro laminado 8 mm | laminado 8 mm | Sala de estar | 1 | EX-015 |
| **SUBSOLO GOURMET — FASE 2 (obra posterior à casa, EX-002)** | | | | | | | | | |
| P10 | 0,95 | 2,10 | 0,00 | correr veneziana | madeira azul colonial · trilho preto | — | Lavanderia / Gourmet / cozinha de roça | 1 | EX-014 |
| P11 | 0,80 | 2,10 | 0,00 | giro 1 folha | madeira pintada azul colonial (gourmet de roça) | — | Banheiro / Gourmet / cozinha de roça | 1 | EX-014 |
| P12 | 0,80 | 2,10 | 0,00 | giro 1 folha | madeira pintada azul colonial (gourmet de roça) | — | Quarto de hóspedes / Gourmet / cozinha de roça | 1 | EX-014 |
| J12 | 1,10 | 0,60 | 1,50 | maxim-ar | alumínio preto + vidro mini-boreal 4 mm | mini-boreal 4 mm | Banheiro | 1 | EX-015 |
| J13 | 1,80 | 1,20 | 1,00 | correr 2 folhas | alumínio preto + vidro incolor 6 mm | incolor 6 mm | Quarto de hóspedes | 1 | EX-015 |
| **CASTELO DA CAIXA D'ÁGUA (cobertura, EX-003)** | | | | | | | | | |
| PC1 | 0,80 | 1,60 | 0,05 | giro 1 folha, metal vazado | alumínio preto brilhante + tela inox | — (vazada) | Castelo da caixa d'água / cobertura | 1 | EX-014 |
| VC1 | 0,60 | 0,30 | 1,30 | veneziana fixa | alumínio preto brilhante | — (sem vidro, lâminas) | Castelo da caixa d'água | 1 | EX-015 |
| | | | | TOTAL: 13 portas e 14 janelas | | | | 27 | |

Campos comuns iguais ao Q02 das EX-001/EX-002; PC1 e VC1 do castelo (EX-003): Peit. = soleira / peitoril acima do piso do castelo. Agrupado por pavimento; subsolo gourmet na FASE 2 (obra posterior), com Peit. medido do piso do subsolo gourmet. Elevação de cada tipo na folha indicada.


## 1 PEITORIL DE GRANITO COM PINGADEIRA

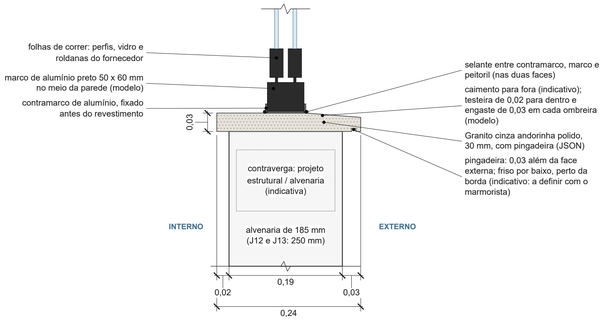ESCALA 1:5 · seção vertical pela janela de correr na parede externa (típico; J12 e J13 na parede de 250 mm): peitoril passante, pingadeira, caimento para fora, marco e contramarco





## 2 MARCO E CONTRAMARCO DE ALUMÍNIO — OMBREIRA E VERGA

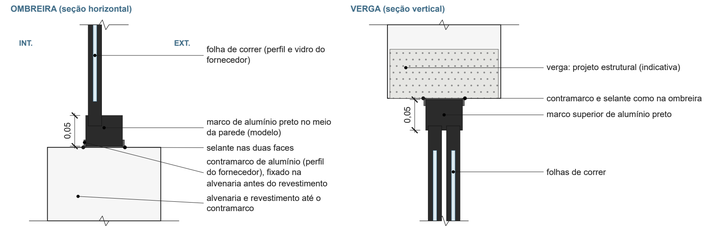ESCALA 1:5 · seção horizontal na ombreira e vertical na verga: contramarco antes do revestimento, marco no meio da parede, vedação com selante





## 3 SOLEIRA DE GRANITO — PORTAS INTERNAS

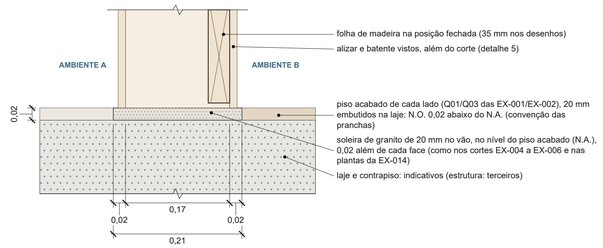ESCALA 1:5 · seção pelo vão: soleira no nível do piso acabado, na troca de piso





## 4 SOLEIRA DA PORTA DE CORRER DE VIDRO P9

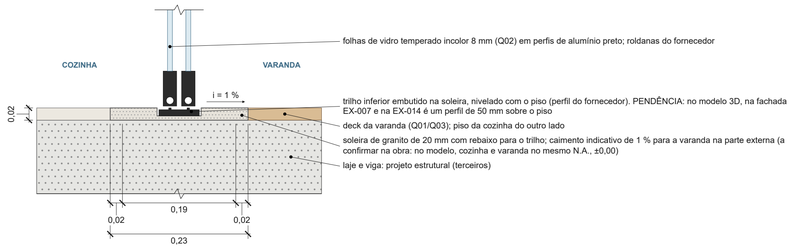ESCALA 1:5 · seção cozinha / varanda: trilho inferior, soleira de granito e caimento para a varanda





## 5 BATENTE E ALIZAR — PORTA DE GIRO DE MADEIRA

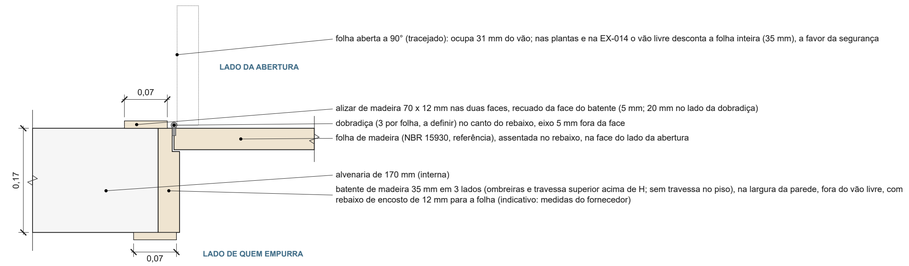ESCALA 1:5 · seção horizontal na ombreira da parede interna: batente de 35 mm, alizar de 70 mm nas duas faces, folha e dobradiça




## 6 PORTA DE CORRER EMBUTIDA (KIT NA PAREDE) — P1 E P5

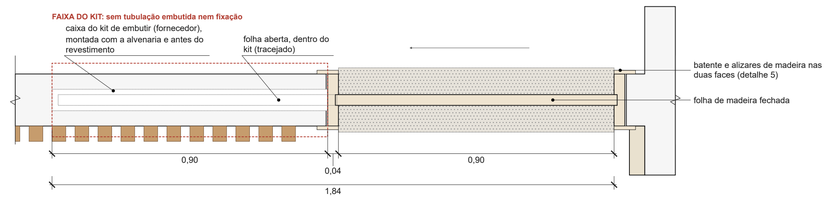
ESCALA 1:10 · planta: caixa do kit na parede interna, folha fechada e aberta, guias e alizares; faixa do kit sem tubulação e sem fixação




P1 cotada (kit 0,90, vão 0,90). P5: kit 0,80 e vão 0,80 (o mesmo detalhe). Ripado e pedra da garagem cortados (modelo).

## 7 PORTA DE CORRER APARENTE — TRILHO SUPERIOR (P2 E P10)

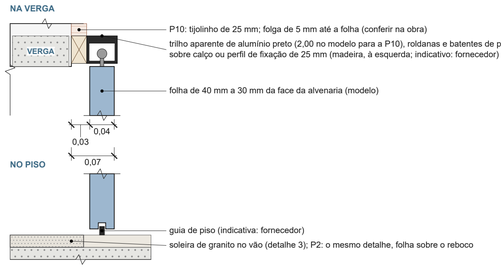ESCALA 1:5 · seção vertical: trilho de alumínio preto na verga, folha afastada da face acabada (P10 sobre o tijolinho), guia de piso




## ESCALAS GRÁFICAS




ESCALA 1:5 (detalhes 1 a 5 e 7)




ESCALA 1:10 (detalhe 6)

## LEGENDA

- Alvenaria cortada
- Concreto: laje e verga (indicativos, estrutura)
- Granito: peitoril e soleira
- Madeira: folha, batente, alizar e calço
- Alumínio preto: marco, contramarco, trilho
- Vidro
- Piso acabado (20 mm, no N.A.)
- Tijolinho (gourmet)
- Pedra cortada (revestimento da garagem)
- Ripado de madeira da garagem (cortado)
- Deck de madeira da varanda
- Selante
- Folha aberta / peça além do corte

## REMISSÃO

PC1 (porta de acesso à caixa d'água): detalhe 3 (CASTELO DA CAIXA D'ÁGUA — CORTE PELA PORTA PC1, 1:25) — EX-003; detalhe 4 (PORTA PC1 — VISTA EXTERNA, 1:20) — EX-003.

## NOTAS E HIPÓTESES

1. Quadro geral: mesmos campos do Q02 das EX-001/EX-002 (Cód., L, H, Peit., Tipologia, Material, Ambientes, Qtd.), mais a PC1 e a VC1 do castelo (EX-003), o vidro e a folha da elevação de cada tipo (EX-014 portas, EX-015 janelas), agrupados por pavimento (térreo, subsolo gourmet da FASE 2, castelo). L x H: portas = vão livre de passagem; janelas = vão acabado.
2. Detalhes típicos indicativos (NBR 6492): perfis, contramarco, ancoragens, vedações e desempenho pelo fornecedor (projeto de fabricação de terceiros; NBR 10821 e NBR 15930 como referência).
3. Vergas e contravergas: projeto estrutural e de alvenaria (terceiros); nos detalhes, só indicadas.
4. Janelas: vão acabado; portas: vão livre de passagem (nota 1); conferir na obra antes de fabricar; contramarco antes do revestimento; selante nas juntas entre marco, contramarco, peitoril e soleira.
5. Peitoril: Granito cinza andorinha polido, 30 mm, com pingadeira (JSON); J1 sem granito: a base da moldura grafite, com caimento e pingadeira, faz o peitoril; soleiras de granito de 20 mm no nível do piso acabado, 0,02 além de cada face (como nos cortes EX-004 a EX-006). Caimentos indicativos: confirmar na obra.
6. Padrões usuais adotados em 11/10/2026 (reversíveis): portas de giro com folha de 0,80 (padrão de mercado; vão livre de 0,77 com a folha aberta) e batente de madeira em 3 lados, sem travessa no piso; H = vão livre, com o batente acima de H; J2, J6, J7 e J10 com P = 1,10 e H = 1,10 (verga mantida em 2,20), proteção contra queda; J11 com faixa inferior fixa de vidro laminado 8 mm até 1,10; vidro laminado 8 mm de segurança em J1, J8 e J11; J1 com o peitoril na base da moldura grafite (caimento e pingadeira, sem granito).
7. Kits de porta de correr embutida e trilhos aparentes: modelo e fixação a definir com o fornecedor; faixa do kit sem tubulação nem fixação.
8. PC1: detalhes 3 (castelo, 1:25) e 4 (porta, 1:20) da EX-003.
9. Vidros conforme a NBR 7199; cores, ferragens e acabamentos a definir com a cliente.

**AVISO: Projeto executivo de ARQUITETURA (somente arquitetura). Implantação, aterro e arrimos dependem do levantamento planialtimétrico; estrutura, contenção e instalações ficam com os projetos complementares (terceiros).**

| REV. | DATA | DESCRIÇÃO | POR |
|---|---|---|---|
| **R04** | **08/10/2026** | **Emissão do executivo (Cleber): cotas 2 casas, cobertura EX-003, caixa 1 x 3.000 L e porta PC1** | **KMZERO** |
| R04 | 07/10/2026 | Revisão 4 [redacted] lha clara, banheiros e pendentes da suíte | KMZERO |
| R03 | 07/10/2026 | Revisão 3 (Cleber): entrada pela sala, cozinha nos fundos com a varanda | KMZERO |
| R02 | 06/10/2026 | Revisão 2 (Cleber): varanda 1,50, subsolo gourmet aterrado, gourmet nos fundos, portas, interiores | KMZERO |
| R01 | 08/10/2026 | Revisão 1 (Cleber): recuos 1,50, cozinha em U, piso +0,15, cobertura, subsolo gourmet | KMZERO |
| R00 | 29/09/2026 | Emissão inicial — estudo preliminar | KMZERO |

**KMZERO** | ENGENHARIA · ARQUITETURA

| EMPREENDIMENTO | LOCAL | ETAPA |
|---|---|---|
| **RESIDÊNCIA** [redacted] | Rio Espera / MG | **PROJETO EXECUTIVO** |

CONTEÚDO DA PRANCHA

**QUADRO GERAL DE ESQUADRIAS E DETALHES TÍPICOS**

| DESENHO | RESPONSÁVEL TÉCNICO | REGISTRO PROFISSIONAL |
|---|---|---|
| **KMZERO** | Kleber Vieira Martins · Arquitetura | ART/RRT a emitir |

| REVISÃO | DATA | ESCALA | UNIDADE | CÓDIGO DA PRANCHA |
|---|---|---|---|---|
| **R04** | 07/10/2026 | 1:5 / 1:10 | metro (m) | **AP-ARQ-EX-016** |

Direitos autorais reservados à KMZERO. Cliente: [redacted]