

PAGINAÇÃO DE PISO — TÉRREO E ÁREAS EXTERNAS (FRENTE E LATERAL LESTE)

ESCALA 1:50 · do muro da frente à borda da varanda · sem mobiliário · cotas e níveis em metros (±0,00 = piso acabado do térreo)

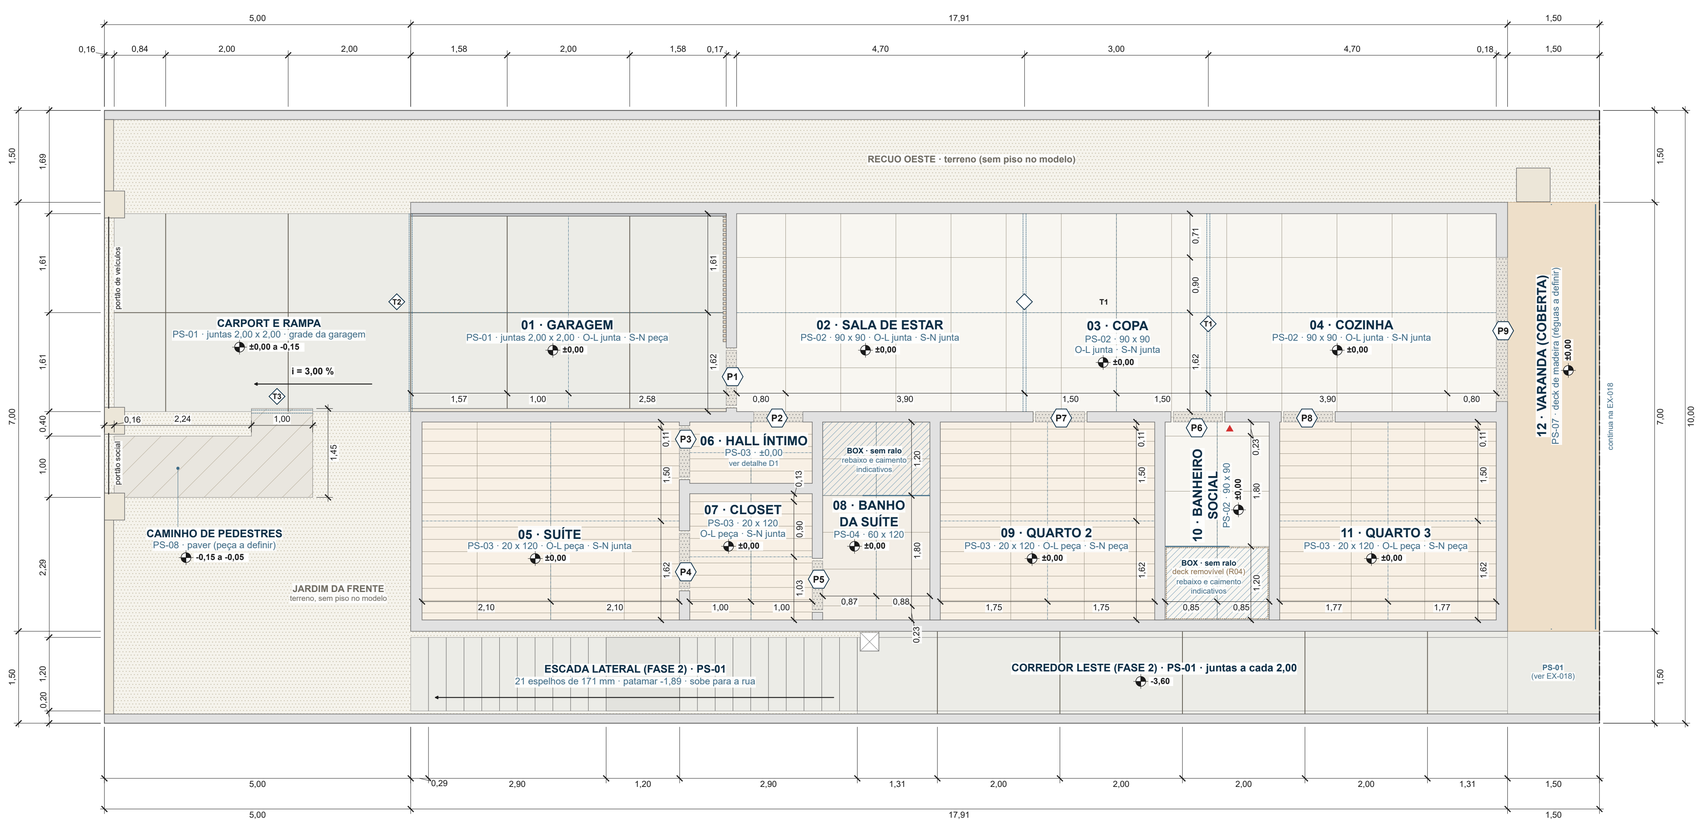

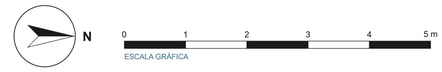


LEGENDA

- Parede cortada (leve, sem hachura)
- Junta da paginação (mesma posição das EX-001/002 e EX-010 a 013)
- Eixo de partida: junta no eixo ou peça centrada (regra equilibrada)
- Junta de movimentação do concreto (PS-01)
- Recorte abaixo de 1/3 da peça (ver Q07)
- Soleira de granito (quadro de soleiras)
- Transição sem porta (T1...): perfil ou arremate a definir
- Box: rebaixo e caimento indicativos (sem ralo)
- Deck de madeira (réguas indicativas, a definir)
- Terreno / jardim (sem piso no modelo)
- T1 — Transição (ver quadro de soleiras e transições)
- Piso paver PS-08 (peça e paginação a definir)
- Deck de madeira removível no box (R04; ver EX-010)
- Caixa de areia do condutor (indicativa; pluvial de terceiros)
- ±0,00 — N.A.: nível do piso acabado (±0,00 = térreo)
- PS-01 — Código do piso (quadro Q07 = Q01/Q03 das EX-001/002)

D1 RECORTES E SOLEIRAS — HALL ÍNTIMO, CLOSET, SUÍTE E BANHO DA SUÍTE

ESCALA 1:25

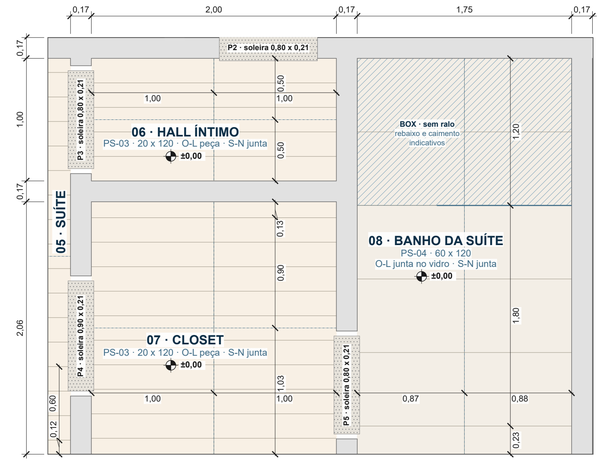

QUADRO DE SOLEIRAS E TRANSIÇÕES — TÉRREO

Ref.	Entre (piso de cada lado)	Vão (m)	Paredo (mm)	Soleira L x P (m)	Observação
P1	Garagem (PS-01) / Sala de estar (PS-02)	0,90	170	0,90 x 0,21	—
P2	Sala de estar (PS-02) / Hall íntimo (PS-03)	0,80	170	0,80 x 0,21	—
P3	Suíte (PS-03) / Hall íntimo (PS-03)	0,80	170	0,80 x 0,21	—
P4	Suíte (PS-03) / Closet (PS-03)	0,90	170	0,90 x 0,21	passagem sem folha
P5	Closet (PS-03) / Banho da suíte (PS-04)	0,80	170	0,80 x 0,21	—
P6	Copa (PS-02) / Banheiro social (PS-02)	0,80	170	0,80 x 0,21	—
P7	Copa (PS-02) / Quarto 2 (PS-03)	0,80	170	0,80 x 0,21	—
P8	Cozinha (PS-02) / Quarto 3 (PS-03)	0,80	170	0,80 x 0,21	—
P9	Cozinha (PS-02) / Varanda (PS-07)	2,35	185	2,35 x 0,23	trilho embutido (EX-016, det. 4)
T1	Sala / copa / cozinha (PS-02 contínuo)	—	—	—	sem perfil; juntas contínuas (campo único)
T2	Garagem / carport e rampa (PS-01)	—	—	—	junta de movimentação
T3	Rampa / caminho (PS-01 / PS-08)	—	—	—	guia ou perfil a definir

QUADRO DE PISOS — TÉRREO E ÁREAS EXTERNAS (Q07)

Nº	Ambiente / área	Cód.	Material e peça (cm)	Sentido	Partida	Área (m²)	Menor recorte (m)	Soleiras	Rodapé	N.A.	Observações
01	Garagem	PS-01	Concreto desempenado, juntas 2,00 x 2,00	—	O-L junta · S-N peça	16,63	1,58	P1	a definir	±0,00	—
02	Sala de estar	PS-02	Porcel. marmorizado 90 x 90 polido	—	O-L junta · S-N junta	15,18	0,72	P1, P2	a definir	±0,00	campo único com copa e cozinha
03	Copa	PS-02	Porcel. marmorizado 90 x 90 polido	—	O-L junta · S-N junta	9,69	0,72	P6, P7	a definir	±0,00	campo único com sala de estar e cozinha
04	Cozinha	PS-02	Porcel. marmorizado 90 x 90 polido	—	O-L junta · S-N junta	15,18	0,72	P8, P9	a definir	±0,00	campo único com sala de estar e copa
05	Suíte	PS-03	Porcel. amadeirado 20 x 120	120 no sentido sul-norte	O-L peça · S-N junta	13,57	0,12	P3, P4	a definir	±0,00	—
06	Hall íntimo	PS-03	Porcel. amadeirado 20 x 120	120 no sentido sul-norte	O-L peça · S-N junta	2,00	1,00	P2, P3	a definir	±0,00	—
07	Closet	PS-03	Porcel. amadeirado 20 x 120	120 no sentido sul-norte	O-L peça · S-N junta	4,12	0,13	P4, P5	a definir	±0,00	—
08	Banho da suíte	PS-04	Porcel. travertino 60 x 120 acetinado	120 no sentido sul-norte	O-L junta no vidro · S-N junta	5,65	0,23	P5	a definir	±0,00	box: rebaixo/caimento indicativos; junta na linha do vidro
09	Quarto 2	PS-03	Porcel. amadeirado 20 x 120	120 no sentido sul-norte	O-L peça · S-N peça	11,31	0,12	P7	a definir	±0,00	—
10	Banheiro social	PS-02	Porcel. marmorizado 90 x 90 polido	—	O-L junta no vidro · S-N junta	5,49	0,23 (< 1/3)	P6	a definir	±0,00	recorte < 1/3 (oeste) inevitável com a junta no vidro; box: rebaixo/caimento indicativos; junta na linha do vidro; deck de madeira removível sobre o PS-02 (R04, EX-010)
11	Quarto 3	PS-03	Porcel. amadeirado 20 x 120	120 no sentido sul-norte	O-L peça · S-N peça	11,42	0,12	P8	a definir	±0,00	—
12	Varanda (coberta)	PS-07	Deck de madeira (réguas a definir)	a definir	a definir	10,50	—	P9	—	±0,00	caimento: proj. impermeabilização
—	Carport e rampa	PS-01	Concreto desempenado, juntas 2,00 x 2,00	—	grade da garagem	15,63	0,84	—	—	±0,00 a -0,15	junta na linha da fachada; i = 3,00 %
—	Caminho de pedestres	PS-08	Piso paver externo (peça a definir)	a definir	a definir	3,69	—	—	—	-0,15 a -0,05	encontro com a rampa: a definir
—	Escada lateral (fase 2)	PS-01	Concreto desempenado (degraus)	—	—	8,75	—	—	—	±0,00 a -3,60	21 espelhos de 171 mm; área em projeção
—	Corredor leste (fase 2)	PS-01	Concreto desempenado, juntas a cada 2,00	—	equilibrada (pontas iguais)	12,67	1,31	—	—	-3,60	placas de 1,31 nas duas pontas; caixa de areia do CP-01 (indicativa, terceiros)

NOTAS E HIPÓTESES

1. Paginação equilibrada conforme o JSON (acabamentos.paginacao e paginacao_regra; padrão usual adotado em 11/10/2026, reversível): em cada ambiente e direção, a partida — junta no eixo ou peça centrada no eixo (traço-ponto) — que deixa os maiores recortes, sem recorte abaixo de 1/3 da peça quando possível; sala, copa e cozinha num campo só (eixo do campo, juntas contínuas); nos boxes, a junta na linha do vidro. Partida no Q07 por direção (O-L oeste-leste, S-N sul-norte): "junta", "peça" ou "vidro". Junta a menos de 0,01 da parede não é marcada (peça inteira; acerto no rejunte e no rodapé). Peças em centímetros (L x C): L no sentido oeste-leste e C no sentido sul-norte (na folha o norte fica à direita).
2. Cotas em metros com 2 casas, de face acabada a face acabada; as cadeias fecham o total. Níveis em metros (±0,00 = piso acabado do térreo); N.A. de cada ambiente no rótulo e no quadro Q07.
3. Menor recorte de cada ambiente cotado. Critério único de recorte em todas as folhas (pisos e paredes, EX-010 e EX-011 e folhas de piso): 1/3 da peça. Abaixo dele só onde a junta no vidro do box o impõe (triângulo; inevitável): banheiro social (oeste).
4. Conferir as peças compradas (medida real de fabricação, lote e tonalidade) antes de assentar. Juntas de 2 mm nos porcelanatos retificados e de 3 mm nos azulejos, conforme o fabricante (JSON acabamentos.juntas; padrão usual adotado em 11/10/2026); lajota e concreto conforme o fabricante; rejunte e espaçadores a definir com a cliente/fornecedor; perdas e sobras: quantitativo do fornecedor (áreas do Q07 medidas no modelo, sem perdas). Referências: NBR 13753 e NBR 13818.
5. Soleiras de granito de 20 mm no N.A., na largura do vão e 0,02 além de cada face da parede (EX-016, detalhes 3 e 4; P9 com o trilho embutido): medidas de fabricação no quadro de soleiras. Transição entre pisos sem porta: perfil ou arremate a definir (T1 a T3).
6. Rodapé: não definido no JSON (a definir com a cliente/fornecedor).
7. Concreto desempenado (PS-01): juntas de movimentação a cada 2,00 no máximo (JSON), pela mesma regra equilibrada (garagem; corredor leste com placas iguais nas duas pontas), também na linha da fachada (laje do térreo x carport e rampa); corte, profundidade e selante das juntas: fornecedor e projeto estrutural.
8. Caimentos da varanda e das áreas externas: a definir no projeto de impermeabilização (no modelo os pisos são planos; a EX-016, detalhe 4, indica 1,00 % junto à P9, indicativo). Rampa e carport: ±0,00 na fachada a -0,15 na divisa (i = 3,00 %, perfil do modelo). Box: rebaixo e caimento indicativos (ver EX-010); no box do banheiro social, deck de madeira removível sobre o piso (R04; réguas a definir). Sem ralos nem pontos de instalação (projetos complementares, terceiros).
9. Escada lateral e corredor leste: FASE 2 (obra posterior), chegada no N.A. -3,60; continuação na EX-018. Faixas entre o corredor leste, a gourmet e o deck: concreto desempenado PS-01 continuando o corredor até o deck e ao longo dele (padrão usual adotado em 11/10/2026, reversível), 5,73 m² no modelo (Q07 da EX-018).
10. Somente arquitetura; mobiliário não desenhado. Áreas, níveis e peças do modelo e do JSON [redacted].

AVISO: Projeto executivo de ARQUITETURA (somente arquitetura). Implantação, aterro e arrimos dependem do levantamento planialtimétrico; estrutura, contenção e instalações ficam com os projetos complementares (terceiros).

REV.	DATA	DESCRIÇÃO	POR
R04	**08/10/2026**	**Emissão do executivo (Cleber): cotas 2 casas, cobertura EX-003, caixa 1 x 3.000 L e porta PC1**	**KMZERO**
R04	07/10/2026	Revisão 4 [redacted]lha clara, banheiros e pendentes da suíte	KMZERO
R03	07/10/2026	Revisão 3 (Cleber): entrada pela sala, cozinha nos fundos com a varanda	KMZERO
R02	06/10/2026	Revisão 2 (Cleber): varanda 1,50, subsolo gourmet aterrado, gourmet nos fundos, portas, interiores	KMZERO
R01	06/10/2026	Revisão 1 (Cleber): recuos 1,50, cozinha em U, piso +0,15, cobertura, subsolo gourmet	KMZERO
R00	29/09/2026	Emissão inicial — estudo preliminar	KMZERO

KMZERO | ENGENHARIA · ARQUITETURA

EMPREENDIMENTO: **RESIDÊNCIA** [redacted]	LOCAL: Rio Espera / MG	ETAPA: **PROJETO EXECUTIVO**

CONTEÚDO DA PRANCHA: **PAGINAÇÃO DE PISO — TÉRREO E ÁREAS EXTERNAS**

DESENHO	RESPONSÁVEL TÉCNICO	REGISTRO PROFISSIONAL
KMZERO	Kleber Vieira Martins · Arquitetura	ART/RRT a emitir

REVISÃO	DATA	ESCALA	UNIDADE	CÓDIGO DA PRANCHA
R04	07/10/2026	1:50 / 1:25	metro (m)	**AP-ARQ-EX-017**

Direitos autorais reservados à KMZERO. Cliente: [redacted]