

PAGINAÇÃO DE PISO — SUBSOLO GOURMET E ÁREA DA PISCINA (FASE 2)

ESCALA 1:50 · piso do subsolo gourmet -3,60 · sem mobiliário · cotas e níveis em metros (±0,00 = piso acabado do térreo)

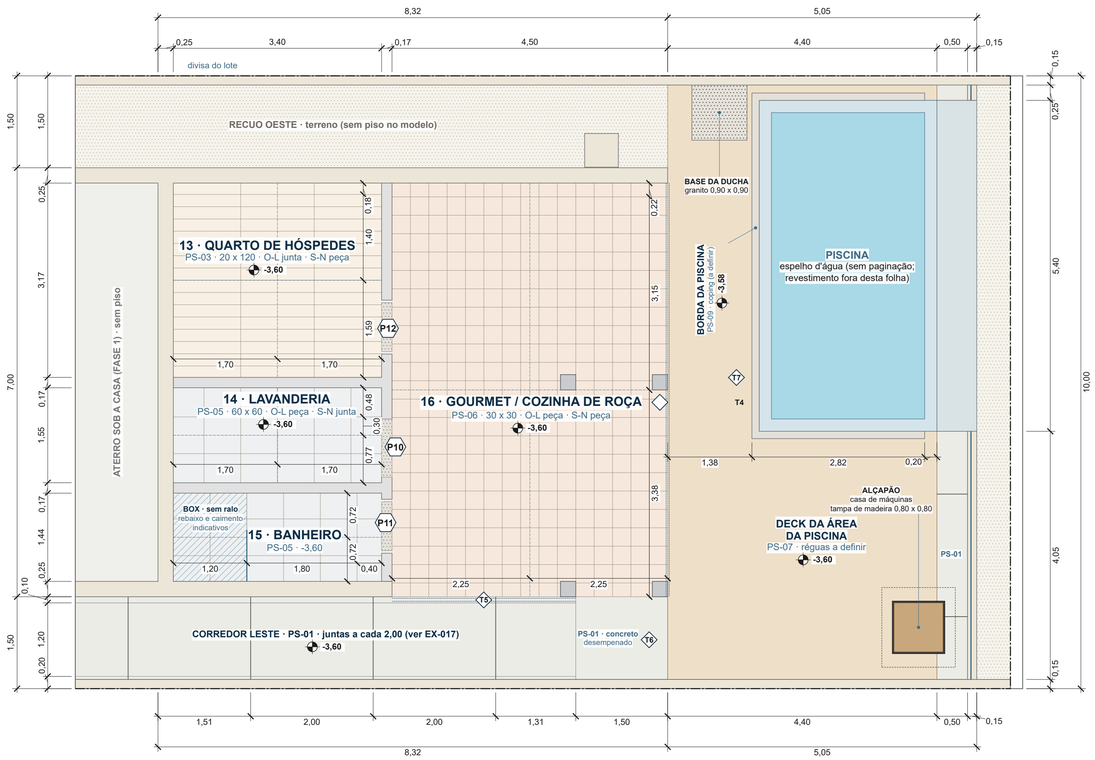


D2 ENCONTROS DA GOURMET COM O DECK E O CORREDOR LESTE

ESCALA 1:25

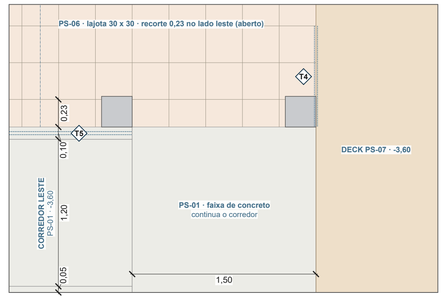

D3 BORDA DA PISCINA (CANTO SUDESTE)

ESCALA 1:25

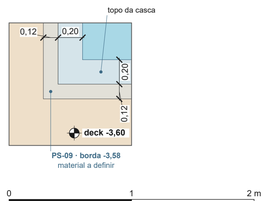

ESCALA GRÁFICA 1:25 (detalhes D2 e D3)

N

0 1 2 3 4 5 m

ESCALA GRÁFICA

LEGENDA

- Parede cortada (leve, sem hachura)
- Junta da paginação (mesma posição das EX-001/002 e EX-010 a 013)
- Eixo de partida: junta no eixo ou peça centrada (regra equilibrada)
- Junta de movimentação do concreto (PS-01)
- Recorte abaixo de 1/3 da peça (ver Q07)
- Soleira de granito (quadro de soleiras)
- Transição sem porta (T1...): perfil ou arremate a definir
- Box: rebaixo e caimento indicativos (sem ralo)
- Deck de madeira (réguas indicativas, a definir)
- Terreno / jardim (sem piso no modelo)
- T1 — Transição (ver quadro de soleiras e transições)
- ±0,00 — N.A.: nível do piso acabado (±0,00 = térreo)
- PS-01 — Código do piso (quadro Q07 = Q01/Q03 das EX-001/002)

QUADRO DE SOLEIRAS E TRANSIÇÕES — SUBSOLO GOURMET

Ref.	Entre (piso de cada lado)	Vão (m)	Parede (mm)	Soleira L x P (m)	Observação
P10	Lavanderia (PS-05) / Gourmet / cozinha de roça (PS-06)	0,95	170	0,95 x 0,21	—
P11	Banheiro (PS-05) / Gourmet / cozinha de roça (PS-06)	0,80	170	0,80 x 0,21	—
P12	Quarto de hóspedes (PS-03) / Gourmet / cozinha de roça (PS-06)	0,80	170	0,80 x 0,21	—
T4	Gourmet / deck (PS-06 / PS-07)	—	—	—	lado aberto: perfil a definir
T5	Gourmet / corredor leste (PS-06 / PS-01)	—	—	—	PS-01 contínuo até a gourmet: perfil a definir
T6	Corredor leste / deck (PS-01 / PS-07)	—	—	—	PS-01 contínuo até o deck: perfil a definir
T7	Deck / borda da piscina (PS-07 / PS-09)	—	—	—	borda 0,02 acima do deck

QUADRO DE PISOS — SUBSOLO GOURMET E ÁREA DA PISCINA (Q07)

Nº	Ambiente / área	Cód.	Material e peça (cm)	Sentido	Partida	Área (m²)	Menor recorte (m)	Soleiras	Rodapé	N.A.	Observações
13	Quarto de hóspedes	PS-03	Porcel. amadeirado 20 x 120	120 no sentido sul-norte	O-L junta · S-N peça	10,78	0,19	P12	a definir	-3,60	—
14	Lavanderia	PS-05	Porcel. cimentício 60 x 60 acetinado	—	O-L peça · S-N junta	5,27	0,48	P10	a definir	-3,60	—
15	Banheiro	PS-05	Porcel. cimentício 60 x 60 acetinado	—	O-L peça · S-N junta no vidro	4,90	0,40	P11	a definir	-3,60	box: rebaixo/caimento indicativos; junta na linha do vidro
16	Gourmet / cozinha de roça	PS-06	Lajota cerâmica rústica 30 x 30	—	O-L peça · S-N peça	30,38	0,23	P10, P11, P12	a definir	-3,60	—
—	Deck da área da piscina	PS-07	Deck de madeira (réguas a definir)	a definir	a definir	26,97	—	—	—	-3,60	caimento: proj. impermeabilização
—	Borda da piscina	PS-09	Borda (coping), material a definir	—	—	1,32	—	—	—	-3,58	faixa sobre o deck (detalhe D3)
—	Corredor leste (trecho)	PS-01	Concreto desempenado, juntas a cada 2,00	—	ver EX-017	ver EX-017	ver EX-017	—	—	-3,60	quadro na EX-017
—	Faixas de concreto (fase 2)	PS-01	Concreto desempenado, juntas a cada 2,00	—	equilibrada	5,73	—	—	—	-3,60	continua o corredor até o deck e ao longo dele (padrão usual)

RESUMO DAS ÁREAS POR CÓDIGO — EX-017 E EX-018 (sem perdas)

Cód.	Material e peça (cm)	Onde	Área total (m²)
PS-01	Concreto desempenado, juntas 2,00 x 2,00	garagem, carport e rampa, corredor leste, faixas de concreto	50,67 + escada 8,75 (projeção)
PS-02	Porcel. marmorizado 90 x 90 polido	sala de estar, copa, cozinha, banheiro social	45,54
PS-03	Porcel. amadeirado 20 x 120	suíte, hall íntimo, closet, quarto 2, quarto 3, quarto de hóspedes	53,19
PS-04	Porcel. travertino 60 x 120 acetinado	banho da suíte	5,65
PS-05	Porcel. cimentício 60 x 60 acetinado	lavanderia, banheiro	10,17
PS-06	Lajota cerâmica rústica 30 x 30	gourmet / cozinha de roça	30,38
PS-07	Deck de madeira (varanda e área da piscina)	varanda, deck da área da piscina (inclui 1,32 sob a borda PS-09)	37,47
PS-08	Piso paver externo (caminho de pedestres; peça e assentamento a definir)	caminho de pedestres	3,69
PS-09	Borda da piscina (coping; material e peça a definir)	borda da piscina (sobre o deck PS-07)	1,32

NOTAS E HIPÓTESES

1. FASE 2 (obra posterior à casa). Paginação equilibrada conforme o JSON (acabamentos.paginacao e paginacao_regra; padrão usual adotado em 11/10/2026, reversível): em cada direção, a partida — junta no eixo ou peça centrada (traço-ponto) — que deixa os maiores recortes; nos boxes, a junta na linha do vidro. As mesmas juntas da EX-002 e das plantas ampliadas EX-012 e EX-013; peças em centímetros (L oeste-leste x C sul-norte); partida no Q07 por direção (O-L, S-N).
2. Cotas em metros com 2 casas; as cadeias fecham o total. Níveis em metros (±0,00 = piso acabado do térreo): subsolo gourmet, deck e corredor leste em -3,60; borda da piscina em -3,58.
3. Deck de madeira da área da piscina e da varanda (PS-07): largura, comprimento, sentido e fixação das réguas a definir com a cliente/fornecedor (o JSON não define; a hachura segue as EX-001/EX-002).
4. Borda da piscina (PS-09) e topo da casca: material, largura e pingadeira a definir (detalhe D3). Revestimento interno da piscina fora desta folha.
5. Encontros da lajota da gourmet com o deck e com o corredor leste (lados abertos, sem porta): perfil ou arremate a definir (T4 a T7; detalhe D2). Faixas entre o corredor leste, a gourmet e o deck: concreto desempenado PS-01 continuando o corredor até o deck e ao longo dele (padrão usual adotado em 11/10/2026, reversível), 5,73 m² no modelo (Q07 da EX-018). Menor recorte cotado; critério único de recorte de 1/3 da peça (o mesmo das plantas ampliadas EX-012 e EX-013).
6. Conferir as peças compradas antes de assentar; juntas de 2 mm nos porcelanatos retificados e de 3 mm nos azulejos, conforme o fabricante (JSON acabamentos.juntas); lajota e concreto conforme o fabricante; perdas pelo fornecedor (áreas do Q07 medidas no modelo, sem perdas). Referências: NBR 13753 e NBR 13818. Rodapé a definir. No resumo por código, o total é a soma exata do modelo, arredondada (pode diferir 0,01 da soma das linhas do Q07); a borda da piscina fica sobre o deck: os 1,32 m² dela estão também no total do deck.
7. Caimentos do deck, do corredor e da área da piscina: projeto de impermeabilização e drenagem (terceiros); sem ralos nem pontos de instalação. Box: rebaixo e caimento indicativos (ver EX-013).
8. Escada lateral e corredor leste: paginação e quadro na EX-017. Casa de máquinas enterrada sob o deck, com alçapão de madeira em quadro de alumínio.
9. Somente arquitetura; mobiliário não desenhado. Áreas e níveis do modelo e do JSON [redacted]

AVISO: Projeto executivo de ARQUITETURA (somente arquitetura). Implantação, aterro e arrimos dependem do levantamento planialtimétrico; estrutura, contenção e instalações ficam com os projetos complementares (terceiros).

REV.	DATA	DESCRIÇÃO	POR
R04	**08/10/2026**	**Emissão do executivo (Cleber): cotas 2 casas, cobertura EX-003, caixa 1 x 3.000 L e porta PC1**	**KMZERO**
R04	07/10/2026	Revisão 4 [redacted]lha clara, banheiros e pendentes da suíte	KMZERO
R03	07/10/2026	Revisão 3 (Cleber): entrada pela sala, cozinha nos fundos com a varanda	KMZERO
R02	06/10/2026	Revisão 2 (Cleber): varanda 1,50, subsolo gourmet aterrado, gourmet nos fundos, portas, interiores	KMZERO
R01	06/10/2026	Revisão 1 (Cleber): recuos 1,50, cozinha em U, piso +0,15, cobertura, subsolo gourmet	KMZERO
R00	29/09/2026	Emissão inicial — estudo preliminar	KMZERO

KMZERO | ENGENHARIA · ARQUITETURA

EMPREENDIMENTO	LOCAL	ETAPA
RESIDÊNCIA [redacted]	Rio Espera / MG	**PROJETO EXECUTIVO**

CONTEÚDO DA PRANCHA

PAGINAÇÃO DE PISO — SUBSOLO GOURMET E ÁREA DA PISCINA

DESENHO	RESPONSÁVEL TÉCNICO	REGISTRO PROFISSIONAL
KMZERO	Kleber Vieira Martins · Arquitetura	ART/RRT a emitir

REVISÃO	DATA	ESCALA	UNIDADE	CÓDIGO DA PRANCHA
R04	07/10/2026	1:50 / 1:25	metro (m)	**AP-ARQ-EX-018**

Direitos autorais reservados à KMZERO. Cliente: [redacted]