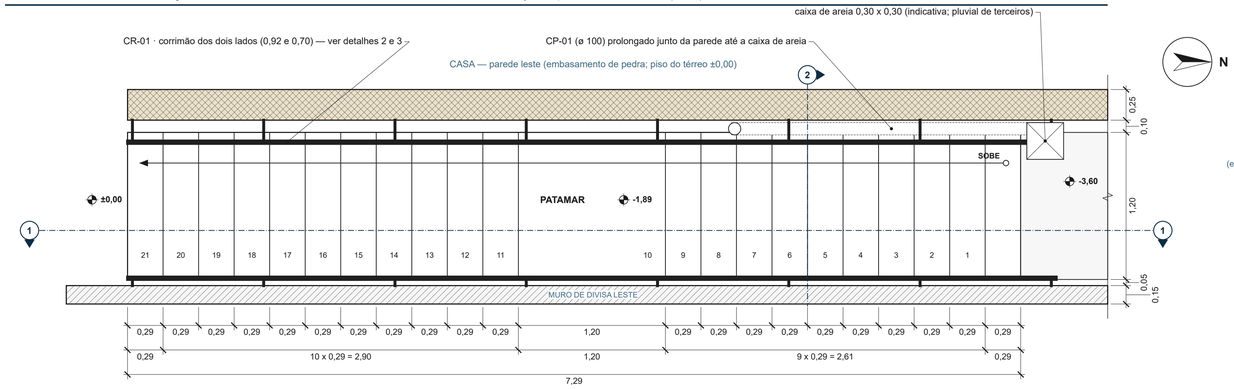
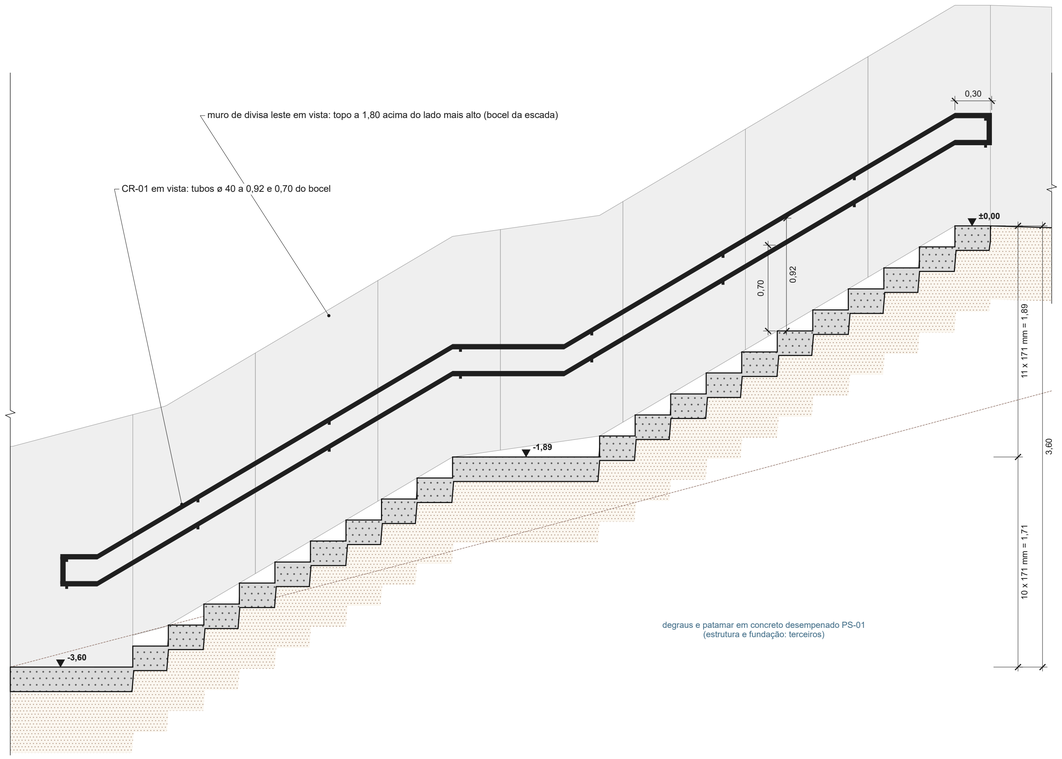
# PLANTA DA ESCADA LATERAL

ESCALA 1:25 · vista de cima · degraus numerados no sentido da subida · cotas em metros · níveis em relação ao piso acabado do térreo (±0,00)



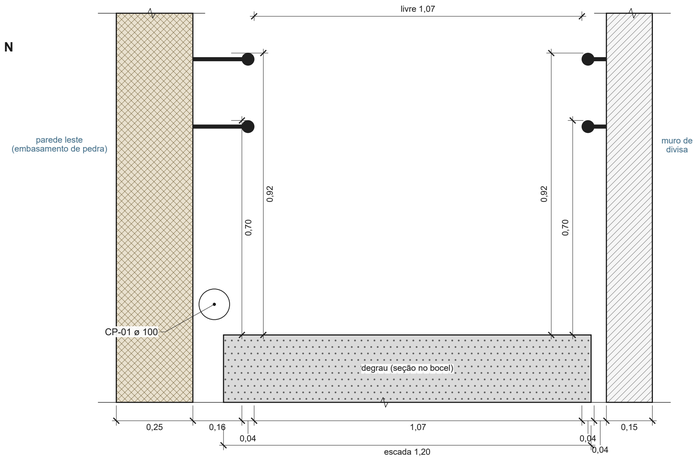

# CORTE 1 — LONGITUDINAL DA ESCADA

ESCALA 1:25 · plano no eixo da escada, vista para leste · corrimão e muro em vista



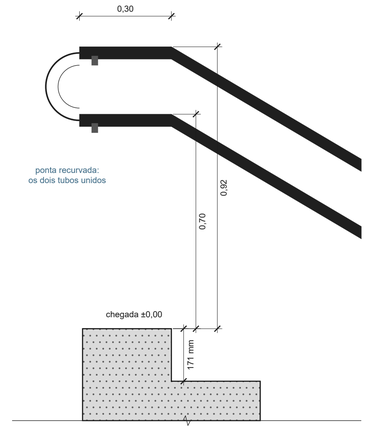

## 2 SEÇÃO TRANSVERSAL NO BOCEL (CORRIMÃOS)

ESCALA 1:10 · no espelho 6, vista para o norte (descida)



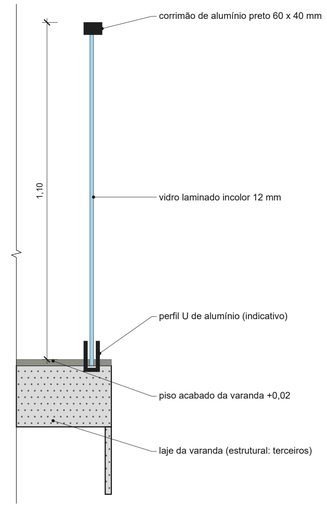

## 3 EXTREMIDADE DO CORRIMÃO (TOPO)

ESCALA 1:10 · vista para leste



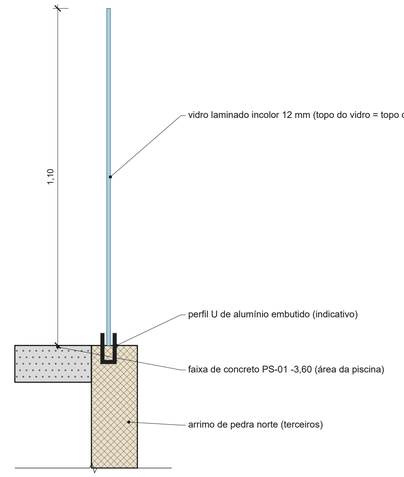

## 4 GC-01 — SEÇÃO NA BORDA DA VARANDA

ESCALA 1:10 · vista para leste



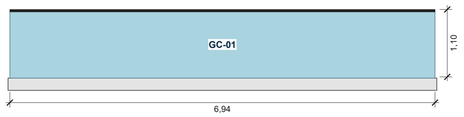

## 5 GC-02 — SEÇÃO NO ARRIMO NORTE

ESCALA 1:10 · área da piscina, vista para leste



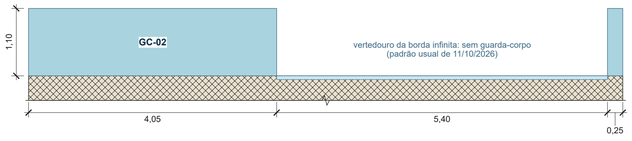

## 6 GC-01 — VISTA NORTE (VARANDA)

ESCALA 1:50 · olhando para o sul




## 7 GC-02 — VISTA NORTE (ÁREA DA PISCINA)

ESCALA 1:50 · olhando para o sul




## LEGENDA

- Concreto cortado (degraus, patamar, lajes, faixas)
- Pedra cortada (embasamento da casa, arrimo)
- Alvenaria cortada (muro de divisa)
- Alumínio preto (corrimãos, perfis, suportes)
- Vidro laminado incolor
- Elemento em vista, além do plano
- Terreno acabado (linha cheia) e natural (tracejada)

0 0,5 1 1,5 2 m — ESCALA GRÁFICA 1:25

0 0,25 0,5 m — ESCALA GRÁFICA 1:10

## NOTAS E HIPÓTESES

1. Somente arquitetura. Metros com 2 casas; espelhos, tubos e vidros em mm. Níveis em relação ao piso acabado do térreo (±0,00). Ver também EX-006 (corte CC), EX-009 (fachada leste), EX-004/005 e EX-017/018.
2. Escada lateral (fase 2): 21 espelhos de 171 mm e pisos de 0,29 (2E + P = 0,63), em 2 lances (11 + 10) com patamar de 1,20 em -1,89; largura de 1,20; concreto desempenado PS-01. Sinalização visual na borda dos pisos (NBR 9050): a definir com a cliente.
3. CR-01 (tubo de alumínio ø 40 mm com pintura eletrostática preta; suportes de alumínio a cada 1,20 no máximo, fixados na parede leste da casa e no muro de divisa): a 0,92 e 0,70 do bocel, na vertical, até a geratriz superior; prolongamento horizontal de 0,30 nas pontas, que são recurvadas; 0,04 do muro e 0,16 da parede leste (folga do CP-01); livre entre corrimãos 1,07 (padrão de 09/10/2026, NBR 9050:2020, 6.9).
4. GC-01 e GC-02: 1,10 no mínimo acima do piso acabado (NBR 14718), vidro laminado (NBR 7199). O GC-02 fica nos trechos laterais; o vertedouro da borda infinita fica sem guarda-corpo (padrão usual de 11/10/2026).
5. CP-01 prolongado até a caixa de areia de 0,30 x 0,30 no pé da escada: indicativo (pluvial de terceiros, EX-003).
6. Fixação dos perfis U e dos suportes do corrimão: indicativa. O fornecedor dimensiona; a borda da laje, o muro e a base da escada ficam com o projeto estrutural (terceiros).
7. Iluminação da escada (balizadores ou arandelas): fora do escopo de arquitetura (projeto elétrico de terceiros).

## QUADRO DA ESCADA LATERAL (Q10)

| Item | Valor |
|---|---|
| Espelhos | 21 x 171 mm (11 + 10 por lance, de cima para baixo) |
| Piso (profundidade) | 0,29 |
| 2E + P | 0,63 (NBR 9050: 0,63 a 0,65) |
| Patamar | 1,20 x 1,20, nível -1,89 |
| Largura da escada | 1,20 (livre entre corrimãos 1,07) |
| Desnível vencido | 3,60 (±0,00 a -3,60) |
| Comprimento em planta | 7,29 |
| Piso dos degraus | concreto desempenado PS-01 (fase 2) |
| Corrimão | CR-01 dos dois lados, a 0,92 e 0,70 do bocel |

## QUADRO DE GUARDA-CORPOS E CORRIMÃOS (Q11)

| Cód. | Elemento | Altura | Extensão | Material | Norma |
|---|---|---|---|---|---|
| CR-01 | Corrimão duplo da escada lateral (dos dois lados) | 0,92 e 0,70 (bocel) | 2 x 7,60 (em planta) | tubo de alumínio ø 40 mm, pintura eletrostática preta; suportes a cada 1,20 no máximo | NBR 9050:2020, 6.9 |
| GC-01 | Guarda-corpo da varanda | 1,10 (piso acabado) | 6,94 + 1,43 + 1,43 | vidro laminado 12 mm (6 + 6) em perfil U de alumínio; corrimão de alumínio preto 60 x 40 mm | NBR 14718 e NBR 7199 |
| GC-02 | Guarda-corpo da área da piscina (trechos laterais do vertedouro) | 1,10 (piso acabado) | 4,05 + 0,25 | vidro laminado 12 mm (6 + 6) em perfil U de alumínio embutido no piso | NBR 14718 e NBR 7199 |

**AVISO: Projeto executivo de ARQUITETURA (somente arquitetura). Implantação, aterro e arrimos dependem do levantamento planialtimétrico; estrutura, contenção e instalações ficam com os projetos complementares (terceiros).**

| REV. | DATA | DESCRIÇÃO | POR |
|---|---|---|---|
| **R04** | **08/10/2026** | **Emissão do executivo (Cleber): cotas 2 casas, cobertura EX-003, caixa 1 x 3.000 L e porta PC1** | **KMZERO** |
| R04 | 07/10/2026 | Revisão 4 [redacted]lha clara, banheiros e pendentes da suíte | KMZERO |
| R03 | 07/10/2026 | Revisão 3 (Cleber): entrada pela sala, cozinha nos fundos com a varanda | KMZERO |
| R02 | 06/10/2026 | Revisão 2 (Cleber): varanda 1,50, subsolo gourmet aterrado, gourmet nos fundos, portas, interiores | KMZERO |
| R01 | 06/10/2026 | Revisão 1 (Cleber): recuos 1,50, cozinha em U, piso +0,15, cobertura, subsolo gourmet | KMZERO |
| R00 | 29/09/2026 | Emissão inicial — estudo preliminar | KMZERO |

**KMZERO** | ENGENHARIA · ARQUITETURA

| EMPREENDIMENTO | LOCAL | ETAPA |
|---|---|---|
| **RESIDÊNCIA [redacted]** | Rio Espera / MG | **PROJETO EXECUTIVO** |

CONTEÚDO DA PRANCHA

## ESCADA LATERAL E GUARDA-CORPOS

| DESENHO | RESPONSÁVEL TÉCNICO | REGISTRO PROFISSIONAL |
|---|---|---|
| **KMZERO** | Kleber Vieira Martins · Arquitetura | ART/RRT a emitir |

| REVISÃO | DATA | ESCALA | UNIDADE | CÓDIGO DA PRANCHA |
|---|---|---|---|---|
| **R04** | 07/10/2026 | 1:25 / 1:10 / 1:50 | metro (m) | **AP-ARQ-EX-020** |

Direitos autorais reservados à KMZERO. Cliente: [redacted]