

PLANTA DO FECHAMENTO DA FRENTE

ESCALA 1:25 · plano de corte a 1,20 da calçada · cotas em metros · níveis em relação ao piso acabado do térreo (±0,00)

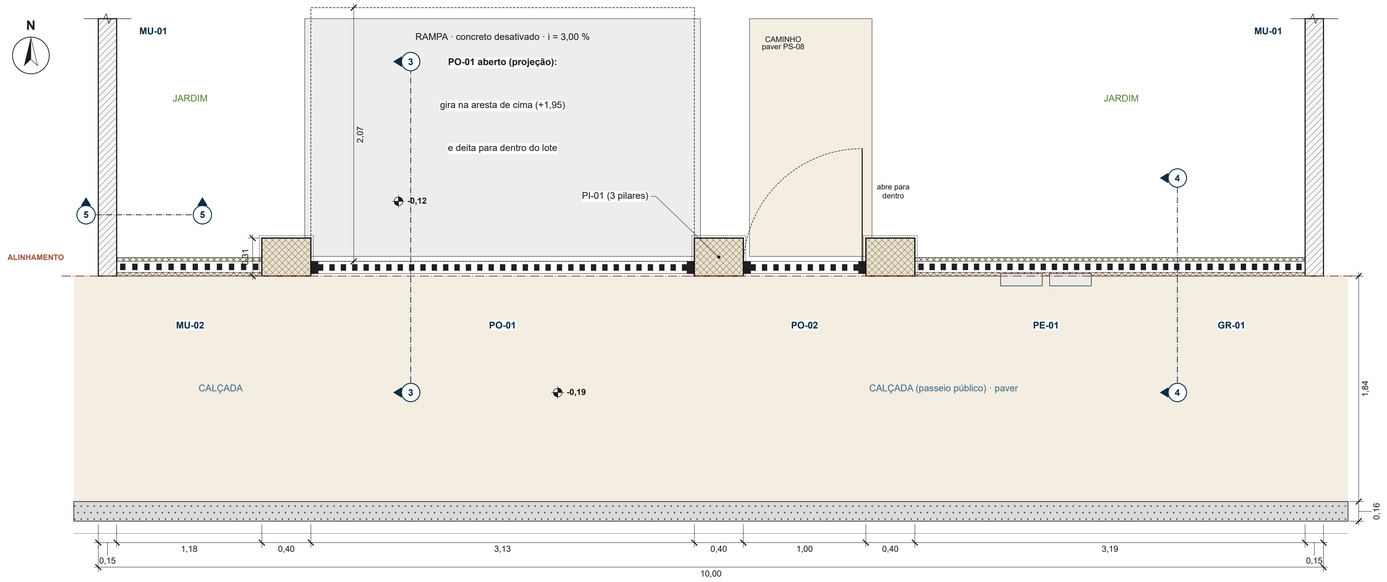


ELEVAÇÃO DO FECHAMENTO DA FRENTE

ESCALA 1:25 · vista da rua (olhando para o norte) · a casa ao fundo fica na EX-007

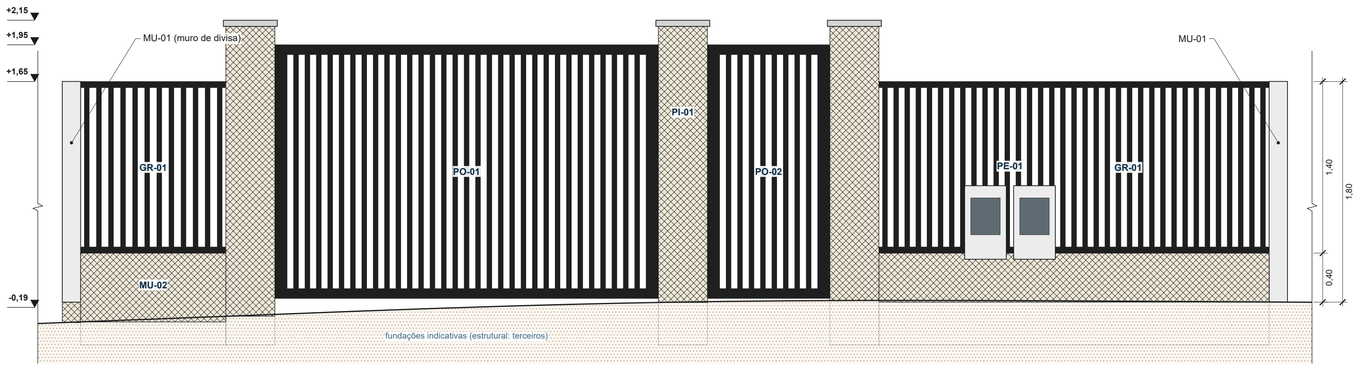


3 PO-01 — CORTE PELO PORTÃO BASCULANTE

ESCALA 1:25 · vista para oeste

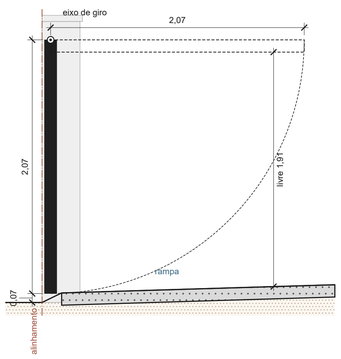


4 MURETA E GRADIL — SEÇÃO

ESCALA 1:10 · vista para oeste

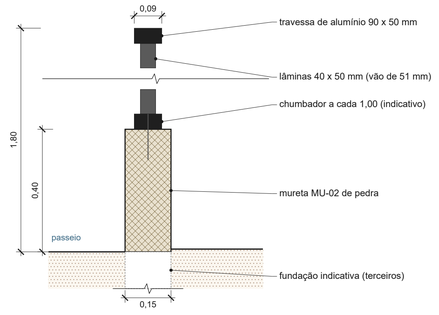


5 MURO DE DIVISA SOBRE O ARRIMO

ESCALA 1:25 · y = -14,50 (oeste), vista para o norte

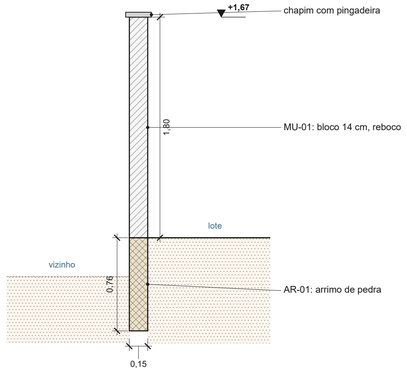


6 MURO DE DIVISA OESTE — FACE INTERNA

ESCALA 1:100 · olhando para oeste · casa omitida

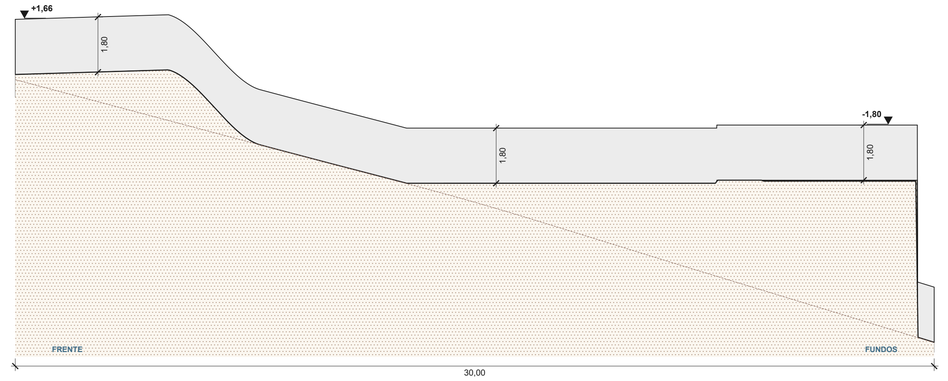

7 MURO DE DIVISA LESTE — FACE INTERNA

ESCALA 1:100 · olhando para leste · casa omitida; escada lateral em perfil

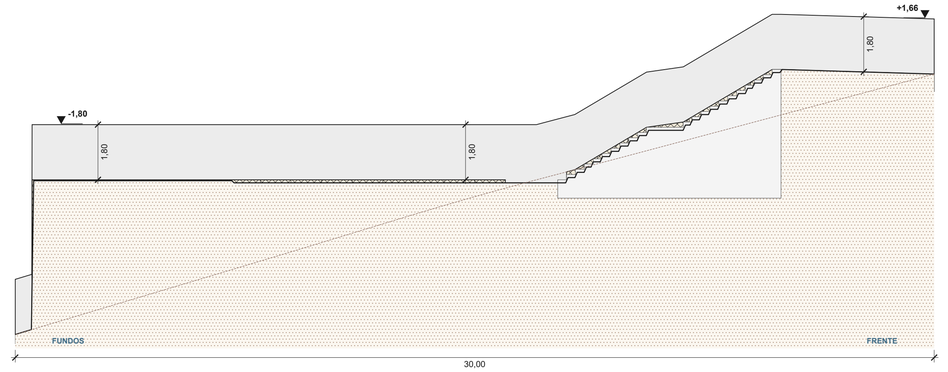

LEGENDA

- Pedra cortada (pilares, mureta, arrimo)
- Pedra em vista
- Alvenaria cortada (muro de divisa)
- Muro rebocado em vista
- Concreto cortado
- Alumínio preto brilhante (portões, gradil)
- Elemento em vista, além do plano
- Terreno do lote (linha cheia) e do vizinho (tracejada)

0 0,5 1 1,5 2 m — ESCALA GRÁFICA 1:25

0 0,25 0,5 m — ESCALA GRÁFICA 1:10

0 2 4 6 8 m — ESCALA GRÁFICA 1:100

QUADRO DE MUROS E PORTÕES (Q12)

Cód.	Elemento	Dimensões	Material e acabamento
MU-01	Muro de divisa (oeste e leste)	0,15; 1,80 acima do lado mais alto	bloco de concreto 14 cm, reboco e pintura cinza-claro; chapim com pingadeira
AR-01	Arrimo de pedra (sob os muros de divisa)	onde o muro retém terra (ver 5, 6 e 7)	pedra mineira; espessura, fundação e dreno: estrutural (terceiros)
MU-02	Mureta da frente	0,15; 0,40 acima da calçada	pedra mineira, 0,15 de espessura
PI-01	Pilares do portão (3)	0,40 x 0,31; topo a 2,30 da calçada	pedra mineira; capa de concreto 0,05 com pingadeira
GR-01	Gradil da frente	até 1,80 da calçada	alumínio preto brilhante: lâminas 40 x 50 mm, travessas 90 x 50 mm
PO-01	Portão de veículos basculante	vão 3,13 x 2,10	alumínio preto brilhante: quadro 60 x 100 mm, lâminas 40 x 50 mm
PO-02	Portão social de giro	vão 1,00 x 2,10	o mesmo desenho do PO-01; abre para dentro (dobradiças a leste)
PE-01	Padrão de entrada de energia (2 medidores)	2 caixas 0,34 x 0,60	indicativo: concessionária (Cemig) e projeto elétrico

AVISO: Projeto executivo de ARQUITETURA (somente arquitetura). Implantação, aterro e arrimos dependem do levantamento planialtimétrico; estrutura, contenção e instalações ficam com os projetos complementares (terceiros).

NOTAS E HIPÓTESES

1. Somente arquitetura. Metros com 2 casas; perfis em mm. Níveis em relação ao piso acabado do térreo (±0,00). Ver também EX-001 (planta), EX-007 a EX-009 (fachadas), EX-017 (piso da frente) e EX-020 (escada lateral).
2. Muros de divisa MU-01 com 1,80 acima do lado mais alto dos dois lados (padrão usual de 11/10/2026): o topo acompanha o terreno e a escada lateral; onde o muro retém terra, fica sobre o arrimo de pedra AR-01.
3. Frente: mureta MU-02 de pedra com 0,40 acima da calçada e gradil GR-01 até 1,80; pilares PI-01 de pedra com capa de concreto. Nada abre nem avança sobre o passeio: os pilares foram recuados para o alinhamento em 12/10/2026.
4. PO-01 basculante: gira na aresta de cima e deita para dentro do lote (alcance de 2,07); altura livre sob a folha aberta de 1,91. PO-02 de giro, abre para dentro.
5. Espessuras de muro, arrimo e fundações desta folha são as do modelo, indicativas.
6. PE-01: no modelo, as caixas avançam 0,08 sobre o passeio. A posição e a mureta do padrão saem do projeto elétrico (terceiros), com a face no alinhamento, sem avançar sobre o passeio.
7. Fundações da mureta, dos pilares e dos muros; arrimos AR-01 (até cerca de 5 m no fundo) e drenagem: projeto estrutural/geotécnico (terceiros). As espessuras desta folha são as do modelo, indicativas.
8. Automação do PO-01, fechadura elétrica do PO-02, interfone e campainha: projeto elétrico (terceiros).
9. Perfis do PO-01 (vão de 3,13): o serralheiro confirma os reforços e as ferragens do basculante.

REV.	DATA	DESCRIÇÃO	POR
R04	**08/10/2026**	**Emissão do executivo (Cleber): cotas 2 casas, cobertura EX-003, caixa 1 x 3.000 L e porta PC1**	**KMZERO**
R04	07/10/2026	Revisão 4 [redacted] lha clara, banheiros e pendentes da suíte	KMZERO
R03	07/10/2026	Revisão 3 (Cleber): entrada pela sala, cozinha nos fundos com a varanda	KMZERO
R02	06/10/2026	Revisão 2 (Cleber): varanda 1,50, subsolo gourmet aterrado, gourmet nos fundos, portas, interiores	KMZERO
R01	06/10/2026	Revisão 1 (Cleber): recuos 1,50, cozinha em U, piso +0,15, cobertura, subsolo gourmet	KMZERO
R00	29/09/2026	Emissão inicial — estudo preliminar	KMZERO

KMZERO | ENGENHARIA · ARQUITETURA

EMPREENDIMENTO	LOCAL	ETAPA
RESIDÊNCIA [redacted]	Rio Espera / MG	**PROJETO EXECUTIVO**

CONTEÚDO DA PRANCHA

MUROS, PORTÕES E FECHAMENTO DA FRENTE

DESENHO	RESPONSÁVEL TÉCNICO	REGISTRO PROFISSIONAL
KMZERO	Kleber Vieira Martins · Arquitetura	ART/RRT a emitir

REVISÃO	DATA	ESCALA	UNIDADE	CÓDIGO DA PRANCHA
R04	07/10/2026	1:25 / 1:10 / 1:100	metro (m)	**AP-ARQ-EX-021**

Direitos autorais reservados à KMZERO. Cliente: [redacted]