

CORTE AA — LONGITUDINAL

ESCALA 1:100 · frente (rua) → fundos
visada para oeste; plano a 2,70 m do eixo x da casa

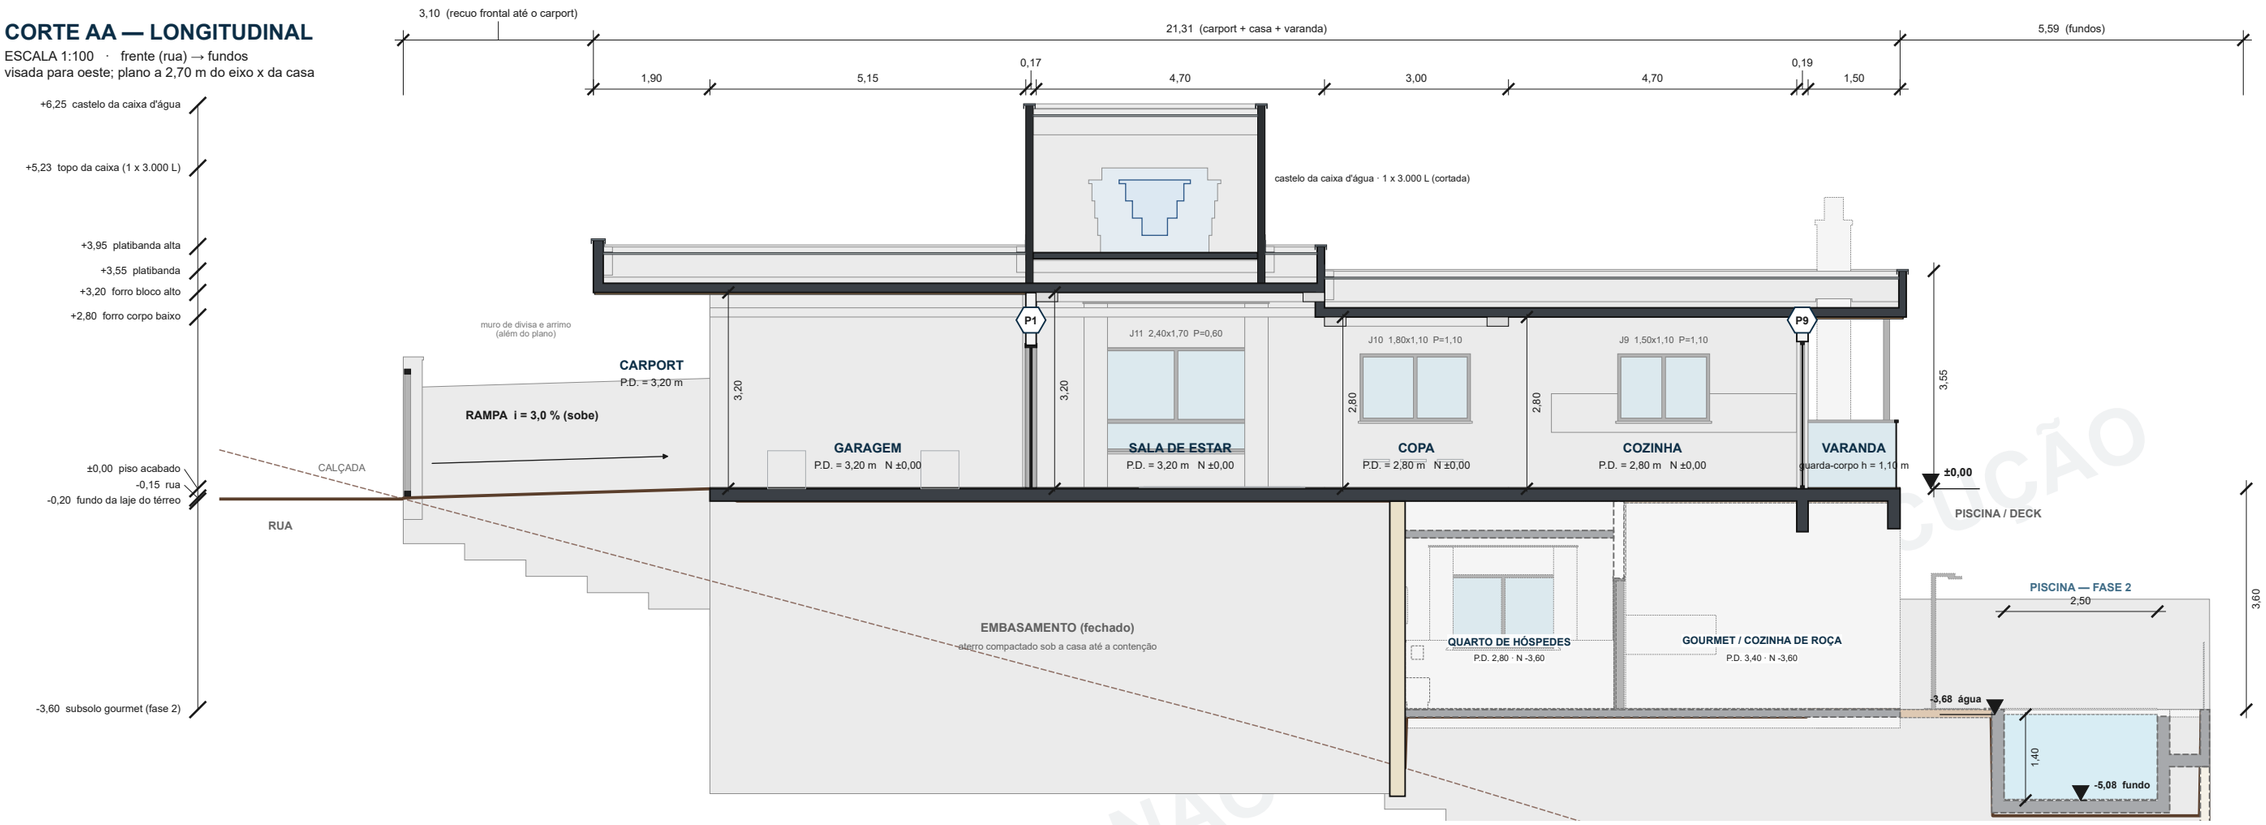

CORTE BB — TRANSVERSAL

ESCALA 1:50 · pela suíte (janela J2) e carport; visada para o norte; plano a 1,60 m da frente da casa

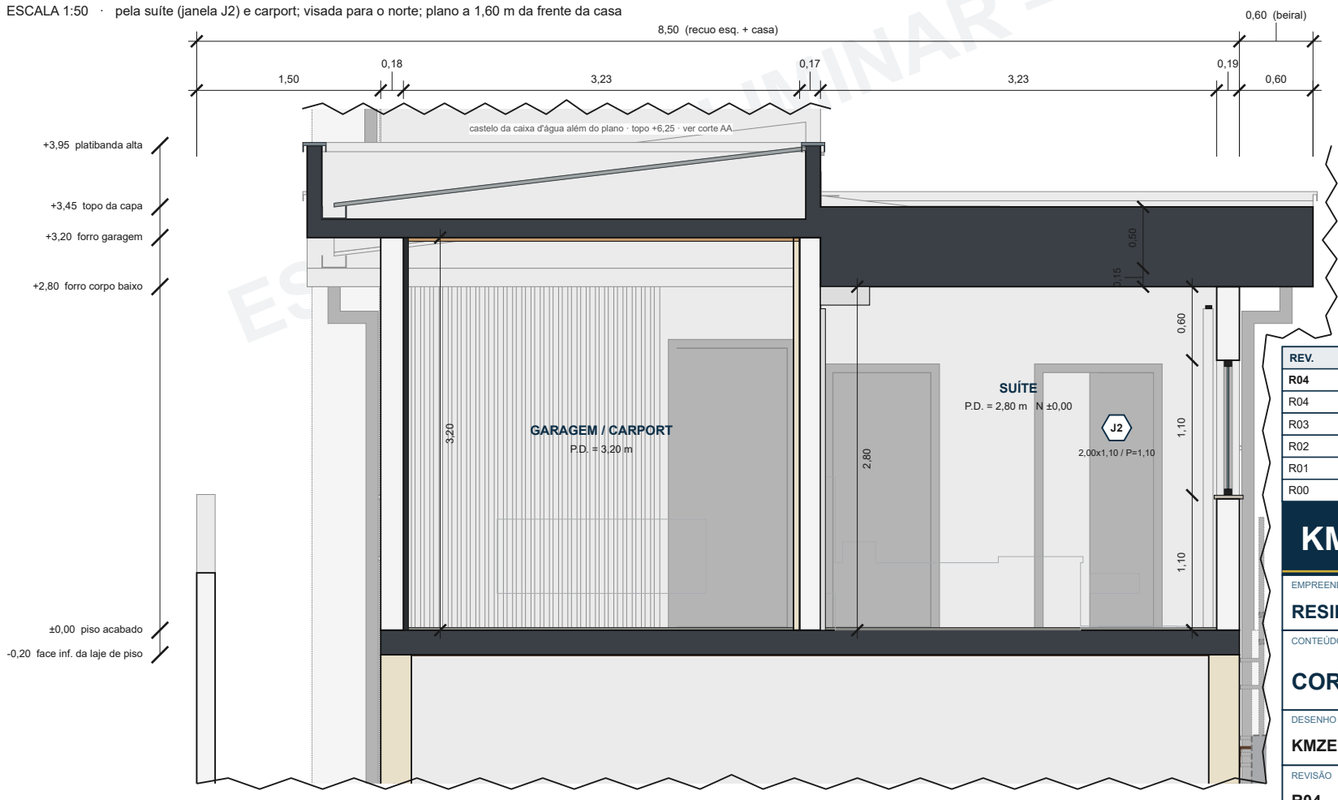

LEGENDA DOS CORTES

- Alvenaria cerâmica (P-02 externa · P-01 interna; espessuras nas cotas)
- Concreto armado (laje, capa, platibanda, pilar)
- Pedra mineira (embasamento, contenção, arrimos, chaminé)
- Forro / painel de madeira
- Esquadria (alumínio preto) e vidro
- Elementos além do plano de corte (cinza claro)
- FASE 2: traço tracejado e cor esmaecida
- Terreno natural (SRTM 30 m)
- Terreno acabado (regrade do projeto)
- Caixa d'água de polietileno (cortada)

NOTAS E HIPÓTESES

1. Cortes gerados por interseção dos sólidos do modelo com o plano; posição dos planos na planta PL-002.
2. Corte AA em 1:100 (o desenvolvimento de 30 m do lote não cabe em 1:75 no A3). Corte BB em 1:50, parcial: cortado abaixo do piso, logo depois do beiral leste e acima da platibanda alta (quebras; o castelo inteiro está no AA).
3. Corte AA passa pela garagem e pela sala de estar (bloco alto; o castelo e a caixa de 1 x 3.000 L, sobre a sala, aparecem cortados), copa, cozinha, varanda e, embaixo, pelo quarto de hóspedes e pela gourmet do subsolo (sobre aterro).
4. Terreno natural = SRTM 30 m (plano de 28,0 %). Contenção do subsolo gourmet a 6,57 m do fundo da casa; fundação e contenção por projeto específico.
5. Níveis relativos ao piso acabado (±0,00 = 754,15 m SRTM, 15 cm acima da rua). FASE 2 em traço tracejado.

REV.	DATA	DESCRIÇÃO	POR
R04	**08/10/2026**	**Emissão do executivo (Cleber): cotas 2 casas, cobertura EX-003, caixa 1 x 3.000 L e porta PC1**	**KMZERO**
R04	07/10/2026	Revisão 4 ([redacted]lha clara, banheiros e pendentes da suíte	KMZERO
R03	07/10/2026	Revisão 3 (Cleber): entrada pela sala, cozinha nos fundos com a varanda	KMZERO
R02	06/10/2026	Revisão 2 (Cleber): varanda 1,50, subsolo gourmet aterrado, gourmet nos fundos, portas, interiores	KMZERO
R01	06/10/2026	Revisão 1 (Cleber): recuos 1,50, cozinha em U, piso +0,15, cobertura, subsolo gourmet	KMZERO
R00	29/09/2026	Emissão inicial — estudo preliminar	KMZERO

KMZERO | ENGENHARIA · ARQUITETURA

EMPREENDIMENTO	LOCAL	ETAPA
RESIDÊNCIA[redacted]	Rio Espera / MG	**ESTUDO PRELIMINAR**

CONTEÚDO DA PRANCHA

CORTES AA E BB

DESENHO	RESPONSÁVEL TÉCNICO	REGISTRO PROFISSIONAL
KMZERO	Kleber Vieira Martins · Arquitetura	sem ART/RRT — estudo preliminar

REVISÃO	DATA	ESCALA	UNIDADE	CÓDIGO DA PRANCHA
R04	07/10/2026	AA 1:100 · BB 1:50	metro (m)	**AP-ARQ-PL-004**

Direitos autorais reservados à KMZERO. Cliente: [redacted]

AVISO: Estudo preliminar: topografia SRTM (30 m) e lote do compromisso de C/V, sem levantamento; não serve para fundação, contenção, terraplenagem ou aprovação legal.