
FACHADA FRENTE (SUL)

ESCALA 1:75 · vista da rua; muro, gradil e portões incluídos



FACHADA FUNDOS (NORTE)

ESCALA 1:100 · vista da cidade; subsolo gourmet, deck e piscina em FASE 2

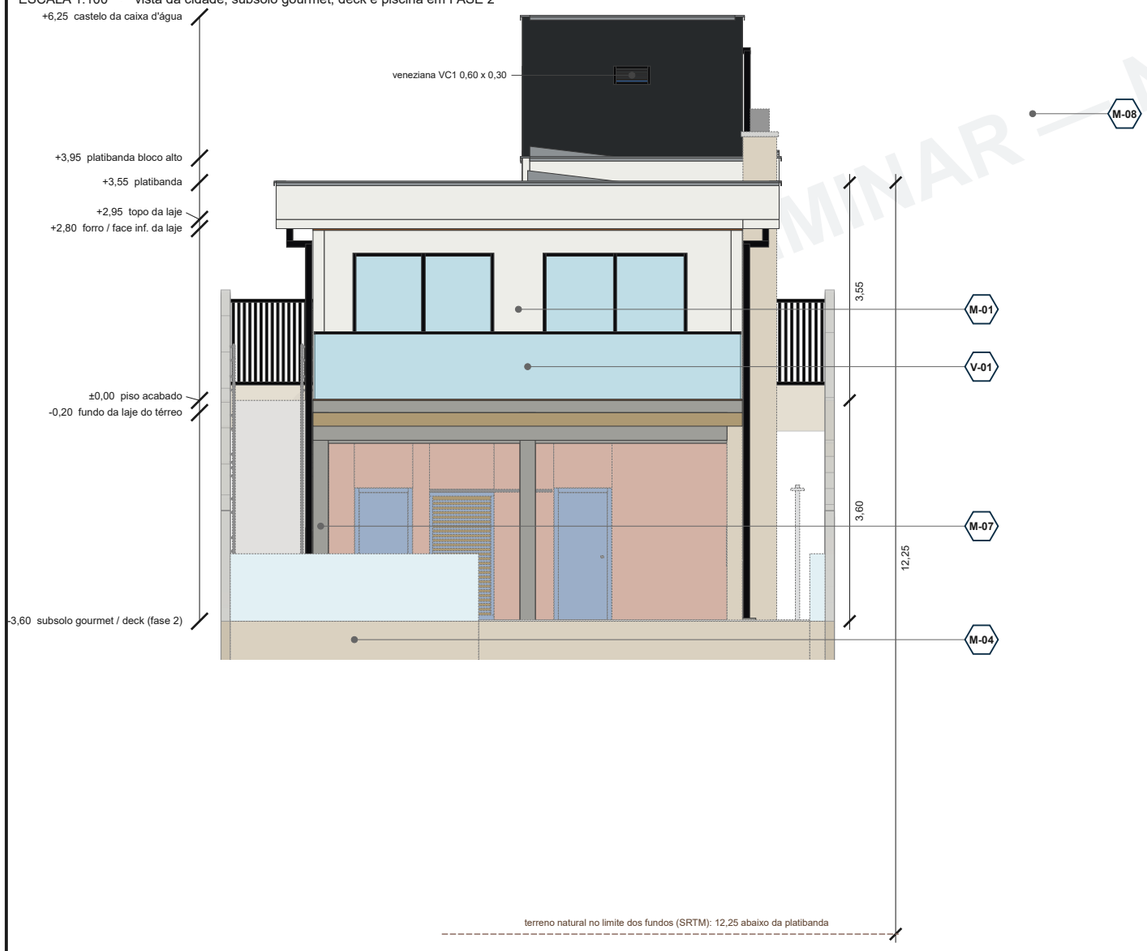

LEGENDA DE MATERIAIS

M-01	Textura acrílica branca sobre emboço
M-02	Pintura acrílica grafite (moldura, frisos, forro da capa)
M-04	Pedra natural mineira (embasamento, contenção, pilares do portão, chaminé)
M-05	Painel ripado de madeira (garagem e forro do carport/varanda)
M-06	Cobogó — elemento vazado 20 x 20 x 9 cm
M-07	Concreto aparente / laje (pilares, arrimos e piscina)
M-08	Reboco cinza claro (muros de divisa, h = 1,80 m)
V-01	Vidro incolor/laminado (esquadrias e guarda-corpo)
A-01	Alumínio preto (caixilhos, gradil, portões, corrimão)
D-01	Deck de madeira (varanda e área da piscina)
	FASE 2 (subsolo gourmet, deck, piscina): cor esmaecida, traço tracejado

NOTAS E HIPÓTESES

1. Fachadas geradas por projeção ortogonal dos sólidos do modelo (cores planas do JSON de materiais).
2. Frente: muro baixo de pedra com gradil de lâminas verticais vazadas e portões (basculante de veículos e social de giro) em alumínio preto brilhante.
3. Desnível: bloco alto (garagem + sala de estar, pé-direito 3,20) com o castelo da caixa d'água acima (1 x 3.000 L; veneziana VC1 nos fundos, porta PC1 de metal vazado na face leste); corpo baixo com telhado embutido e beiral de 0,60 m.
4. Fundos: subsolo gourmet (FASE 2, sobre aterro) com gourmet aberta na largura toda sob a casa e a varanda, paredes externas em pedra; chaminé de pedra à direita (oeste), ao lado da varanda.
5. Fachada da frente: janela J1 ampliada (1,90 x 2,40) emoldurada em grafite; cobogó ao lado; painel ripado ao fundo da garagem.
6. M-06 = cobogó, conforme pedido para esta prancha (no Padrão KMZERO M-06 é ACM/painel metálico: ajustar a legenda do Padrão).

AVISO: Estudo preliminar: topografia SRTM (30 m) e lote do compromisso de C/V, sem levantamento; não serve para fundação, contenção, terraplenagem ou aprovação legal.

REV.	DATA	DESCRIÇÃO	POR
R04	**08/10/2026**	**Emissão do executivo (Cleber): cotas 2 casas, cobertura EX-003, caixa 1 x 3.000 L e porta PC1**	**KMZERO**
R04	07/10/2026	Revisão 4 [redacted]lha clara, banheiros e pendentes da suíte	KMZERO
R03	07/10/2026	Revisão 3 (Cleber): entrada pela sala, cozinha nos fundos com a varanda	KMZERO
R02	06/10/2026	Revisão 2 (Cleber): varanda 1,50, subsolo gourmet aterrado, gourmet nos fundos, portas, interiores	KMZERO
R01	06/10/2026	Revisão 1 (Cleber): recuos 1,50, cozinha em U, piso +0,15, cobertura, subsolo gourmet	KMZERO
R00	29/09/2026	Emissão inicial — estudo preliminar	KMZERO

KMZERO | ENGENHARIA · ARQUITETURA

EMPREENDIMENTO: **RESIDÊNCIA [redacted]**	LOCAL: Rio Espera / MG	ETAPA: **ESTUDO PRELIMINAR**

CONTEÚDO DA PRANCHA: **FACHADAS FRENTE E FUNDOS**

DESENHO: **KMZERO**	RESPONSÁVEL TÉCNICO: Kleber Vieira Martins · Arquitetura	REGISTRO PROFISSIONAL: sem ART/RRT — estudo preliminar

REVISÃO	DATA	ESCALA	UNIDADE	CÓDIGO DA PRANCHA
R04	07/10/2026	1:75 e 1:100	metro (m)	**AP-ARQ-PL-005**

Direitos autorais reservados à KMZERO. Cliente: [redacted]

NÃO USAR PARA EXECUÇÃO