

FACHADA LESTE (lado direito)

ESCALA 1:150 · observador a leste; frente à esquerda; muros de divisa e arrimos translúcidos

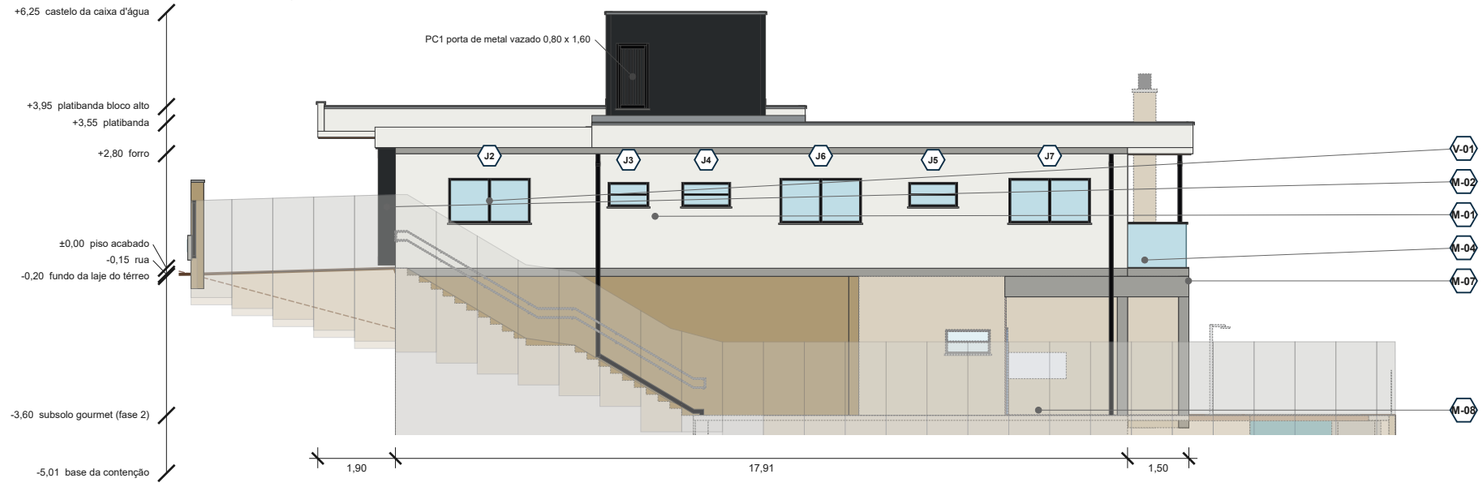

FACHADA OESTE (lado esquerdo)

ESCALA 1:150 · observador a oeste; fundos à esquerda; recuo de 1,50 m com janelas baixas e peitoril de granito

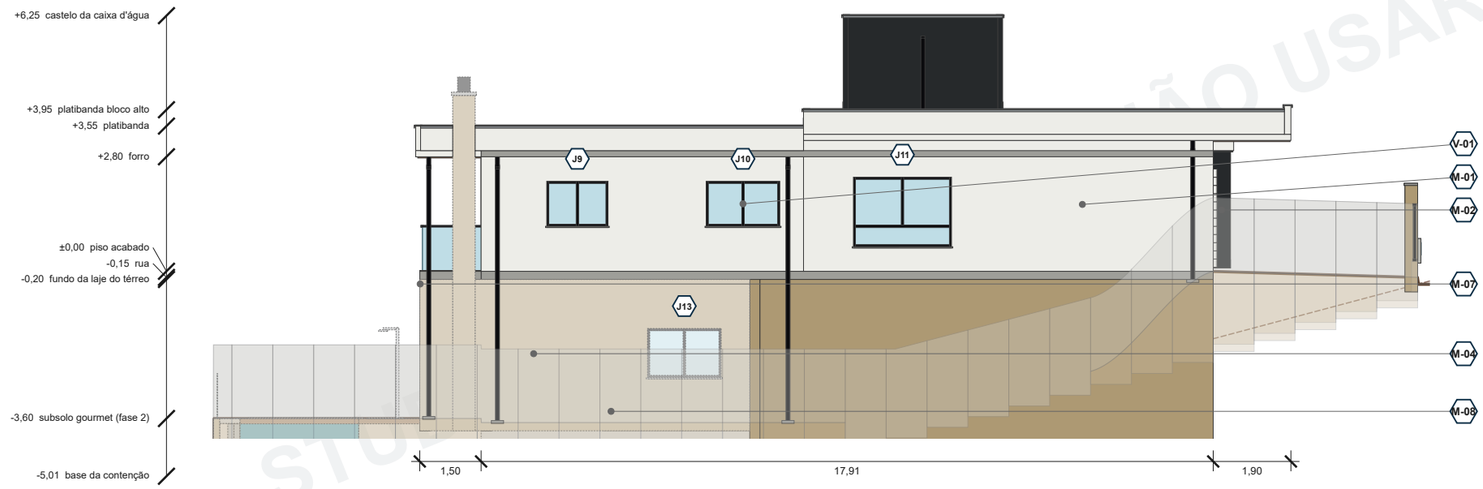

QUADRO DE ESQUADRIAS (Q02/Q03)

Cód.	Descrição	L (m)	H (m)	Peit. (m)	Tipologia · material	Qtd.
P1	Porta de entrada (correr embutida, para a sala)	0,90	2,30	0,00	correr embutida (kit na parede) · madeira maciça (freijó/imbuia, a definir)	1
P2	Porta sala/hall da suíte (correr aparente)	0,80	2,10	0,00	correr aparente · madeira maciça · trilho preto aparente	1
P3	Porta suíte (hall)	0,80	2,10	0,00	giro 1 folha · madeira semi-oca ou maciça (a definir)	1
P4	Passagem suíte/closet	0,90	2,10	0,00	passagem livre (sem folha) · vão com guarnição de madeira	1
P5	Porta banho da suíte (correr embutida)	0,80	2,10	0,00	correr embutida (kit na parede) · madeira maciça (freijó/imbuia, a definir)	1
P6	Porta banheiro social	0,80	2,10	0,00	giro 1 folha · madeira semi-oca ou maciça (a definir)	1
P7	Porta quarto 2	0,80	2,10	0,00	giro 1 folha · madeira semi-oca ou maciça (a definir)	1
P8	Porta quarto 3	0,80	2,10	0,00	giro 1 folha · madeira semi-oca ou maciça (a definir)	1
P9	Porta de correr de vidro (cozinha/varanda)	2,35	2,40	0,00	correr, folhas de vidro · vidro temperado incolor 8 mm + alumínio preto	1
J1	Janela alta da suíte (fachada)	1,90	2,40	0,30	fixa (+ bandeira) · alumínio preto + vidro laminado 8 mm	1
J2	Janela suíte	2,00	1,10	1,10	correr 2 folhas · alumínio preto + vidro incolor 6 mm · peitoril de granito	1
J3	Janela closet	1,00	0,60	1,50	basculante · alumínio preto + vidro mini-boreal 4 mm · peitoril de granito	1
J4	Janela banho suíte	1,20	0,60	1,50	maxim-ar · alumínio preto + vidro mini-boreal 4 mm · peitoril de granito	1
J5	Janela banheiro social	1,20	0,60	1,50	maxim-ar · alumínio preto + vidro mini-boreal 4 mm · peitoril de granito	1
J6	Janela quarto 2	2,00	1,10	1,10	correr 2 folhas · alumínio preto + vidro incolor 6 mm · peitoril de granito	1
J7	Janela quarto 3 (leste)	2,00	1,10	1,10	correr 2 folhas · alumínio preto + vidro incolor 6 mm · peitoril de granito	1
J8	Janela quarto 3 (vista)	2,30	1,80	0,60	correr 2 folhas · alumínio preto + vidro laminado 8 mm · peitoril de granito	1
J9	Janela cozinha (sobre a pia)	1,50	1,10	1,10	correr 2 folhas · alumínio preto + vidro incolor 6 mm · peitoril de granito	1
J10	Janela copa	1,80	1,10	1,10	correr 2 folhas · alumínio preto + vidro incolor 6 mm · peitoril de granito	1
J11	Janela sala	2,40	1,70	0,60	correr 2 folhas + fixo inferior · alumínio preto + vidro laminado 8 mm · peitoril de granitot	
PC1 **	Porta de acesso à caixa d'água	0,80	1,60	0,05 (cast.)	giro, abre para fora · metal vazado (alumínio preto + tela inox)	1
VC1 **	Veneziana de ventilação do castelo	0,60	0,30	1,30 (cast.)	veneziana fixa · alumínio preto	1
P10 *	Porta lavanderia (correr veneziana)	0,95	2,10	0,00 (inf.)	correr veneziana · madeira azul colonial · trilho preto	1
P11 *	Porta banheiro (inferior)	0,80	2,10	0,00 (inf.)	giro 1 folha · madeira pintada azul colonial (gourmet de roça)	1
P12 *	Porta quarto de hóspedes	0,80	2,10	0,00 (inf.)	giro 1 folha · madeira pintada azul colonial (gourmet de roça)	1
J12 *	Janela banheiro (inferior)	1,10	0,60	1,50 (inf.)	maxim-ar · alumínio preto + vidro mini-boreal 4 mm · peitoril de granito	1
J13 *	Janela quarto de hóspedes	1,80	1,20	1,00 (inf.)	correr 2 folhas · alumínio preto + vidro incolor 6 mm · peitoril de granito	1

Fase 1: 10 portas + 12 janelas = 22 vãos (com as 2 do castelo). * subsolo gourmet (fase 2), peitoril medido do piso do subsolo (-3,60).

** castelo da caixa d'água (1 x 3.000 L): peitoril medido do piso do castelo (+3,85); PC1 abre para fora (leste), dobradiças no batente norte; detalhes no AP-ARQ-EX-003.

Portas: altura livre do vão; peitoril = distância do piso acabado (±0,00) à soleira da esquadria.

LEGENDA DE MATERIAIS

- M-01 — Textura acrílica branca sobre emboço
- M-02 — Pintura acrílica grafite (moldura, frisos, forro da capa)
- M-04 — Pedra natural mineira (embasamento, contenção, pilares do portão, chaminé)
- M-05 — Painel ripado de madeira (garagem e forro do carport/varanda)
- M-06 — Cobogó — elemento vazado 20 x 20 x 9 cm
- M-07 — Concreto aparente / laje (pilares, arrimos e piscina)
- M-08 — Reboco cinza claro (muros de divisa, h = 1,80 m)
- V-01 — Vidro incolor/laminado (esquadrias e guarda-corpo)
- A-01 — Alumínio preto (caixilhos, gradil, portões, corrimão)
- D-01 — Deck de madeira (varanda e área da piscina)
- FASE 2 (subsolo gourmet, deck, piscina): cor esmaecida, traço tracejado

DECISÕES DA R04 [redacted]

[redacted]1. Pedido da [redacted] (foto de referência): ilha em cor clara. Tampo e laterais em cascata até o piso em porcelanato branco com veios cinza (efeito mármore), frentes no mesmo material; cooktop e coifa de ilha mantidos. A bancada da pia segue em granito cinza.

2. Pedido da [redacted] tom claro com acessórios dourados. Paredes em porcelanato branco com veios dourados até o teto, faixa de ripado de madeira entre a bancada e o box, nicho de madeira, deck de madeira no piso do box, piso marmorizado claro; torneira, chuveiro, perfil do box, papeleira, toalheiro e moldura do espelho dourados.

3. Ideia da KMZERO (a [redacted] ainda não tinha ideia): banho "spa natural". Box em porcelanato travertino até o teto com nicho iluminado, piso em travertino 60 x 120, parede da bancada em verde-musgo, gabinete de madeira com tampo de travertino, espelho redondo com LED por trás e metais em dourado escovado.

4. Pedido da [redacted] (foto de referência): pendentes de cabeceira com aro oval de cristal iluminado, haste e canopla douradas e cabo fino até o teto.

5. Pedido do Cleber: calha, rufo e descida à mostra e outra cobertura para a caixa d'água. Estudada a telha colonial a 35 %, ficou o fibrocimento, agora a 12 %, ainda escondido pela platibanda de 60 cm. Calhas em U de chapa galvanizada, rufo de capa com pingadeira, rufo de encosto no bloco alto, condutores ø100 em alumínio preto aparentes nas laterais com caixa de areia; castelo da caixa d'água sem o telhadinho, com platibanda, rufo, telhado escondido, calha e descida.

6. Escopo da KMZERO neste projeto: somente arquitetura. Estrutural, contenção, fundações, hidrossanitário e pluvial, elétrico, levantamento e sondagem ficam com terceiros; as posições de calhas, descidas, pilares e arrimos do modelo são indicativas.

7. Emissão do executivo (Cleber), 08/10/2026: cotas com 2 casas, fechando o total nas cadeias; cobertura executiva no AP-ARQ-EX-003 (condutores CP-01 a CP-07); caixa d'água 1 x 3.000 L no castelo de 3,59 × 3,90 m (topo +6,25), porta PC1 0,80 × 1,60 de metal vazado na face leste e veneziana VC1 0,60 × 0,30 ao norte.

AVISO: Estudo preliminar: topografia SRTM (30 m) e lote do compromisso de C/V, sem levantamento; não serve para fundação, contenção, terraplenagem ou aprovação legal.

PENDÊNCIAS PARA A ETAPA SEGUINTE

1. Documento da compra do irmão (o compromisso está no nome do Tiago): recibo, contrato ou cessão
2. Escritura e matrícula individual (só após a conclusão do loteamento)
3. Croqui do loteamento (anexo do compromisso) e pin correto do lote 03, quadra 03
4. Pavimento e redes da Rua 02 no local (contrato prevê bloquete)
5. Código de Obras de Rio Espera: recuos, taxa de ocupação, permeabilidade, altura de muro
6. Cliente escolher porcelanato/acabamentos (loja Tau, em Rio Espera, citada por ela)
7. Validar com a cliente a R04: ilha clara, banheiros, pendentes da suíte e cobertura com calhas e descidas aparentes (entrada pela sala, varanda de 1,50 m e subsolo gourmet aterrado já vistos nas revisões anteriores)
8. Validar o castelo maior da caixa de 3.000 L (3,59 × 3,90 m, topo +6,25, 0,50 m mais alto): ele aparece mais nas vistas da frente
9. Acesso ao telhado até a porta do castelo: escada móvel até a capa da suíte e passarela de tábuas sobre as terças (indicativo; definir com a cliente)
10. Fora do escopo (somente arquitetura): levantamento planialtimétrico, sondagem e projetos complementares — estrutural e contenção, fundações, hidrossanitário e pluvial, elétrico — por terceiros, a partir deste anteprojeto

HIPÓTESES DESTAS PRANCHAS

1. Sentido de abertura das portas de giro indicativo; mobiliário e automóvel ilustrativos (a cliente define o layout).
2. Térreo em ±0,00 (0,15 acima da rua); bloco alto (garagem + sala de estar) com pé-direito 3,20; subsolo gourmet a -3,60 (fase 2).
3. Cotas em metro com 2 casas (Padrão KMZERO); nas cadeias a soma fecha o total (posição acumulada arredondada): a parede externa P-02 sai 0,18 ou 0,19.
4. Cobertura: telhado embutido de fibrocimento (i = 12 %), platibanda de 0,60 m com rufo, calhas em U e condutores ø100 aparentes nas laterais — dimensionar no projeto pluvial.
5. Castelo da caixa d'água: 1 x 3.000 L, porta PC1 de metal vazado (leste), veneziana VC1 (norte); carga cheia indicativa ~3.120 kgf para o projeto estrutural (terceiros).
6. Recuos laterais de 1,50 m: janelas baixas permitidas nas duas laterais (Código Civil art. 1.301); conferir o Código de Obras.
7. Escalas: PL-003 cobertura 1:75, subsolo gourmet 1:100; PL-004 AA 1:100, BB 1:50; PL-005 frente 1:75, fundos 1:100; PL-006 1:150.

REV.	DATA	DESCRIÇÃO	POR
R04	**08/10/2026**	**Emissão do executivo (Cleber): cotas 2 casas, cobertura EX-003, caixa 1 x 3.000 L e porta PC1**	**KMZERO**
R04	07/10/2026	Revisão 4 ([redacted] ilha clara, banheiros e pendentes da suíte	KMZERO
R03	07/10/2026	Revisão 3 (Cleber): entrada pela sala, cozinha nos fundos com a varanda	KMZERO
R02	06/10/2026	Revisão 2 (Cleber): varanda 1,50, subsolo gourmet aterrado, gourmet nos fundos, portas, interiores	KMZERO
R01	06/10/2026	Revisão 1 (Cleber): recuos 1,50, cozinha em U, piso +0,15, cobertura, subsolo gourmet	KMZERO
R00	29/09/2026	Emissão inicial — estudo preliminar	KMZERO

KMZERO | ENGENHARIA · ARQUITETURA

EMPREENDIMENTO	LOCAL	ETAPA
RESIDÊNCIA [redacted]	Rio Espera / MG	**ESTUDO PRELIMINAR**

CONTEÚDO DA PRANCHA

FACHADAS LATERAIS · ESQUADRIAS · NOTAS

DESENHO	RESPONSÁVEL TÉCNICO	REGISTRO PROFISSIONAL
KMZERO	Kleber Vieira Martins · Arquitetura	sem ART/RRT — estudo preliminar

REVISÃO	DATA	ESCALA	UNIDADE	CÓDIGO DA PRANCHA
R04	07/10/2026	1:150 (fachadas)	metro (m)	**AP-ARQ-PL-006**

Direitos autorais reservados à KMZERO. Cliente: [redacted]