

PLANTA BAIXA — TÉRREO

ESCALA 1:50 · cortada a 1,20 m do piso acabado · cotas em metros · níveis em metros (±0,00 = piso acabado do térreo)

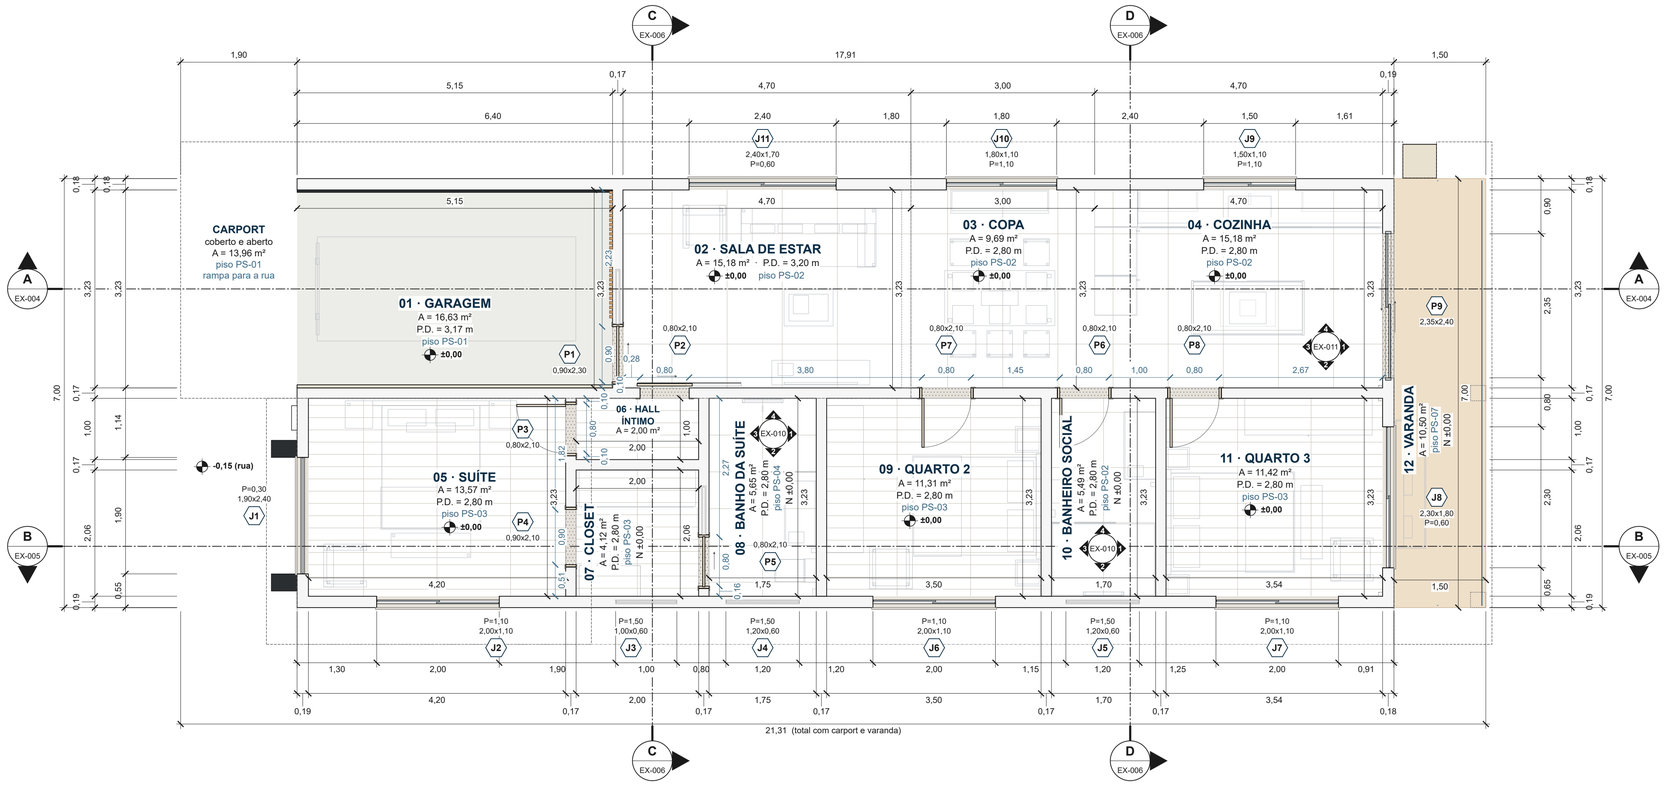

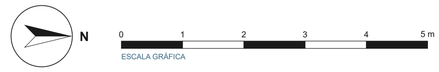

LEGENDA

- Alvenaria cortada (plano a 1,20 m)
- Pedra (embasamento, chaminé, arrimo)
- Concreto (pilar/contenção — referência, ver estrutural)
- Soleira de granito
- Batente, alizar e folha de madeira (portas)
- Esquadria de alumínio e vidro; peitoril com pingadeira
- Projeção acima do corte (laje, viga, aéreo)
- Beiral (projeção da laje de cobertura)
- Mobiliário e equipamentos (indicativo)
- Paginação do piso (juntas)
- P1 — Porta: L x H (vão livre)
- J1 — Janela: L x H e P = peitoril
- ±0,00 — Nível de piso acabado (±0,00 = 754,15 m SRTM)
- Cota de amarração de porta (canto → batente)
- EX-0nn — Vista interna das áreas molhadas (1:25) seta para a parede vista, com o nº da vista; no círculo, a folha de destino (EX-010 e EX-011)

QUADRO DE ESQUADRIAS DO TÉRREO (Q02)

Cód.	L (m)	H (m)	Peit. (m)	Tipologia	Material	Ambientes	Qtd.	Detalhe
P1	0,90	2,30	0,00	correr embutida (kit na parede)	madeira maciça (a definir)	Garagem / Sala de estar	1	EX-014
P2	0,80	2,10	0,00	correr aparente	madeira maciça · trilho preto aparente	Sala de estar / Hall íntimo	1	EX-014
P3	0,80	2,10	0,00	giro 1 folha	madeira semi-oca ou maciça (a definir)	Suíte / Hall íntimo	1	EX-014
P4	0,90	2,10	0,00	passagem livre (sem folha)	vão com guarnição de madeira	Suíte / Closet	1	EX-014
P5	0,80	2,10	0,00	correr embutida (kit na parede)	madeira maciça (a definir)	Closet / Banho da suíte	1	EX-014
P6	0,80	2,10	0,00	giro 1 folha	madeira semi-oca ou maciça (a definir)	Copa / Banheiro social	1	EX-014
P7	0,80	2,10	0,00	giro 1 folha	madeira semi-oca ou maciça (a definir)	Copa / Quarto 2	1	EX-014
P8	0,80	2,10	0,00	giro 1 folha	madeira semi-oca ou maciça (a definir)	Cozinha / Quarto 3	1	EX-014
P9	2,35	2,40	0,00	correr, folhas de vidro	vidro temperado incolor 8 mm + alumínio preto	Cozinha / Varanda	1	EX-014
J1	1,90	2,40	0,30	fixa (+ bandeira)	alumínio preto + vidro laminado 8 mm	Suíte	1	EX-015
J2	2,00	1,10	1,10	correr 2 folhas	alumínio preto + vidro incolor 6 mm	Suíte	1	EX-015
J3	1,00	0,60	1,50	basculante	alumínio preto + vidro mini-boreal 4 mm	Closet	1	EX-015
J4	1,20	0,60	1,50	maxim-ar	alumínio preto + vidro mini-boreal 4 mm	Banho da suíte	1	EX-015
J5	1,20	0,60	1,50	maxim-ar	alumínio preto + vidro mini-boreal 4 mm	Banheiro social	1	EX-015
J6	2,00	1,10	1,10	correr 2 folhas	alumínio preto + vidro incolor 6 mm	Quarto 2	1	EX-015
J7	2,00	1,10	1,10	correr 2 folhas	alumínio preto + vidro incolor 6 mm	Quarto 3	1	EX-015
J8	2,30	1,80	0,60	correr 2 folhas	alumínio preto + vidro laminado 8 mm	Quarto 3	1	EX-015
J9	1,50	1,10	1,10	correr 2 folhas	alumínio preto + vidro incolor 6 mm	Cozinha	1	EX-015
J10	1,80	1,10	1,10	correr 2 folhas	alumínio preto + vidro incolor 6 mm	Copa	1	EX-015
J11	2,40	1,70	0,60	correr 2 folhas + fixo inferior	alumínio preto + vidro laminado 8 mm	Sala de estar	1	EX-015

QUADRO DE AMBIENTES (Q01)

Nº	Ambiente	Área (m²)	Perím. (m)	P.D. (m)	Piso	Nível
01	Garagem	16,63	16,76	3,17	PS-01 Concreto desempenado, juntas 2,00 x 2,00	±0,00
02	Sala de estar	15,18	15,86	3,20	PS-02 Porcel. marmorizado 90 x 90 polido	±0,00
03	Copa	9,69	12,46	2,80	PS-02 Porcel. marmorizado 90 x 90 polido	±0,00
04	Cozinha	15,18	15,86	2,80	PS-02 Porcel. marmorizado 90 x 90 polido	±0,00
05	Suíte	13,57	14,86	2,80	PS-03 Porcel. amadeirado 20 x 120	±0,00
06	Hall íntimo	2,00	6,00	2,80	PS-03 Porcel. amadeirado 20 x 120	±0,00
07	Closet	4,12	8,12	2,80	PS-03 Porcel. amadeirado 20 x 120	±0,00
08	Banho da suíte	5,65	9,96	2,80	PS-04 Porcel. travertino 60 x 120 acetinado	±0,00
09	Quarto 2	11,31	13,46	2,80	PS-03 Porcel. amadeirado 20 x 120	±0,00
10	Banheiro social	5,49	9,86	2,80	PS-02 Porcel. marmorizado 90 x 90 polido	±0,00
11	Quarto 3	11,42	13,53	2,80	PS-03 Porcel. amadeirado 20 x 120	±0,00
12	Varanda (coberta)	10,50	17,00	2,77	PS-07 Deck de madeira (varanda e área da piscina)	±0,00
	ÁREA ÚTIL DOS AMBIENTES	110,24				

QUADRO DE ACABAMENTOS DO TÉRREO (Q03)

Ambiente	Piso	Paredes	Teto
Garagem	PS-01 Concreto desempenado, juntas 2,00 x 2,00	reboco + massa + pintura acrílica branca	forro de madeira
Sala de estar	PS-02 Porcel. marmorizado 90 x 90 polido	reboco + massa + pintura branca; painel ripado de madeira (TV)	sanca de gesso com LED
Copa	PS-02 Porcel. marmorizado 90 x 90 polido	reboco + massa + pintura acrílica branca	sanca de gesso com LED
Cozinha	PS-02 Porcel. marmorizado 90 x 90 polido	reboco + massa + pintura branca; metrô verde atrás da bancada; parede do meio em terracota + prateleiras	laje com gesso liso + pintura branca
Suíte	PS-03 Porcel. amadeirado 20 x 120	reboco + massa + pintura branca; ripado de madeira na cabeceira	laje com gesso liso + pintura branca; sanca de gesso com LED na cabeceira
Hall íntimo	PS-03 Porcel. amadeirado 20 x 120	reboco + massa + pintura acrílica branca	laje com gesso liso + pintura branca
Closet	PS-03 Porcel. amadeirado 20 x 120	reboco + massa + pintura acrílica branca	laje com gesso liso + pintura branca
Banho da suíte	PS-04 Porcel. travertino 60 x 120 acetinado	reboco + massa + pintura branca; box em porcelanato travertino até o teto; parede da bancada em verde-musgo	laje com gesso liso + pintura branca
Quarto 2	PS-03 Porcel. amadeirado 20 x 120	reboco + massa + pintura branca; parede da cabeceira em sálvia	laje com gesso liso + pintura branca
Banheiro social	PS-02 Porcel. marmorizado 90 x 90 polido	reboco + massa + pintura branca; porcelanato com veio dourado até o teto; faixa ripada de madeira	laje com gesso liso + pintura branca
Quarto 3	PS-03 Porcel. amadeirado 20 x 120	reboco + massa + pintura branca; parede da cabeceira em terracota	laje com gesso liso + pintura branca
Varanda	PS-07 Deck de madeira (varanda e área da piscina)	reboco + pintura; guarda-corpo de vidro	forro de madeira

QUADRO DE ÁREAS (Q05)

Descrição	Área (m²)	% lote
Terreno (lote 03, quadra 03: 10,00 x 30,00 m)	300,00	100,00
Área útil dos ambientes do térreo	110,24	36,75
Paredes	15,10	5,03
Casa: paredes externas (7,00 x 17,91)	125,34	41,78
Carport (fora da casa)	13,96	4,65
Varanda coberta	10,50	3,50
ÁREA CONSTRUÍDA COBERTA (térreo)	149,80	49,93
Projeção da cobertura (com beirais)	169,58	56,53
Taxa de ocupação (projeção / lote)	56,53 %	

NOTAS E HIPÓTESES

1. Cotas em metros com 2 casas, de face acabada a face acabada (paredes externas de 185 mm e internas de 170 mm, com reboco). As cadeias fecham o total: a parede de 185 mm aparece como 0,18 ou 0,19, conforme o arredondamento acumulado. Conferir todas as medidas na obra antes de executar esquadrias, bancadas e revestimentos.
2. Níveis em metros relativos ao piso acabado do térreo (±0,00 = 754,15 m SRTM, 0,15 m acima da rua). P.D. medido do piso acabado à face inferior do forro de madeira ou da laje (mesmo critério dos cortes EX-004 a EX-006).
3. Esquadrias: portas L x H = vão livre de passagem; janelas L x H = vão acabado; P = peitoril (granito; na J1, a base da moldura grafite com caimento e pingadeira, padrão usual de 11/10/2026), do piso acabado interno ao topo do peitoril. Ver quadro Q02; folhas, ferragens e cores a confirmar com a cliente.
4. Amarração das portas internas (cotas em azul): do canto da parede ao batente, no lado oposto ao giro da folha.
5. Mobiliário e equipamentos em cinza são indicativos (layout); bancadas, louças e metais conforme vistas e memorial.
6. Somente arquitetura: pilares, vigas e lajes aparecem como referência; dimensões finais no projeto estrutural. Instalações elétricas e hidrossanitárias por projetos complementares (terceiros).
7. Cortes AA, BB, CC e DD: ver EX-004 a EX-006. Revestimentos: ver quadro Q03. Guarda-corpos com 1,10 m acima do piso acabado (NBR 14718).
8. Vistas internas das áreas molhadas: ver EX-010 e EX-011 (1:25; banho da suíte e banheiro social na EX-010, cozinha na EX-011).
9. Detalhamento das esquadrias: ver EX-014 a EX-016 (portas P1 a P9 na EX-014 e janelas J1 a J11 na EX-015, em 1:25; quadro geral e detalhes típicos em 1:5 e 1:10 na EX-016). Folha de cada esquadria: coluna Detalhe do Q02.
10. Paginação de piso: ver EX-017 (térreo) e EX-018 (subsolo gourmet); planta de forro: ver EX-019.

AVISO: Projeto executivo de ARQUITETURA (somente arquitetura). Implantação, aterro e arrimos dependem do levantamento planialtimétrico; estrutura, contenção e instalações ficam com os projetos complementares (terceiros).

REV.	DATA	DESCRIÇÃO	POR
R04	**08/10/2026**	**Emissão do executivo (Cleber): cotas 2 casas, cobertura EX-003, caixa 1 x 3.000 L e porta PC1**	**KMZERO**
R04	07/10/2026	Revisão 4 (Ana Paula): ilha clara, banheiros e pendentes da suíte	KMZERO
R03	07/10/2026	Revisão 3 (Cleber): entrada pela sala, cozinha nos fundos com a varanda	KMZERO
R02	06/10/2026	Revisão 2 (Cleber): varanda 1,50, subsolo gourmet aterrado, gourmet nos fundos, portas, interiores	KMZERO
R01	06/10/2026	Revisão 1 (Cleber): recuos 1,50, cozinha em U, piso +0,15, cobertura, subsolo gourmet	KMZERO
R00	29/09/2026	Emissão inicial — estudo preliminar	KMZERO

KMZERO | ENGENHARIA · ARQUITETURA

EMPREENDIMENTO	LOCAL	ETAPA
RESIDÊNCIA ANA PAULA	Rio Espera / MG	PROJETO EXECUTIVO

CONTEÚDO DA PRANCHA

PLANTA BAIXA DO TÉRREO

DESENHO	RESPONSÁVEL TÉCNICO	REGISTRO PROFISSIONAL
KMZERO	Kleber Vieira Martins · Arquitetura	ART/RRT a emitir

REVISÃO	DATA	ESCALA	UNIDADE	CÓDIGO DA PRANCHA
R04	07/10/2026	1:50	metro (m)	AP-ARQ-EX-001

Direitos autorais reservados à KMZERO. Cliente: Ana Paula.