
CORTE AA — LONGITUDINAL

ESCALA 1:50 · longitudinal pela garagem, sala, castelo da caixa d'água, copa, cozinha, varanda, subsolo gourmet e piscina · plano x = 1,80 m da casa, visada para oeste

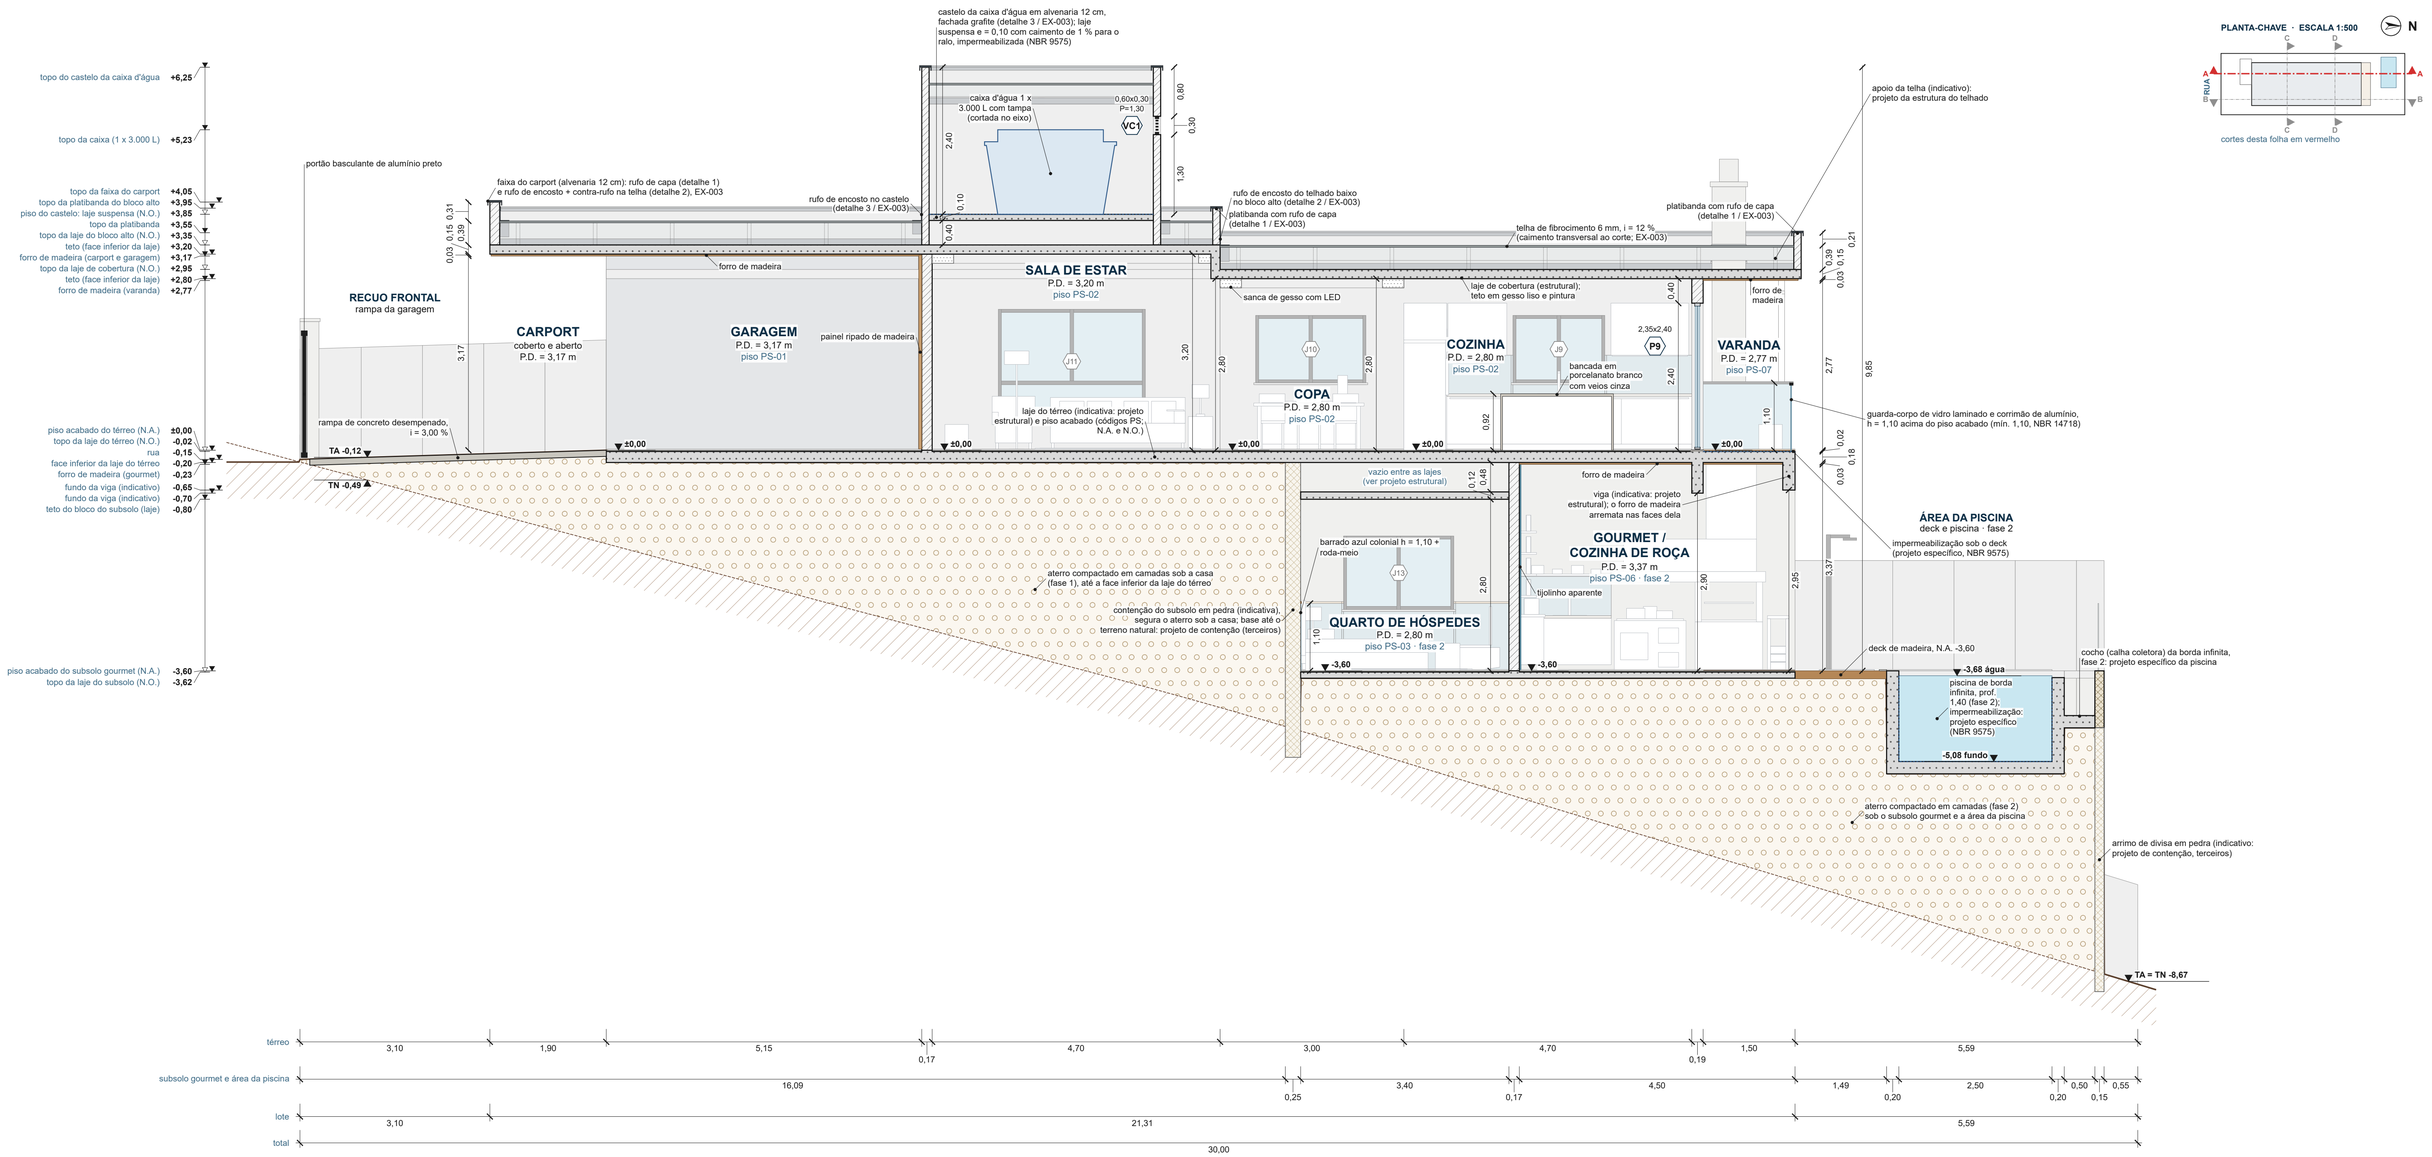

LEGENDA DOS CORTES

- Alvenaria cortada (paredes, platibandas e castelo; espessuras nas plantas)
- Concreto cortado: laje, viga, pilar e degraus (indicativo, projeto estrutural)
- Pedra: paredes externas do subsolo (arquitetura)
- Pedra indicativa (hachura clara): embasamento, contenção e arrimos (terceiros)
- Madeira: forro e painel ripado
- Madeira: batente, alizar e folha de porta
- Deck de madeira
- Piso acabado (topo no N.A.; códigos PS)
- Revestimento de parede (áreas molhadas e barrados)
- Gesso (sanca)
- Granito / mármore: peitoril, soleira e bancada
- Vidro (esquadrias, guarda-corpos e box)
- Alumínio preto (marcos, perfis, trilhos, portão e gradil)
- Pintura grafite (moldura e forro do beiral da capa)
- Telha de fibrocimento 6 mm
- Rufos e calhas em chapa galvanizada pré-pintada
- Apoio da telha (indicativo: estrutura do telhado)
- Caixa d'água de polietileno
- Água da piscina
- Borda da piscina (coping)
- Rampa de concreto (perfil do terreno acabado)
- Impermeabilização (indicativa: projeto específico, NBR 9575)
- Além do plano de corte (linha fina cinza)
- Mobiliário e equipamentos: só vistos, linha fina
- Solo natural; terreno natural TN (tracejado, SRTM 30 m)
- Aterro compactado (sob a casa: fase 1; subsolo e piscina: fase 2); TA (linha cheia)
- Nível acabado N.A. (m, ±0,00 = piso acabado do térreo)
- Nível em osso N.O. (topo da laje); "TA = TN": coincidem
- J1 — Esquadria cortada: L x H (vão) e P = peitoril
- J9 — Esquadria vista além do plano

PISOS NESTA FOLHA

Cód.	Piso (ver quadros Q01/Q03 das plantas)
PS-01	Concreto desempenado, juntas 2,00 x 2,00
PS-02	Porcelanato marmorizado 90 x 90 polido
PS-03	Porcelanato amadeirado 20 x 120
PS-06	Lajota cerâmica rústica 30 x 30
PS-07	Deck de madeira (varanda e área da piscina)

PADRÕES USUAIS ADOTADOS EM 11/10/2026 (reversíveis)

- Vidro laminado 8 mm de segurança em J11; J11 com faixa inferior fixa de vidro laminado 8 mm até 1,10 do piso (travessa desenhada); duto da coifa da gourmet afastado 0,05 da viga (compatibilizar com o projeto estrutural).

NOTAS E HIPÓTESES

1. Somente arquitetura. Estrutura (lajes, vigas, pilares e vergas), fundações, contenção, arrimos e instalações aparecem como INDICATIVOS: dimensionamento e cotas finais nos projetos complementares (terceiros).
2. Cotas em metros com 2 casas, de face acabada a face acabada; as cadeias fecham o total. Níveis em metros em relação ao piso acabado do térreo: ±0,00 (N.A.) = cota 754,15 (SRTM 30 m; confirmar no levantamento planialtimétrico). N.A. = nível acabado do piso; N.O. = nível em osso (topo da laje), abaixo do N.A. na espessura do piso acabado. P.D. medido do piso acabado à face inferior do forro de madeira ou da laje.
3. Planos dos cortes indicados nas plantas EX-001 (térreo), EX-002 (subsolo gourmet) e EX-003 (cobertura) e na planta-chave desta folha.
4. Terreno natural (TN, tracejado) do SRTM; terreno acabado (TA, linha cheia) do projeto ("TA = TN" onde coincidem). Vão sob a casa, entre a frente e a contenção: aterro compactado em camadas até a face inferior da laje do térreo (fase 1; decisão de 09/10/2026). Subsolo gourmet e área da piscina sobre aterro compactado (fase 2), que sobe até a face inferior das peças (cocho e casca da piscina). Drenagem e impermeabilização da contenção por projeto específico.
5. Esquadrias cortadas com marco, folhas, batente, alizar, soleira e peitoril de granito; portas L x H = vão livre de passagem, janelas L x H = vão acabado e P = peitoril (quadros Q02 das plantas EX-001 e EX-002; detalhamento nas EX-014 a EX-016).
6. Pisos (códigos PS) e revestimentos conforme os quadros Q01 e Q03 das plantas; revestimentos das áreas molhadas cotados a partir do piso acabado. Impermeabilização de lajes, box, áreas molhadas, castelo, piscina e contenção conforme projeto de impermeabilização (NBR 9575); a linha azul tracejada marca os pontos críticos (indicativa). Rebaixo e caimento do piso do box para o ralo: no projeto de impermeabilização.
7. Guarda-corpos com altura mínima de 1,10 m acima do piso acabado (NBR 14718); a altura cotada é a do modelo. Cobertura, calhas, rufos e castelo da caixa d'água: ver EX-003 (detalhes 1 a 4). Apoios da telha (terças e pontaletes, tracejados) indicativos: projeto da estrutura do telhado.
8. Mobiliário e equipamentos só vistos além do plano, em linha fina (indicativos).
9. Contenção, embasamento e arrimos em pedra (hachura clara) seguram o aterro; base desenhada = a do modelo, INDICATIVA: profundidade e fundação no projeto de contenção (terceiros), após levantamento e sondagem.
10. Borda infinita (cocho, topo -3,60; 4,96 m acima do terreno natural junto do muro, corte AA): sem guarda-corpo no vertedouro (padrão usual de 11/10/2026): a lâmina d'água é a barreira; cocho só de manutenção; guarda-corpo do terraço nos trechos laterais.

AVISO: Projeto executivo de ARQUITETURA (somente arquitetura). Implantação, aterro e arrimos dependem do levantamento planialtimétrico; estrutura, contenção e instalações ficam com os projetos complementares (terceiros).

0 1 2 3 4 5 m
ESCALA GRÁFICA

REV.	DATA	DESCRIÇÃO	POR
R04	**08/10/2026**	**Emissão do executivo (Cleber): cotas 2 casas, cobertura EX-003, caixa 1 x 3.000 L e porta PC1**	**KMZERO**
R04	07/10/2026	Revisão 4 (Ana Paula): ilha clara, banheiros e pendentes da suíte	KMZERO
R03	07/10/2026	Revisão 3 (Cleber): entrada pela sala, cozinha nos fundos com a varanda	KMZERO
R02	06/10/2026	Revisão 2 (Cleber): varanda 1,50, subsolo gourmet aterrado, gourmet nos fundos, portas, interiores	KMZERO
R01	06/10/2026	Revisão 1 (Cleber): recuos 1,50, cozinha em U, piso +0,15, cobertura, subsolo gourmet	KMZERO
R00	29/09/2026	Emissão inicial — estudo preliminar	KMZERO

KMZERO | ENGENHARIA · ARQUITETURA

EMPREENDIMENTO	LOCAL	ETAPA
RESIDÊNCIA ANA PAULA	Rio Espera / MG	**PROJETO EXECUTIVO**

CONTEÚDO DA PRANCHA

CORTE AA (LONGITUDINAL)

DESENHO	RESPONSÁVEL TÉCNICO	REGISTRO PROFISSIONAL
KMZERO	Kleber Vieira Martins · Arquitetura	ART/RRT a emitir

REVISÃO	DATA	ESCALA	UNIDADE	CÓDIGO DA PRANCHA
R04	07/10/2026	1:50	metro (m)	**AP-ARQ-EX-004**

Direitos autorais reservados à KMZERO. Cliente: Ana Paula.