

COZINHA — PLANTA AMPLIADA E VISTAS

N ESCALA 1:25 · A = 15,18 m² · P.D. 2,80 · piso PS-02 · N.A. ±0,00 · planta cortada a 1,20 m do piso acabado · paginação do piso: equilibrada, campo único com sala de estar e copa (oeste-leste: junta no eixo; sul-norte: junta no eixo), peças de 900 x 900 mm

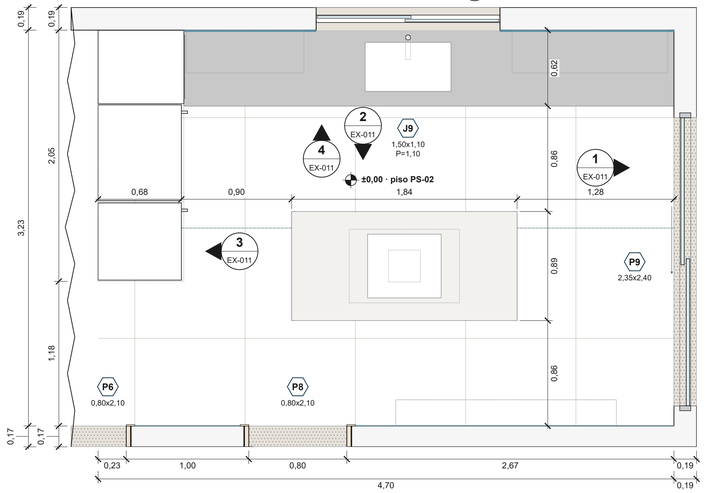


VISTA 1 — parede norte

ESCALA 1:25 · plano da vista a 0,64 m da parede

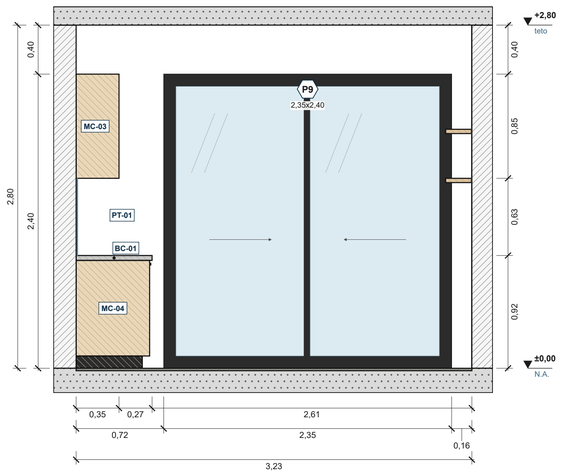

VISTA 2 — parede leste (ilha à frente)

ESCALA 1:25 · plano da vista a 2,60 m da parede

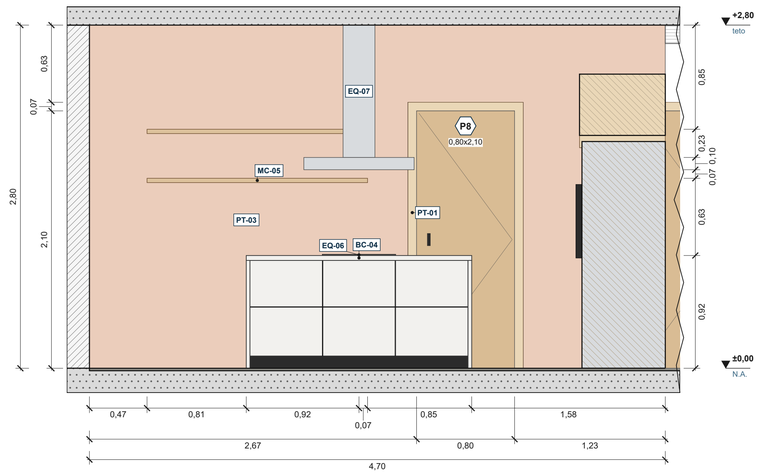

VISTA 3 — sul (torres)

ESCALA 1:25 · plano da vista a 1,16 m da parede

VISTA 4 — parede oeste (pia)

ESCALA 1:25 · plano da vista a 1,05 m da parede

LEGENDA

- Alvenaria cortada
- Laje, viga, pilar cortados (indicativos)
- Piso acabado (N.A.)
- Revestimento de parede cortado
- Sanca de gesso cortada (vista além: contorno)
- Paginação (módulo de referência)
- Vidro do box e das esquadrias
- Louça, bancada, marcenaria, equipamento
- Marcenaria / bancada cortada pelo plano da vista
- Peça oculta (cuba de embutir, aparelho atrás)
- Projeção acima do plano de corte da planta
- Código dos quadros desta folha (RV-nn)
- J1 — Esquadria: Q02, L x H e P = peitoril
- 1 / EX-011 — Vista: número e folha (seta = visada)
- Eixo / início da paginação
- Nível acabado N.A. (±0,00 = térreo)

QUADRO DE REVESTIMENTOS, PINTURAS E TAMPOS (conferir as peças compradas antes de paginar)

Cód.	Material (texto do Q03 e dos cortes)	Peça (módulo de ref.)	Acabamento	Junta / rejunte	Paginação	Altura do N.A. (m)	Onde
BC-01	bancada em granito (cozinha: granito cinza, decisão R04)	esp. 0,04; prof. 0,62	a definir com a cliente	—	sem saia / frontão (a definir)	h = 0,92	Cozinha
BC-04	ilha em porcelanato branco com veios cinza, efeito mármore (decisão R04)	esp. 0,04; prof. 0,89	a definir com a cliente	—	sem saia / frontão (a definir)	h = 0,92	Cozinha
PT-01	reboco + massa + pintura branca	—	a definir com a cliente	—	—	—	Cozinha
PT-03	parede do meio em terracota + prateleiras	—	a definir com a cliente	—	—	h = 2,80 (até o teto)	Cozinha
RV-04	metrô verde atrás da bancada	300 x 75 mm (ref. render)	a definir com a cliente	3 mm (azulejo)	meia-peça, no eixo da J9	h = 0,92 a 1,55; 1,10 a 1,55; 0,92 a 1,07	Cozinha

QUADRO DE LOUÇAS, METAIS, ACESSÓRIOS, MARCENARIA E EQUIPAMENTOS (layout; modelo e fabricante a definir com a cliente)

Cód.	Peça (descrição genérica)	Medidas do modelo L x P x H (m)	Acabamento (modelo)	Onde
LO-03	cuba de inox de embutir (sob o tampo)	0,70 x 0,40 x 0,13	inox	Cozinha
ME-04	torneira de mesa (pia)	0,04 x 0,04 x 0,36	inox	Cozinha
MC-02	armário / torre de madeira até 2,40	0,60 x 0,70 x 2,40	madeira	Cozinha
MC-03	armário aéreo de madeira	1,45 x 0,70 x 0,60 / 1,27 x 0,35 x 0,85 / 0,96 x 0,35 x 0,85	madeira	Cozinha
MC-04	móvel de madeira sob o tampo	4,00 x 0,60 x 0,78	madeira	Cozinha
MC-05	prateleira de madeira rústica	1,80 x 0,21 x 0,04	madeira	Cozinha
EQ-01	forno elétrico de embutir (equipamento indicativo)	0,52 x 0,60 (L x H); profundidade (aparelho) a definir	a definir	Cozinha
EQ-02	micro-ondas de embutir (equipamento indicativo)	0,52 x 0,36 (L x H); profundidade (aparelho) a definir	a definir	Cozinha
EQ-03	geladeira duplex (equipamento indicativo)	0,78 x 0,68 x 1,85	a definir	Cozinha
EQ-04	freezer vertical (equipamento indicativo)	0,63 x 0,68 x 1,75	a definir	Cozinha
EQ-05	lava-louças sob a bancada (equipamento indicativo)	0,60 x 0,74 (L x H); profundidade (aparelho) a definir	a definir	Cozinha
EQ-06	cooktop de indução (equipamento indicativo)	0,60 x 0,52 (L x P); altura (aparelho) a definir	a definir	Cozinha
EQ-07	coifa de ilha com duto (equipamento indicativo)	0,90 x 0,60 x 1,18	a definir	Cozinha

PENDÊNCIAS DO MODELO (decisão do Cleber)

8. Cozinha: o armário aéreo de madeira (MC-03) fica 0,02 à frente do micro-ondas (EQ-02) e cobre 60 % da frente dele (1,62 a 1,98): a porta não abre; rever a peça ou a posição do aparelho.
9. Cozinha: torres e armários até 2,40 com a laje a 2,80: fechamento dos 0,40 até o teto a definir.
10. Paginação de parede, recortes abaixo de 1/3 da peça (distribuir na ponta ou ajustar a peça): Cozinha (RV-04), vista 4: 0,03 nas pontas, em a = 0,70 (fiadas alternadas); 0,07 nas pontas, no canto norte (fiadas alternadas).

NOTAS E HIPÓTESES

1. Somente arquitetura: estrutura, contenção, impermeabilização e instalações são INDICATIVAS (projetos complementares, terceiros). Sem pontos de instalação: louças, metais e acessórios só como layout.
2. Cotas em metros com 2 casas, de face acabada a face acabada, fechando o total. Alturas a partir do piso acabado (N.A.: térreo ±0,00; subsolo gourmet -3,60); P.D. até o forro de madeira ou a laje (Q01 e cortes EX-004 a EX-006). Acessórios (papeleira, toalheiro, registro) cotados pelo eixo, na vertical e na horizontal.
3. Pisos PS conforme Q01/Q03 (EX-001/EX-002); RV, PT e BC conforme o quadro desta folha (textos do Q03 e dos cortes EX-004 a EX-006). Paginação de parede: módulo de referência (piso ou render; conferir as peças compradas); juntas de 2 mm nos retificados e 3 mm nos azulejos (fabricante); verticais pela coluna "Paginação" (marcada na vista), horizontais a partir do N.A.
4. Impermeabilização do box, das áreas molhadas e das paredes junto da contenção: projeto específico (NBR 9575, indicativa). Rebaixo, caimento e ralos (linear ou sifonado): hidrossanitário e impermeabilização.
5. Louças, metais, equipamentos e acessórios genéricos: modelo e acabamento a definir com a cliente; conferir os aparelhos comprados antes da marcenaria e das bancadas. Alturas: NBR 9050 como referência (sem barras).
6. Esquadrias: Q02 das EX-001/EX-002 e EX-014 a EX-016 (portas L x H = vão livre de passagem; janelas L x H = vão acabado; P = peitoril). Planos das vistas nas plantas ampliadas; o que o plano corta sai hachurado.
7. Padrões usuais adotados em 11/10/2026 (decisão do Cleber, reversíveis): piso equilibrado — partida no eixo que deixa os maiores recortes, mínimo de 1/3 da peça (também nas paredes), box com junta no vidro (cozinha em campo único com sala de estar e copa).

AVISO: Projeto executivo de ARQUITETURA (somente arquitetura). Implantação, aterro e arrimos dependem do levantamento planialtimétrico; estrutura, contenção e instalações ficam com os projetos complementares (terceiros).

0 — 1 — 2 m
ESCALA GRÁFICA

REV.	DATA	DESCRIÇÃO	POR
R04	**08/10/2026**	**Emissão do executivo (Cleber): cotas 2 casas, cobertura EX-003, caixa 1 x 3.000 L e porta PC1**	**KMZERO**
R04	07/10/2026	Revisão 4 (Ana Paula): ilha clara, banheiros e pendentes da suíte	KMZERO
R03	07/10/2026	Revisão 3 (Cleber): entrada pela sala, cozinha nos fundos com a varanda	KMZERO
R02	06/10/2026	Revisão 2 (Cleber): varanda 1,50, subsolo gourmet aterrado, gourmet nos fundos, portas, interiores	KMZERO
R01	06/10/2026	Revisão 1 (Cleber): recuos 1,50, cozinha em U, piso +0,15, cobertura, subsolo gourmet	KMZERO
R00	29/09/2026	Emissão inicial — estudo preliminar	KMZERO

KMZERO | ENGENHARIA · ARQUITETURA

EMPREENDIMENTO	LOCAL	ETAPA
RESIDÊNCIA ANA PAULA	Rio Espera / MG	**PROJETO EXECUTIVO**

CONTEÚDO DA PRANCHA

VISTAS INTERNAS — COZINHA

DESENHO	RESPONSÁVEL TÉCNICO	REGISTRO PROFISSIONAL
KMZERO	Kleber Vieira Martins · Arquitetura	ART/RRT a emitir

REVISÃO	DATA	ESCALA	UNIDADE	CÓDIGO DA PRANCHA
R04	07/10/2026	1:25	metro (m)	**AP-ARQ-EX-011**

Direitos autorais reservados à KMZERO. Cliente: Ana Paula.