

GOURMET / COZINHA DE ROÇA — PLANTA AMPLIADA E VISTAS

N ESCALA 1:25 · A = 30,38 m² · P.D. 3,37 · piso PS-06 · N.A. -3,60 · planta cortada a 1,20 m do piso acabado · paginação do piso: equilibrada (oeste-leste: peça no eixo; sul-norte: peça no eixo), peças de 300 x 300 mm

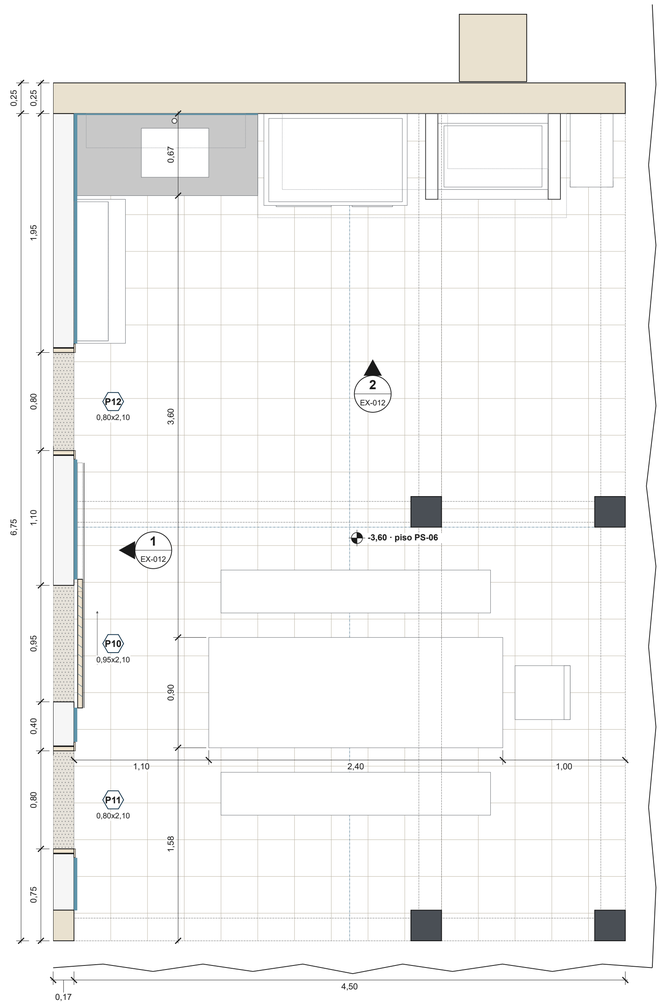


VISTA 1 — parede sul

ESCALA 1:25 · plano da vista a 0,76 m da parede

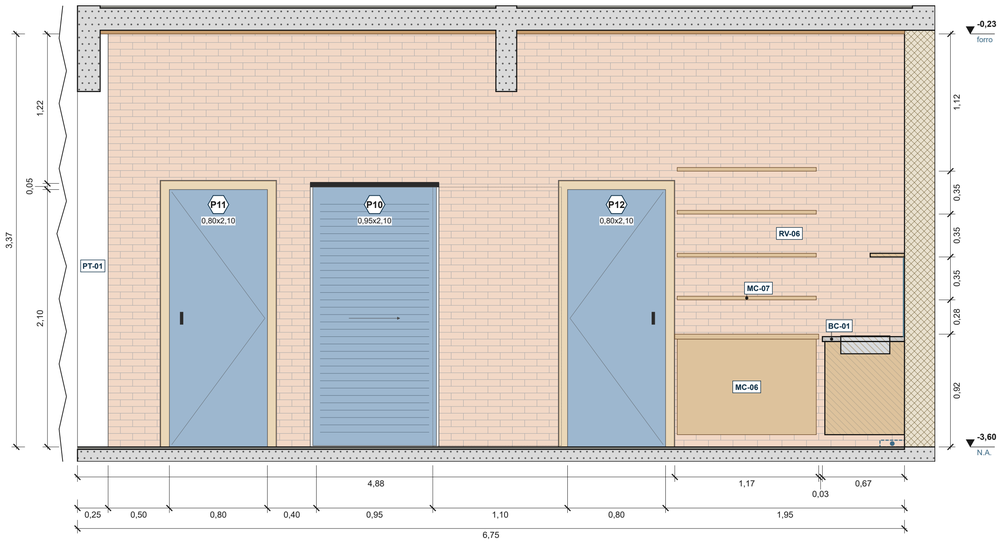

VISTA 2 — parede oeste

ESCALA 1:25 · plano da vista a 2,29 m da parede

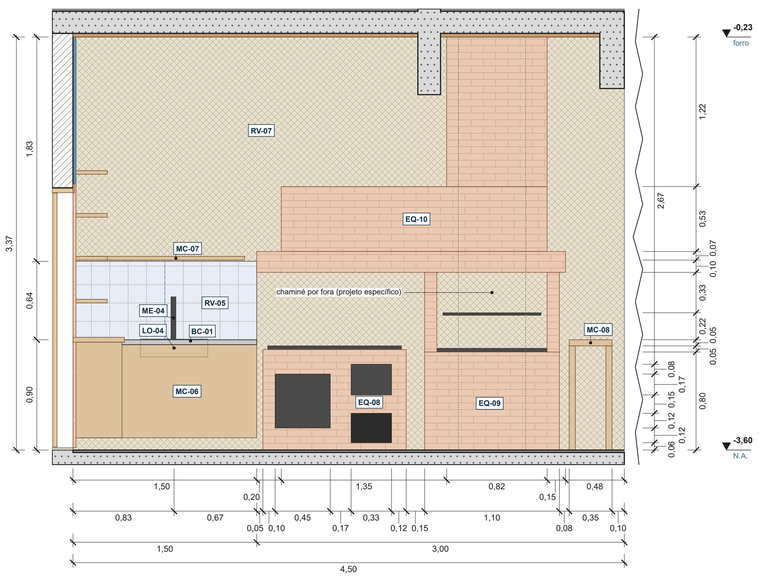

LEGENDA

- Alvenaria cortada
- Laje, viga, pilar cortados (indicativos)
- Pilar cortado na planta (indicativo)
- Pedra / contenção cortada (indicativa)
- Piso acabado (N.A.)
- Revestimento de parede cortado
- Paginação (módulo de referência)
- Vidro do box e das esquadrias
- Louça, bancada, marcenaria, equipamento
- Marcenaria / bancada cortada pelo plano da vista
- Peça oculta (cuba de embutir, aparelho atrás)
- Projeção acima do plano de corte da planta
- RV-nn — Código dos quadros desta folha
- J1 — Esquadria: Q02, L x H e P = peitoril
- 1 / EX-012 — Vista: número e folha (seta = visada)
- Eixo / início da paginação
- Início da paginação: 1ª peça inteira
- Nível acabado N.A. (±0,00 = térreo)

NOTAS E HIPÓTESES

1. Somente arquitetura: estrutura, contenção, impermeabilização e instalações são INDICATIVAS (projetos complementares, terceiros). Sem pontos de instalação: louças, metais e acessórios só como layout.
2. Cotas em metros com 2 casas, de face acabada a face acabada, fechando o total. Alturas a partir do piso acabado (N.A.: térreo ±0,00; subsolo gourmet -3,60); P.D. até o forro de madeira ou a laje (Q01 e cortes EX-004 a EX-006). Acessórios (papeleira, toalheiro, registro) cotados pelo eixo, na vertical e na horizontal.
3. Pisos PS conforme Q01/Q03 (EX-001/EX-002); RV, PT e BC conforme o quadro desta folha (textos do Q03 e dos cortes EX-004 a EX-006). Paginação de parede: módulo de referência (piso ou render; conferir as peças compradas); juntas de 2 mm nos retificados e 3 mm nos azulejos (fabricante); verticais pela coluna "Paginação" (marcada na vista), horizontais a partir do N.A.
4. Impermeabilização do box, das áreas molhadas e das paredes junto da contenção: projeto específico (NBR 9575, indicativa). Rebaixo, caimento e ralos (linear ou sifonado): hidrossanitário e impermeabilização.
5. Louças, metais, equipamentos e acessórios genéricos: modelo e acabamento a definir com a cliente; conferir os aparelhos comprados antes da marcenaria e das bancadas. Alturas: NBR 9050 como referência (sem barras).
6. Esquadrias: Q02 das EX-001/EX-002 e EX-014 a EX-016 (portas L x H = vão livre de passagem; janelas L x H = vão acabado; P = peitoril). Planos das vistas nas plantas ampliadas; o que o plano corta sai hachurado.
7. Padrões usuais adotados em 11/10/2026 (decisão do Cleber, reversíveis): piso equilibrado — partida no eixo que deixa os maiores recortes, mínimo de 1/3 da peça (também nas paredes), box com junta no vidro; gourmet: pedra mineira aparente (RV-07) e duto da coifa afastado da viga.

QUADRO DE REVESTIMENTOS, PINTURAS E TAMPOS (conferir as peças compradas antes de paginar)

Cód.	Material (texto do Q03 e dos cortes)	Peça (módulo de ref.)	Acabamento	Junta / rejunte	Paginação	Altura do N.A. (m)	Onde
BC-01	bancada em granito	esp. 0,04; prof. 0,67	a definir com a cliente	—	sem saia / frontão (a definir)	h = 0,90	Gourmet / cozinha de roça
PT-01	reboco + massa + pintura branca	—	a definir com a cliente	—	—	—	Gourmet / cozinha de roça
RV-05	azulejo colonial atrás da pia	150 x 150 mm (ref. render)	a definir com a cliente	3 mm (azulejo)	prumo, nas juntas do piso PS-06	h = 0,90 a 1,54	Gourmet / cozinha de roça
RV-06	tijolinho aparente	200 x 55 mm (ref. render)	a definir com a cliente	conforme o fabricante	meia-peça, do canto oeste	h = 3,37 (até o forro)	Gourmet / cozinha de roça
RV-07	pedra mineira aparente (face interna das paredes de pedra)	pedra do modelo (parede)	natural (pedra do modelo)	—	—	h = 3,37 (até o forro)	Gourmet / cozinha de roça

QUADRO DE LOUÇAS, METAIS, ACESSÓRIOS, MARCENARIA E EQUIPAMENTOS (layout; modelo e fabricante a definir com a cliente)

Cód.	Peça (descrição genérica)	Medidas do modelo L x P x H (m)	Acabamento (modelo)	Onde
LO-04	cuba de inox de embutir (sob o tampo)	0,55 x 0,40 x 0,15	inox	Gourmet / cozinha de roça
ME-04	torneira de mesa (pia)	0,04 x 0,04 x 0,35	ferro fundido preto	Gourmet / cozinha de roça
MC-06	móvel de madeira sob o tampo (rústico)	1,50 x 0,65 x 0,76 / 1,18 x 0,42 x 0,82	madeira	Gourmet / cozinha de roça
MC-07	prateleira de madeira rústica	1,30 x 0,28 x 0,03 / 1,14 x 0,28 x 0,03	madeira	Gourmet / cozinha de roça
MC-08	lenheiro: tampo de madeira rústica sobre pés, lenha embaixo	0,35 x 0,60 x 0,90	madeira	Gourmet / cozinha de roça
EQ-08	fogão a lenha em alvenaria com tijolinho (RV-06), chapa e portas de ferro	corpo 1,17 x 0,75 x 0,82; chapa 1,09 x 0,68 a 0,82; portas (L x H, do N.A.): forno 0,45 x 0,44 a 0,18, cinzeiro 0,33 x 0,24 a 0,06, fornalha 0,33 x 0,25 a 0,45; indicativo: conferir com as peças compradas	tijolinho; ferro fundido	Gourmet / cozinha de roça
EQ-09	churrasqueira em alvenaria com tijolinho (RV-06), braseiro e grelha de ferro	corpo 1,10 x 0,70 x 1,45; braseiro 0,94 x 0,54 a 0,80; grelha 0,80 x 0,50 a 1,10; indicativo: conferir com as peças compradas	tijolinho; ferro	Gourmet / cozinha de roça
EQ-10	coifa e duto em alvenaria com tijolinho (RV-08) até o forro; tiragem e chaminé por projeto específico	saia 2,52 x 0,85 (L x P), de 1,45 a 1,62; corpo 2,17 x 0,62 (L x P), de 1,62 a 2,15; duto 0,82 x 0,45 (L x P), de 2,15 ao forro	tijolinho	Gourmet / cozinha de roça

PENDÊNCIAS DO MODELO (decisão do Cleber)

8. Gourmet: duto, tiragem e chaminé do fogão a lenha e da churrasqueira por projeto específico (indicativos). O piso de lajota não tem ralo nem caimento junto da pia no modelo (não inventado).
9. Paginação de parede, recortes abaixo de 1/3 da peça (distribuir na ponta ou ajustar a peça): Gourmet / cozinha de roça (RV-06), vista 1: 0,03 nas pontas, junto da P11 (fiadas alternadas); 0,05 nas pontas, junto da P10 (fiadas alternadas).
10. Gourmet / cozinha de roça, vista 1: a folha da P10 (1,05) corre aparente sobre a parede (trilho aparente); aberta, ocupa de a = 2,90 a 3,95 e passa 0,02 sobre o alizar da P12 (entre a P10 e o alizar da P12 ficam 1,03 para a folha de 1,05): rever a folha, o alizar ou a posição das portas.

AVISO: Projeto executivo de ARQUITETURA (somente arquitetura). Implantação, aterro e arrimos dependem do levantamento planialtimétrico; estrutura, contenção e instalações ficam com os projetos complementares (terceiros).

0 1 2 m
ESCALA GRÁFICA

REV.	DATA	DESCRIÇÃO	POR
R04	**08/10/2026**	**Emissão do executivo (Cleber): cotas 2 casas, cobertura EX-003, caixa 1 x 3.000 L e porta PC1**	**KMZERO**
R04	07/10/2026	Revisão 4 (Ana Paula): ilha clara, banheiros e pendentes da suíte	KMZERO
R03	07/10/2026	Revisão 3 (Cleber): entrada pela sala, cozinha nos fundos com a varanda	KMZERO
R02	06/10/2026	Revisão 2 (Cleber): varanda 1,50, subsolo gourmet aterrado, gourmet nos fundos, portas, interiores	KMZERO
R01	06/10/2026	Revisão 1 (Cleber): recuos 1,50, cozinha em U, piso +0,15, cobertura, subsolo gourmet	KMZERO
R00	29/09/2026	Emissão inicial — estudo preliminar	KMZERO

KMZERO | ENGENHARIA · ARQUITETURA

EMPREENDIMENTO	LOCAL	ETAPA
RESIDÊNCIA ANA PAULA	Rio Espera / MG	**PROJETO EXECUTIVO**

CONTEÚDO DA PRANCHA

VISTAS INTERNAS — GOURMET / COZINHA DE ROÇA

DESENHO	RESPONSÁVEL TÉCNICO	REGISTRO PROFISSIONAL
KMZERO	Kleber Vieira Martins · Arquitetura	ART/RRT a emitir

REVISÃO	DATA	ESCALA	UNIDADE	CÓDIGO DA PRANCHA
R04	07/10/2026	1:25	metro (m)	**AP-ARQ-EX-012**

Direitos autorais reservados à KMZERO. Cliente: Ana Paula.