QUADRO GERAL DE ESQUADRIAS E DETALHES TÍPICOS

ESCALA 1:5 / 1:10 · quadro geral sem escala · detalhes típicos indicativos com as medidas do modelo · cotas em metros (perfis em mm)


QUADRO GERAL DE ESQUADRIAS

Cód.	L (m)	H (m)	Peit. (m)	Tipologia	Material	Vidro	Ambientes	Qtd.	Folha
TÉRREO									
P1	0,90	2,30	0,00	correr embutida (kit na parede)	madeira maciça (a definir)	—	Garagem / Sala de estar	1	EX-014
P2	0,80	2,10	0,00	correr aparente	madeira maciça · trilho preto aparente	—	Sala de estar / Hall íntimo	1	EX-014
P3	0,80	2,10	0,00	giro 1 folha	madeira semi-oca ou maciça (a definir)	—	Suíte / Hall íntimo	1	EX-014
P4	0,90	2,10	0,00	passagem livre (sem folha)	vão com guarnição de madeira	—	Suíte / Closet	1	EX-014
P5	0,80	2,10	0,00	correr embutida (kit na parede)	madeira maciça (a definir)	—	Closet / Banho da suíte	1	EX-014
P6	0,80	2,10	0,00	giro 1 folha	madeira semi-oca ou maciça (a definir)	—	Copa / Banheiro social	1	EX-014
P7	0,80	2,10	0,00	giro 1 folha	madeira semi-oca ou maciça (a definir)	—	Copa / Quarto 2	1	EX-014
P8	0,80	2,10	0,00	giro 1 folha	madeira semi-oca ou maciça (a definir)	—	Cozinha / Quarto 3	1	EX-014
P9	2,35	2,40	0,00	correr, folhas de vidro	vidro temperado incolor 8 mm + alumínio preto	temperado incolor 8 mm	Cozinha / Varanda	1	EX-014
J1	1,90	2,40	0,30	fixa (+ bandeira)	alumínio preto + vidro laminado 8 mm	laminado 8 mm	Suíte	1	EX-015
J2	2,00	1,10	1,10	correr 2 folhas	alumínio preto + vidro incolor 6 mm	incolor 6 mm	Suíte	1	EX-015
J3	1,00	0,60	1,50	basculante	alumínio preto + vidro mini-boreal 4 mm	mini-boreal 4 mm	Closet	1	EX-015
J4	1,20	0,60	1,50	maxim-ar	alumínio preto + vidro mini-boreal 4 mm	mini-boreal 4 mm	Banho da suíte	1	EX-015
J5	1,20	0,60	1,50	maxim-ar	alumínio preto + vidro mini-boreal 4 mm	mini-boreal 4 mm	Banheiro social	1	EX-015
J6	2,00	1,10	1,10	correr 2 folhas	alumínio preto + vidro incolor 6 mm	incolor 6 mm	Quarto 2	1	EX-015
J7	2,00	1,10	1,10	correr 2 folhas	alumínio preto + vidro incolor 6 mm	incolor 6 mm	Quarto 3	1	EX-015
J8	2,30	1,80	0,60	correr 2 folhas	alumínio preto + vidro laminado 8 mm	laminado 8 mm	Quarto 3	1	EX-015
J9	1,50	1,10	1,10	correr 2 folhas	alumínio preto + vidro incolor 6 mm	incolor 6 mm	Cozinha	1	EX-015
J10	1,80	1,10	1,10	correr 2 folhas	alumínio preto + vidro incolor 6 mm	incolor 6 mm	Copa	1	EX-015
J11	2,40	1,70	0,60	correr 2 folhas + fixo inferior	alumínio preto + vidro laminado 8 mm	laminado 8 mm	Sala de estar	1	EX-015
SUBSOLO GOURMET — FASE 2 (obra posterior à casa, EX-002)									
P10	0,95	2,10	0,00	correr veneziana	madeira azul colonial · trilho preto	—	Lavanderia / Gourmet / cozinha de roça	1	EX-014
P11	0,80	2,10	0,00	giro 1 folha	madeira pintada azul colonial (gourmet de roça)	—	Banheiro / Gourmet / cozinha de roça	1	EX-014
P12	0,80	2,10	0,00	giro 1 folha	madeira pintada azul colonial (gourmet de roça)	—	Quarto de hóspedes / Gourmet / cozinha de roça	1	EX-014
J12	1,10	0,60	1,50	maxim-ar	alumínio preto + vidro mini-boreal 4 mm	mini-boreal 4 mm	Banheiro	1	EX-015
J13	1,80	1,20	1,00	correr 2 folhas	alumínio preto + vidro incolor 6 mm	incolor 6 mm	Quarto de hóspedes	1	EX-015
CASTELO DA CAIXA D'ÁGUA (cobertura, EX-003)									
PC1	0,80	1,60	0,05	giro 1 folha, metal vazado	alumínio preto brilhante + tela inox	— (vazada)	Castelo da caixa d'água / cobertura	1	EX-014
VC1	0,60	0,30	1,30	veneziana fixa	alumínio preto brilhante	— (sem vidro, lâminas)	Castelo da caixa d'água	1	EX-015
				TOTAL: 13 portas e 14 janelas				27	

Campos comuns iguais ao Q02 das EX-001/EX-002; PC1 e VC1 do castelo (EX-003): Peit. = soleira / peitoril acima do piso do castelo. Agrupado por pavimento; subsolo gourmet na FASE 2 (obra posterior), com Peit. medido do piso do subsolo gourmet. Elevação de cada tipo na folha indicada.


1 PEITORIL DE GRANITO COM PINGADEIRA

ESCALA 1:5 · seção vertical pela janela de correr na parede externa (típico; J12 e J13 na parede de 250 mm): peitoril passante, pingadeira, caimento para fora, marco e contramarco

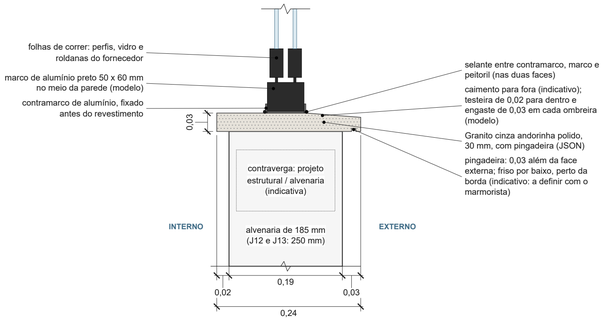


2 MARCO E CONTRAMARCO DE ALUMÍNIO — OMBREIRA E VERGA

ESCALA 1:5 · seção horizontal na ombreira e vertical na verga: contramarco antes do revestimento, marco no meio da parede, vedação com selante

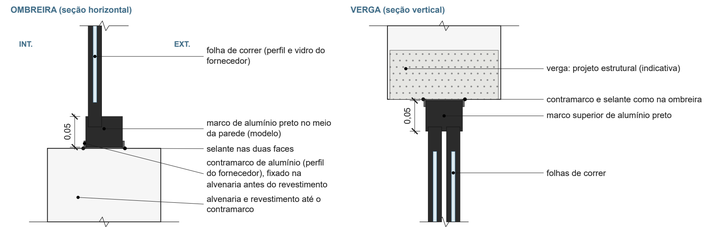


3 SOLEIRA DE GRANITO — PORTAS INTERNAS

ESCALA 1:5 · seção pelo vão: soleira no nível do piso acabado, na troca de piso

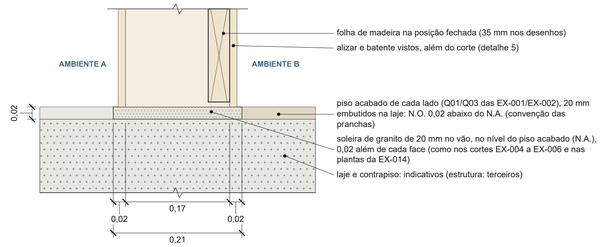


4 SOLEIRA DA PORTA DE CORRER DE VIDRO P9

ESCALA 1:5 · seção cozinha / varanda: trilho inferior, soleira de granito e caimento para a varanda

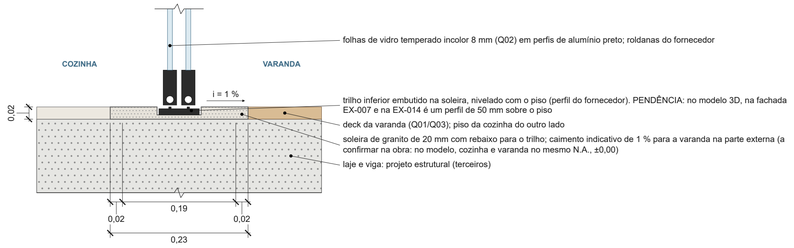


5 BATENTE E ALIZAR — PORTA DE GIRO DE MADEIRA

ESCALA 1:5 · seção horizontal na ombreira da parede interna: batente de 35 mm, alizar de 70 mm nas duas faces, folha e dobradiça

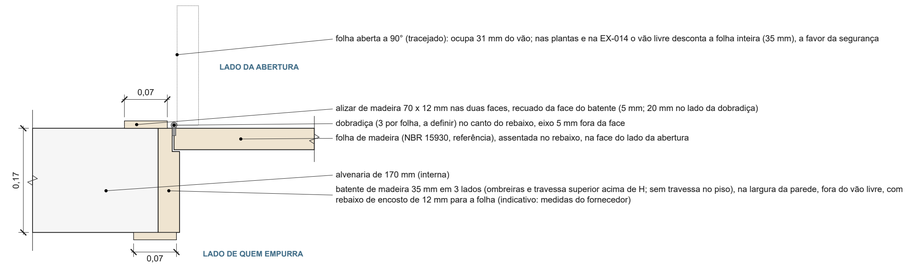

6 PORTA DE CORRER EMBUTIDA (KIT NA PAREDE) — P1 E P5


ESCALA 1:10 · planta: caixa do kit na parede interna, folha fechada e aberta, guias e alizares; faixa do kit sem tubulação e sem fixação

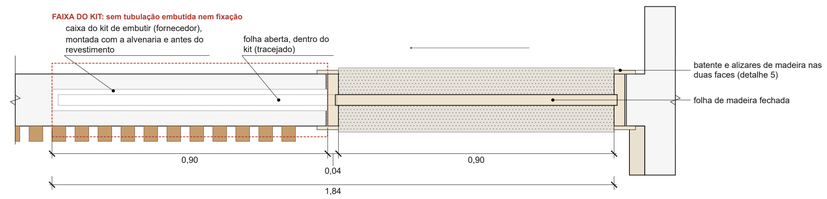

P1 cotada (kit 0,90, vão 0,90). P5: kit 0,80 e vão 0,80 (o mesmo detalhe). Ripado e pedra da garagem cortados (modelo).

7 PORTA DE CORRER APARENTE — TRILHO SUPERIOR (P2 E P10)

ESCALA 1:5 · seção vertical: trilho de alumínio preto na verga, folha afastada da face acabada (P10 sobre o tijolinho), guia de piso

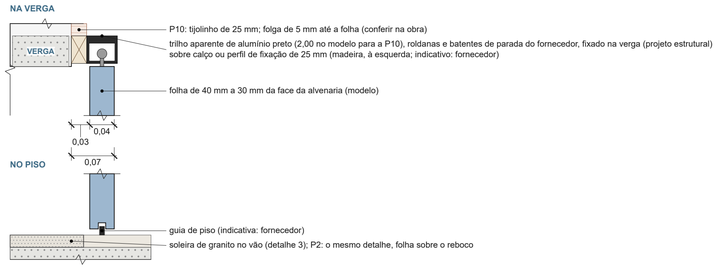

ESCALAS GRÁFICAS



ESCALA 1:5 (detalhes 1 a 5 e 7)



ESCALA 1:10 (detalhe 6)

LEGENDA

- Alvenaria cortada
- Concreto: laje e verga (indicativos, estrutura)
- Granito: peitoril e soleira
- Madeira: folha, batente, alizar e calço
- Alumínio preto: marco, contramarco, trilho
- Vidro
- Piso acabado (20 mm, no N.A.)
- Tijolinho (gourmet)
- Pedra cortada (revestimento da garagem)
- Ripado de madeira da garagem (cortado)
- Deck de madeira da varanda
- Selante
- Folha aberta / peça além do corte

REMISSÃO

PC1 (porta de acesso à caixa d'água): detalhe 3 (CASTELO DA CAIXA D'ÁGUA — CORTE PELA PORTA PC1, 1:25) — EX-003; detalhe 4 (PORTA PC1 — VISTA EXTERNA, 1:20) — EX-003.

NOTAS E HIPÓTESES

1. Quadro geral: mesmos campos do Q02 das EX-001/EX-002 (Cód., L, H, Peit., Tipologia, Material, Ambientes, Qtd.), mais a PC1 e a VC1 do castelo (EX-003), o vidro e a folha da elevação de cada tipo (EX-014 portas, EX-015 janelas), agrupados por pavimento (térreo, subsolo gourmet da FASE 2, castelo). L x H: portas = vão livre de passagem; janelas = vão acabado.
2. Detalhes típicos indicativos (NBR 6492): perfis, contramarco, ancoragens, vedações e desempenho pelo fornecedor (projeto de fabricação de terceiros; NBR 10821 e NBR 15930 como referência).
3. Vergas e contravergas: projeto estrutural e de alvenaria (terceiros); nos detalhes, só indicadas.
4. Janelas: vão acabado; portas: vão livre de passagem (nota 1); conferir na obra antes de fabricar; contramarco antes do revestimento; selante nas juntas entre marco, contramarco, peitoril e soleira.
5. Peitoril: Granito cinza andorinha polido, 30 mm, com pingadeira (JSON); J1 sem granito: a base da moldura grafite, com caimento e pingadeira, faz o peitoril; soleiras de granito de 20 mm no nível do piso acabado, 0,02 além de cada face (como nos cortes EX-004 a EX-006). Caimentos indicativos: confirmar na obra.
6. Padrões usuais adotados em 11/10/2026 (reversíveis): portas de giro com folha de 0,80 (padrão de mercado; vão livre de 0,77 com a folha aberta) e batente de madeira em 3 lados, sem travessa no piso; H = vão livre, com o batente acima de H; J2, J6, J7 e J10 com P = 1,10 e H = 1,10 (verga mantida em 2,20), proteção contra queda; J11 com faixa inferior fixa de vidro laminado 8 mm até 1,10; vidro laminado 8 mm de segurança em J1, J8 e J11; J1 com o peitoril na base da moldura grafite (caimento e pingadeira, sem granito).
7. Kits de porta de correr embutida e trilhos aparentes: modelo e fixação a definir com o fornecedor; faixa do kit sem tubulação nem fixação.
8. PC1: detalhes 3 (castelo, 1:25) e 4 (porta, 1:20) da EX-003.
9. Vidros conforme a NBR 7199; cores, ferragens e acabamentos a definir com a cliente.

AVISO: Projeto executivo de ARQUITETURA (somente arquitetura). Implantação, aterro e arrimos dependem do levantamento planialtimétrico; estrutura, contenção e instalações ficam com os projetos complementares (terceiros).

REV.	DATA	DESCRIÇÃO	POR
R04	**08/10/2026**	**Emissão do executivo (Cleber): cotas 2 casas, cobertura EX-003, caixa 1 x 3.000 L e porta PC1**	**KMZERO**
R04	07/10/2026	Revisão 4 (Ana Paula): ilha clara, banheiros e pendentes da suíte	KMZERO
R03	07/10/2026	Revisão 3 (Cleber): entrada pela sala, cozinha nos fundos com a varanda	KMZERO
R02	06/10/2026	Revisão 2 (Cleber): varanda 1,50, subsolo gourmet aterrado, gourmet nos fundos, portas, interiores	KMZERO
R01	06/10/2026	Revisão 1 (Cleber): recuos 1,50, cozinha em U, piso +0,15, cobertura, subsolo gourmet	KMZERO
R00	29/09/2026	Emissão inicial — estudo preliminar	KMZERO

KMZERO | ENGENHARIA · ARQUITETURA

EMPREENDIMENTO	LOCAL	ETAPA
RESIDÊNCIA ANA PAULA	Rio Espera / MG	**PROJETO EXECUTIVO**

CONTEÚDO DA PRANCHA

QUADRO GERAL DE ESQUADRIAS E DETALHES TÍPICOS

DESENHO	RESPONSÁVEL TÉCNICO	REGISTRO PROFISSIONAL
KMZERO	Kleber Vieira Martins · Arquitetura	ART/RRT a emitir

REVISÃO	DATA	ESCALA	UNIDADE	CÓDIGO DA PRANCHA
R04	07/10/2026	1:5 / 1:10	metro (m)	**AP-ARQ-EX-016**

Direitos autorais reservados à KMZERO. Cliente: Ana Paula.