
PLANTA DE FORRO (TETO REFLETIDO) — TÉRREO

ESCALA 1:50 · nível do teto acima do piso acabado do térreo (±0,00) · cotas em metros · sem mobiliário

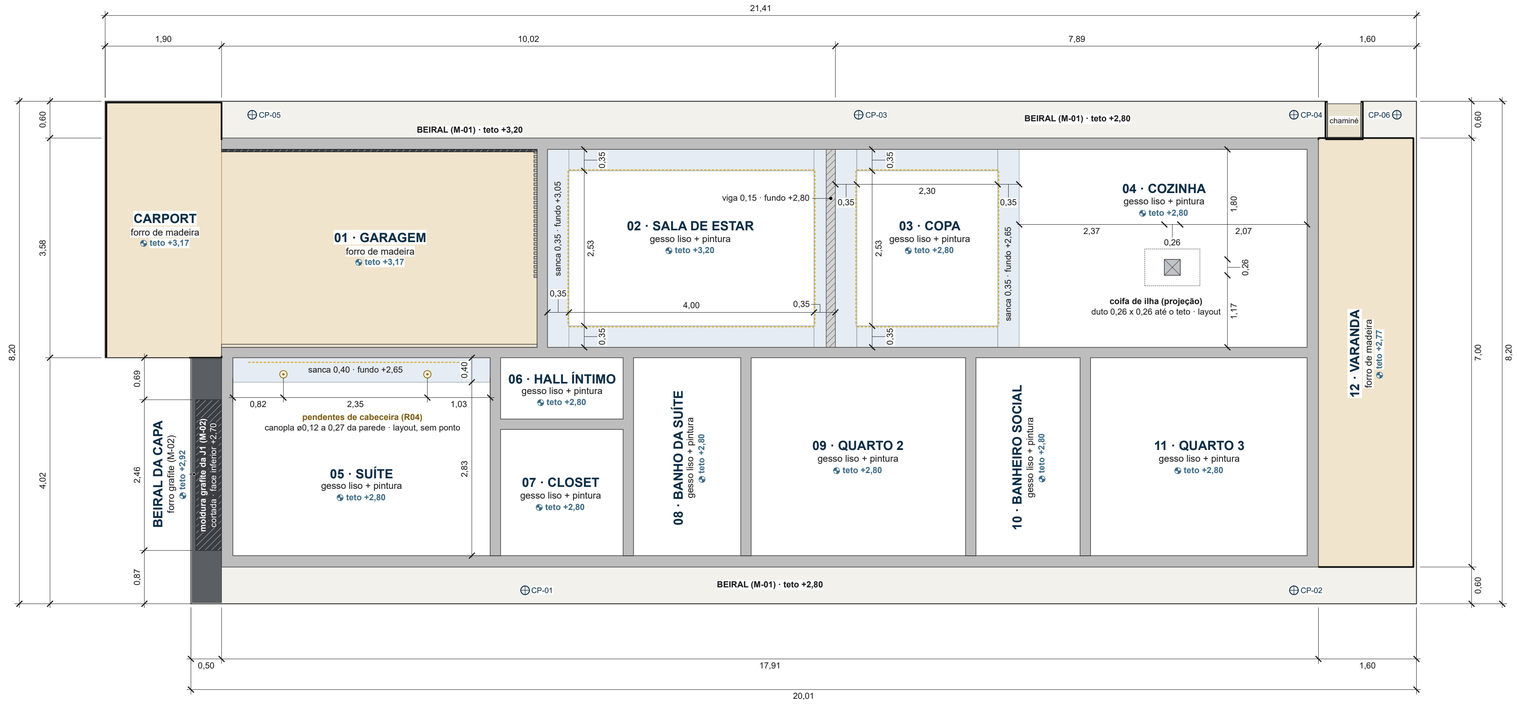

QUADRO DE FORROS E TETOS (Q09)

Nº	Ambiente	Tipo	Material e acabamento	Nível do teto	P.D. (m)	Área (m²)
01	Garagem	forro	forro de madeira (réguas a definir) sob a laje	+3,17	3,17	16,63
02	Sala de estar	laje + sanca	laje com gesso liso + pintura branca; sanca de gesso aberta de 0,35 com LED	+3,20; sanca +3,05	3,20	15,18
03	Copa	laje + sanca	laje com gesso liso + pintura branca; sanca de gesso aberta de 0,35 com LED	+2,80; sanca +2,65	2,80	9,69
04	Cozinha	laje	laje com gesso liso + pintura branca; projeção da coifa de ilha	+2,80	2,80	15,18
05	Suíte	laje + sanca	laje com gesso liso + pintura branca; sanca de gesso de 0,40 com LED na cabeceira	+2,80; sanca +2,65	2,80	13,57
06	Hall íntimo	laje	laje com gesso liso + pintura branca	+2,80	2,80	2,00
07	Closet	laje	laje com gesso liso + pintura branca	+2,80	2,80	4,12
08	Banho da suíte	laje	laje com gesso liso + pintura branca	+2,80	2,80	5,65
09	Quarto 2	laje	laje com gesso liso + pintura branca	+2,80	2,80	11,31
10	Banheiro social	laje	laje com gesso liso + pintura branca	+2,80	2,80	5,49
11	Quarto 3	laje	laje com gesso liso + pintura branca	+2,80	2,80	11,42
12	Varanda (coberta)	forro	forro de madeira (réguas a definir) sob a laje	+2,77	2,77	10,85
—	Carport (externo)	forro	forro de madeira (réguas a definir) sob a laje	+3,17	—	7,83
—	Beiral sul da capa da suíte	forro	forro grafite: pintura acrílica grafite (M-02), fora da moldura da J1	+2,92	—	0,87
—	Beirais da laje de cobertura	laje	face inferior da laje: textura acrílica branca (M-01)	+2,80 / +3,20	—	23,65
13	Quarto de hóspedes	laje	laje com gesso liso + pintura branca	+2,80 (-0,80)	2,80	10,78
14	Lavanderia	laje	laje com gesso liso + pintura branca	+2,80 (-0,80)	2,80	5,27
15	Banheiro	laje	laje com gesso liso + pintura branca	+2,80 (-0,80)	2,80	4,90
16	Gourmet / cozinha de roça	forro + vigas	forro de madeira (réguas a definir) entre vigas indicativas (fundos +2,90 e +2,95)	+3,37 (-0,23)	3,37	25,93

RESUMO DAS ÁREAS POR TIPO DE TETO (sem perdas)


Tipo de teto	Área (m²)
Laje com gesso liso + pintura branca (fora das sancas)	103,94
Sanca de gesso com LED (projeção)	10,61
Forro de madeira (garagem, carport, varanda e gourmet)	61,24
Forro grafite (beiral sul da capa da suíte)	0,87
Face inferior da laje nos beirais (M-01)	23,65


PENDÊNCIAS DA PLANTA DE FORRO (a definir)

1. Sanca norte da sala sobrepõe 0,15 a viga de desnível sala/copa (fundo +2,80): definir o encontro.
2. Beirais do corpo baixo em concreto no modelo x textura acrílica branca (M-01) nas fachadas; réguas do forro de madeira (garagem/carport, varanda, gourmet) a definir (o arremate com perfil L de alumínio preto junto às vigas e aos beirais é padrão adotado em 11/10/2026).
3. Luminárias do modelo fora do JSON (lustre da copa, pendente do hall íntimo, pendentes de palha da gourmet, embutidos do carport): não desenhadas; confirmar.
4. Capa da suíte: a moldura grafite da J1 sobe até +2,94 e o forro grafite do beiral fica de +2,92 a +2,95 (sobreposição de 0,02 no modelo); área do forro sem a moldura; definir o encontro.
5. Sanca com fita de LED da copa: está no modelo, fora da decisão R02 ("sanca com LED na sala e na suíte"); confirmar com a cliente.

TETO REFLETIDO — SUBSOLO GOURMET (FASE 2)

ESCALA 1:50 · nível do teto acima do piso do subsolo gourmet (-3,60); entre parênteses, o nível do projeto

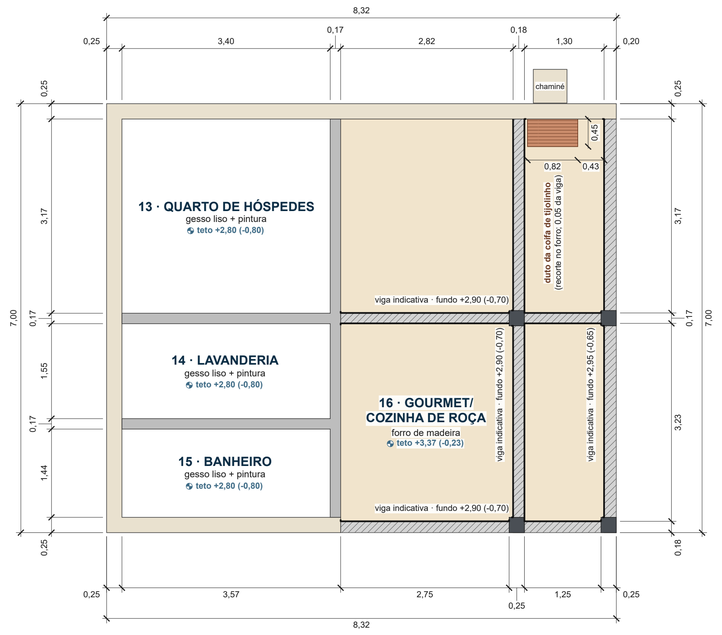

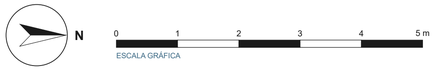

LEGENDA

- Laje com gesso liso + pintura branca (teto sem forro, Q03)
- Forro de madeira (réguas, sentido e fixação a definir)
- Sanca de gesso (largura e fundo indicados)
- Fita de LED da sanca (layout; sem ponto nem circuito)
- Forro grafite: pintura acrílica grafite (M-02)
- Beiral: face inferior da laje, textura acrílica branca (M-01)
- Viga aparente (fundo indicado); no subsolo, indicativa (estrutural)
- Pilar indicativo (projeto estrutural)
- Parede cortada acima das portas e janelas
- Pedra cortada (revestimento da garagem, paredes do subsolo gourmet, chaminé)
- Grafite cortado (M-02): moldura da janela da capa da suíte, revestimento da garagem
- Projeção da coifa de ilha e duto até o teto (layout)
- Duto da coifa de tijolinho: recorte no forro
- Perfil L de alumínio preto: forro de madeira junto às vigas e aos beirais; rufo da chaminé
- Pendente decorativo do JSON (R04): canopla, layout
- Condutor pluvial ø100 no beiral: referência, ver EX-003
- Nível do teto acima do piso acabado do pavimento
- Borda da laje de cobertura (vista de baixo)

NOTAS E HIPÓTESES

1. Planta de teto refletido: o teto visto de baixo, com a mesma orientação das plantas EX-001 e EX-002 (norte à direita). Paredes cortadas acima das portas e janelas, em cinza cheio; sem mobiliário.
2. Nível do teto em metros acima do piso acabado do pavimento (térreo ±0,00; subsolo gourmet -3,60), igual ao P.D. do quadro Q01 das EX-001/EX-002 e dos cortes EX-004 a EX-006; no subsolo gourmet, entre parênteses, o nível do projeto (±0,00 = piso acabado do térreo).
3. Sem forro: laje com gesso liso + pintura branca (Q03). Sancas de gesso com fita de LED na sala e na suíte (decisão R02) e na copa (só no modelo: ver pendências); o LED é só layout, sem ponto, circuito nem comando (elétrico por terceiros). Tabicas e arremates do gesso: não definidos no modelo (a definir).
4. Forro de madeira (garagem e carport, varanda, gourmet): réguas, largura, sentido, fixação e acabamento a definir com a cliente/fornecedor (o modelo e o JSON não definem); arremate com perfil L de alumínio preto junto às vigas e aos beirais (linha preta grossa; padrão usual adotado em 11/10/2026, reversível).
5. Vigas e pilares do subsolo gourmet indicativos (projeto estrutural, terceiros): o forro de madeira arremata nas faces das vigas com o perfil L; área do forro sem as vigas, os pilares e o duto da coifa de tijolinho, que fica afastado 0,05 da viga (padrão usual adotado em 11/10/2026; compatibilizar com o projeto estrutural).
6. Beirais: face inferior da laje de cobertura em textura acrílica branca (M-01 das fachadas), a +2,80 e a +3,20, e a faixa de 0,02 da laje da capa (+2,95) em volta do forro grafite; área sem a chaminé de pedra (beiral oeste da varanda), com recorte do beiral, rufo em volta da pedra e contra-rufo embutido nela (padrão usual; EX-003). Beiral sul da capa: forro grafite (M-02), fora da moldura da J1 (face inferior +2,70).
7. Luminária desenhada só a definida no JSON como peça de arquitetura: pendentes de cabeceira da suíte (R04), como layout (fita de LED das sancas: nota 3). Coifa de ilha da cozinha em projeção (layout; exaustão por terceiros).
8. Sem alçapão no forro (não existe no modelo). Condutores pluviais aparentes que passam pelos beirais (CP-01 a CP-06): só referência, ver EX-003.
9. Somente arquitetura: sem pontos elétricos, luminárias de instalação ou outros itens de instalações (projetos complementares, terceiros). Áreas medidas no modelo, sem perdas.

REV.	DATA	DESCRIÇÃO	POR
R04	**08/10/2026**	**Emissão do executivo (Cleber): cotas 2 casas, cobertura EX-003, caixa 1 x 3.000 L e porta PC1**	**KMZERO**
R04	07/10/2026	Revisão 4 (Ana Paula): ilha clara, banheiros e pendentes da suíte	KMZERO
R03	07/10/2026	Revisão 3 (Cleber): entrada pela sala, cozinha nos fundos com a varanda	KMZERO
R02	06/10/2026	Revisão 2 (Cleber): varanda 1,50, subsolo gourmet aterrado, gourmet nos fundos, portas, interiores	KMZERO
R01	06/10/2026	Revisão 1 (Cleber): recuos 1,50, cozinha em U, piso +0,15, cobertura, subsolo gourmet	KMZERO
R00	29/09/2026	Emissão inicial — estudo preliminar	KMZERO

KMZERO | ENGENHARIA · ARQUITETURA

EMPREENDIMENTO	LOCAL	ETAPA
RESIDÊNCIA ANA PAULA	Rio Espera / MG	**PROJETO EXECUTIVO**

CONTEÚDO DA PRANCHA

PLANTA DE FORRO — TÉRREO E SUBSOLO GOURMET

DESENHO	RESPONSÁVEL TÉCNICO	REGISTRO PROFISSIONAL
KMZERO	Kleber Vieira Martins · Arquitetura	ART/RRT a emitir

REVISÃO	DATA	ESCALA	UNIDADE	CÓDIGO DA PRANCHA
R04	07/10/2026	1:50	metro (m)	**AP-ARQ-EX-019**

Direitos autorais reservados à KMZERO. Cliente: Ana Paula.

AVISO: Projeto executivo de ARQUITETURA (somente arquitetura). Implantação, aterro e arrimos dependem do levantamento planialtimétrico; estrutura, contenção e instalações ficam com os projetos complementares (terceiros).