

PLANTA DA ESCADA LATERAL

ESCALA 1:25 · vista de cima · degraus numerados no sentido da subida · cotas em metros · níveis em relação ao piso acabado do térreo (±0,00)

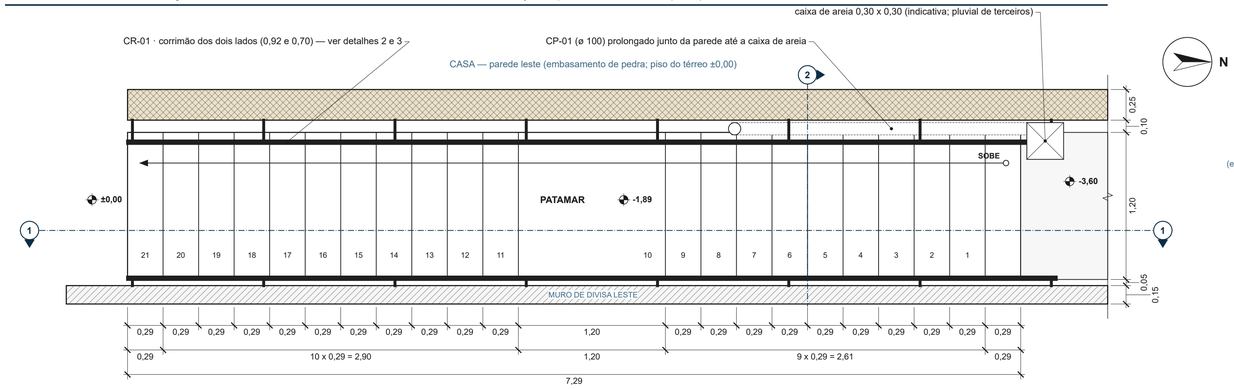


CORTE 1 — LONGITUDINAL DA ESCADA

ESCALA 1:25 · plano no eixo da escada, vista para leste · corrimão e muro em vista

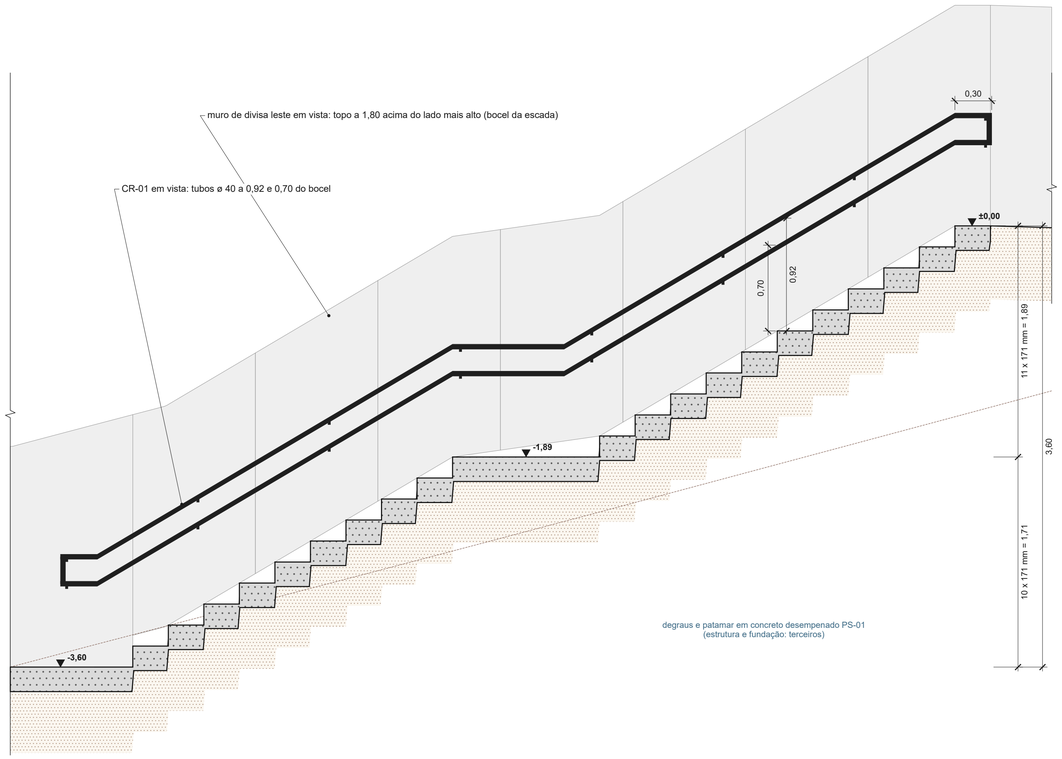


2 SEÇÃO TRANSVERSAL NO BOCEL (CORRIMÃOS)

ESCALA 1:10 · no espelho 6, vista para o norte (descida)

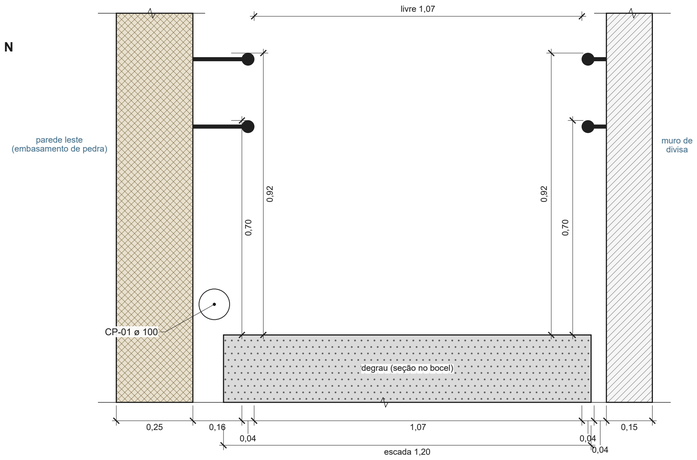


3 EXTREMIDADE DO CORRIMÃO (TOPO)

ESCALA 1:10 · vista para leste

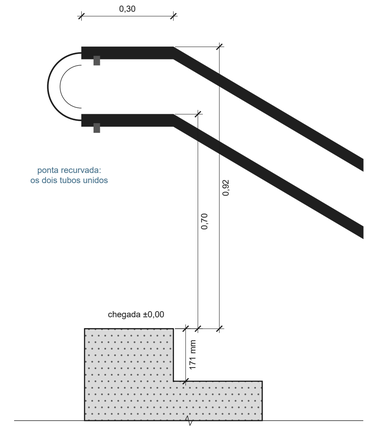


4 GC-01 — SEÇÃO NA BORDA DA VARANDA

ESCALA 1:10 · vista para leste

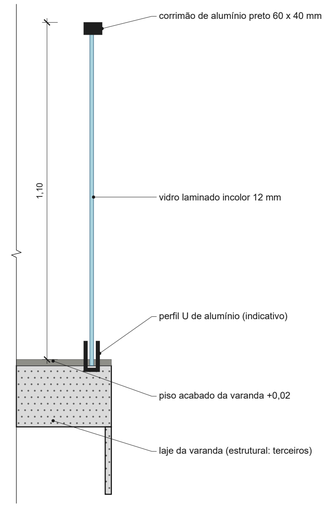


5 GC-02 — SEÇÃO NO ARRIMO NORTE

ESCALA 1:10 · área da piscina, vista para leste

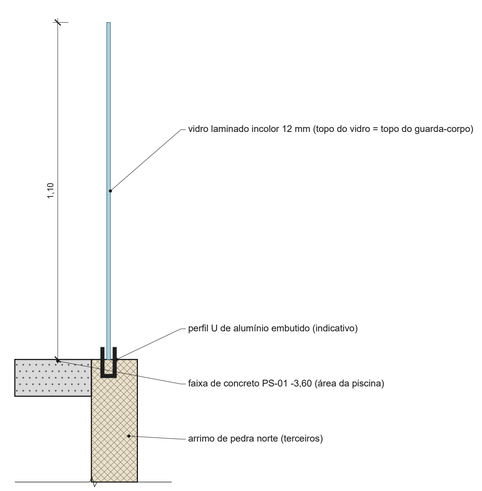


6 GC-01 — VISTA NORTE (VARANDA)

ESCALA 1:50 · olhando para o sul

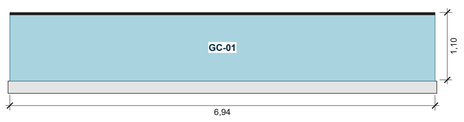

7 GC-02 — VISTA NORTE (ÁREA DA PISCINA)

ESCALA 1:50 · olhando para o sul

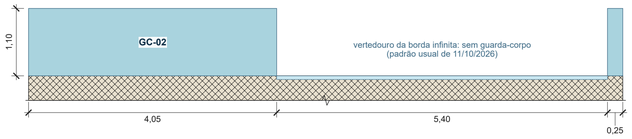

LEGENDA

- Concreto cortado (degraus, patamar, lajes, faixas)
- Pedra cortada (embasamento da casa, arrimo)
- Alvenaria cortada (muro de divisa)
- Alumínio preto (corrimãos, perfis, suportes)
- Vidro laminado incolor
- Elemento em vista, além do plano
- Terreno acabado (linha cheia) e natural (tracejada)

0 0,5 1 1,5 2 m — 1:25 — ESCALA GRÁFICA

0 0,25 0,5 m — 1:10 — ESCALA GRÁFICA

NOTAS E HIPÓTESES

1. Somente arquitetura. Metros com 2 casas; espelhos, tubos e vidros em mm. Níveis em relação ao piso acabado do térreo (±0,00). Ver também EX-006 (corte CC), EX-009 (fachada leste), EX-004/005 e EX-017/018.
2. Escada lateral (fase 2): 21 espelhos de 171 mm e pisos de 0,29 (2E + P = 0,63), em 2 lances (11 + 10) com patamar de 1,20 em -1,89; largura de 1,20; concreto desempenado PS-01. Sinalização visual na borda dos pisos (NBR 9050): a definir com a cliente.
3. CR-01 (tubo de alumínio ø 40 mm com pintura eletrostática preta; suportes de alumínio a cada 1,20 no máximo, fixados na parede leste da casa e no muro de divisa): a 0,92 e 0,70 do bocel, na vertical, até a geratriz superior; prolongamento horizontal de 0,30 nas pontas, que são recurvadas; 0,04 do muro e 0,16 da parede leste (folga do CP-01); livre entre corrimãos 1,07 (padrão de 09/10/2026, NBR 9050:2020, 6.9).
4. GC-01 e GC-02: 1,10 no mínimo acima do piso acabado (NBR 14718), vidro laminado (NBR 7199). O GC-02 fica nos trechos laterais; o vertedouro da borda infinita fica sem guarda-corpo (padrão usual de 11/10/2026).
5. CP-01 prolongado até a caixa de areia de 0,30 x 0,30 no pé da escada: indicativo (pluvial de terceiros, EX-003).
6. Fixação dos perfis U e dos suportes do corrimão: indicativa. O fornecedor dimensiona; a borda da laje, o muro e a base da escada ficam com o projeto estrutural (terceiros).
7. Iluminação da escada (balizadores ou arandelas): fora do escopo de arquitetura (projeto elétrico de terceiros).

QUADRO DA ESCADA LATERAL (Q10)

Item	Valor
Espelhos	21 x 171 mm (11 + 10 por lance, de cima para baixo)
Piso (profundidade)	0,29
2E + P	0,63 (NBR 9050: 0,63 a 0,65)
Patamar	1,20 x 1,20, nível -1,89
Largura da escada	1,20 (livre entre corrimãos 1,07)
Desnível vencido	3,60 (±0,00 a -3,60)
Comprimento em planta	7,29
Piso dos degraus	concreto desempenado PS-01 (fase 2)
Corrimão	CR-01 dos dois lados, a 0,92 e 0,70 do bocel

QUADRO DE GUARDA-CORPOS E CORRIMÃOS (Q11)

Cód.	Elemento	Altura	Extensão	Material	Norma
CR-01	Corrimão duplo da escada lateral (dos dois lados)	0,92 e 0,70 (bocel)	2 x 7,60 (em planta)	tubo de alumínio ø 40 mm, pintura eletrostática preta; suportes a cada 1,20 no máximo	NBR 9050:2020, 6.9
GC-01	Guarda-corpo da varanda	1,10 (piso acabado)	6,94 + 1,43 + 1,43	vidro laminado 12 mm (6 + 6) em perfil U de alumínio; corrimão de alumínio preto 60 x 40 mm	NBR 14718 e NBR 7199
GC-02	Guarda-corpo da área da piscina (trechos laterais do vertedouro)	1,10 (piso acabado)	4,05 + 0,25	vidro laminado 12 mm (6 + 6) em perfil U de alumínio embutido no piso	NBR 14718 e NBR 7199

AVISO: Projeto executivo de ARQUITETURA (somente arquitetura). Implantação, aterro e arrimos dependem do levantamento planialtimétrico; estrutura, contenção e instalações ficam com os projetos complementares (terceiros).

REV.	DATA	DESCRIÇÃO	POR
R04	**08/10/2026**	**Emissão do executivo (Cleber): cotas 2 casas, cobertura EX-003, caixa 1 x 3.000 L e porta PC1**	**KMZERO**
R04	07/10/2026	Revisão 4 (Ana Paula): ilha clara, banheiros e pendentes da suíte	KMZERO
R03	07/10/2026	Revisão 3 (Cleber): entrada pela sala, cozinha nos fundos com a varanda	KMZERO
R02	06/10/2026	Revisão 2 (Cleber): varanda 1,50, subsolo gourmet aterrado, gourmet nos fundos, portas, interiores	KMZERO
R01	06/10/2026	Revisão 1 (Cleber): recuos 1,50, cozinha em U, piso +0,15, cobertura, subsolo gourmet	KMZERO
R00	29/09/2026	Emissão inicial — estudo preliminar	KMZERO

KMZERO | ENGENHARIA · ARQUITETURA

EMPREENDIMENTO	LOCAL	ETAPA
RESIDÊNCIA ANA PAULA	Rio Espera / MG	**PROJETO EXECUTIVO**

CONTEÚDO DA PRANCHA

ESCADA LATERAL E GUARDA-CORPOS

DESENHO	RESPONSÁVEL TÉCNICO	REGISTRO PROFISSIONAL
KMZERO	Kleber Vieira Martins · Arquitetura	ART/RRT a emitir

REVISÃO	DATA	ESCALA	UNIDADE	CÓDIGO DA PRANCHA
R04	07/10/2026	1:25 / 1:10 / 1:50	metro (m)	**AP-ARQ-EX-020**

Direitos autorais reservados à KMZERO. Cliente: Ana Paula.