
IMPLANTAÇÃO E SITUAÇÃO

ESCALA 1:150 · norte para cima · cotas de nível em metros

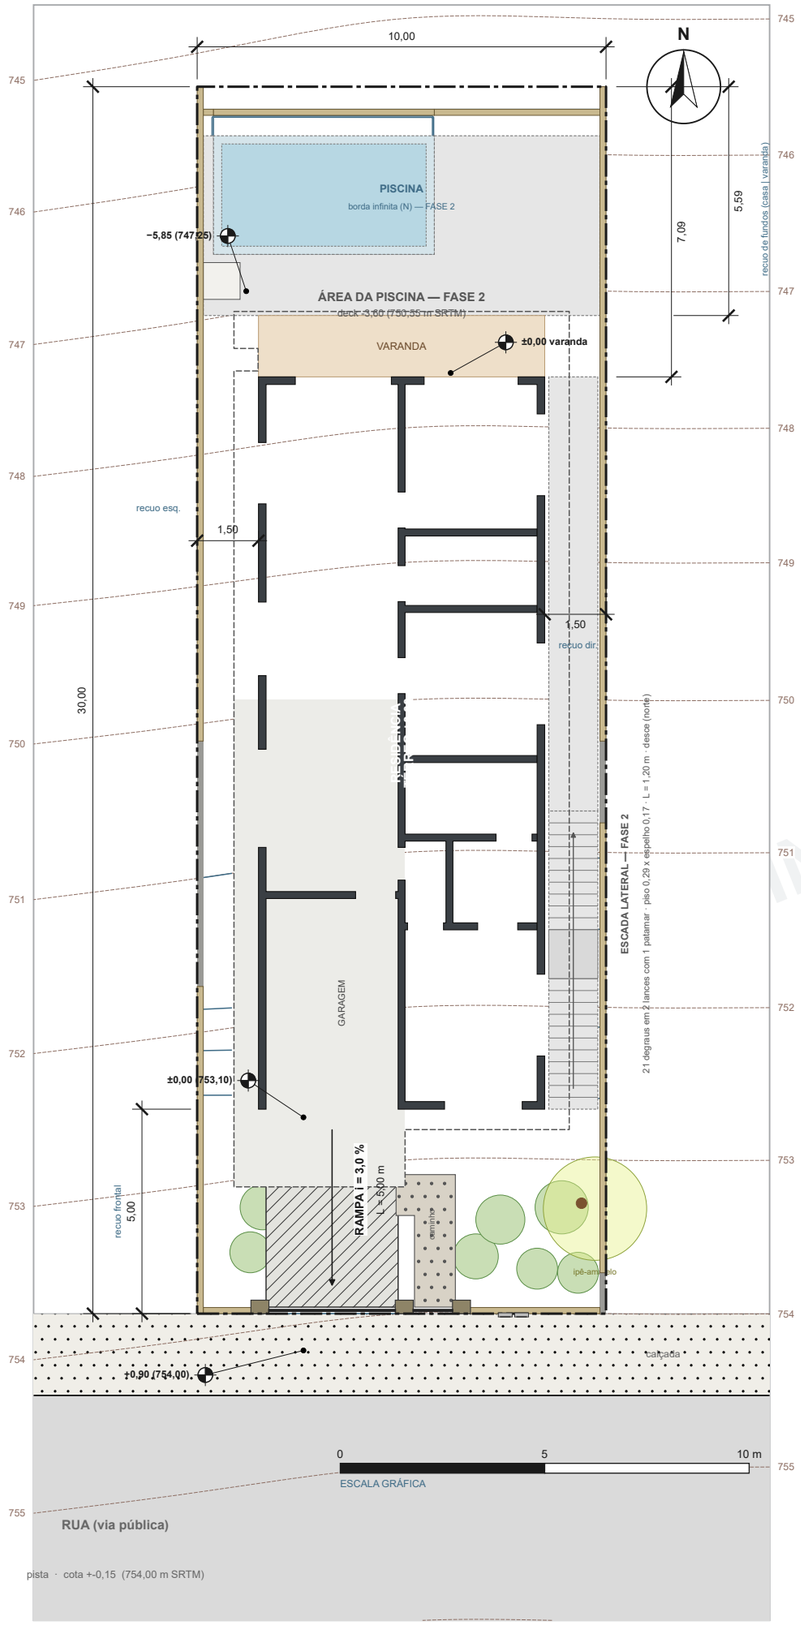

QUADRO DE DADOS DO LOTE E DA EDIFICAÇÃO

Parâmetro	Valor (calculado do modelo)
Terreno (lote 03, quadra 03, compromisso C/V)	10,00 x 30,00 m = 300,00 m²
Área construída coberta (fase 1)	149,80 m² (casa 125,34 + carport 13,96 + varanda 10,50)
Projeção da cobertura	169,58 m² (com beirais, capa da suíte e laje da varanda)
Taxa de ocupação	56,5 % (projeção / lote)
Coef. de aproveitamento	0,50 (área construída / lote; 1 pavimento)
Permeabilidade estimada — fase 1	111,10 m² = 37,0 % (jardim/gramado)
Permeabilidade estimada — fases 1+2	46,98 m² = 15,7 % (deck, piscina e escada impermeáveis)
Recuos (frontal | esq. | dir.)	5,00 | 1,50 | 1,50 m (frontal: carport avança 1,90 m)
Recuo de fundos (casa | varanda)	7,09 | 5,59 m
Altura da edificação	castelo da caixa d'água +6,25 m acima do piso (térreo + subsolo gourmet, fase 2)
Declividade natural do terreno	28,0 % para o norte (SRTM 30 m)
Rampa da garagem	3,0 % subindo da rua (piso 0,15 acima da rua; limite 20 %)
Vaga de garagem	1 carro, vaga 2,50 x 5,00 m (garagem 3,23 x 5,15 m)
Subsolo gourmet (fase 2)	20,94 m² fechados + gourmet aberta

TABELA DE NÍVEIS (Q08)

Nível (Q08)	Relativo	Cota SRTM (m)	Observação
Rua (pista/calçada)	-0,15	754,00	entrada do lote
Piso acabado (garagem, casa, varanda)	±0,00	754,15	referência ±0,00
Forro do corpo baixo	+2,80	756,95	pé-direito 2,80 m
Forro do bloco alto (garagem + sala de estar)	+3,20	757,35	pé-direito 3,20 m
Topo da platibanda (corpo baixo)	+3,55	757,70	telhado embutido atrás
Topo da platibanda (bloco alto)	+3,95	758,10	
Castelo da caixa d'água (topo)	+6,25	760,40	1 x 3.000 L
Subsolo gourmet e piscina (fase 2)	-3,60	750,55	desnível de 3,60 m
Base da contenção (indicativa)	-5,01	749,14	projeto de contenção


AVISO — ESTUDO PRELIMINAR

Estudo preliminar: topografia SRTM (30 m) e lote do compromisso de C/V, sem levantamento; não serve para fundação, contenção, terraplenagem ou aprovação legal.

CROQUI DE SITUAÇÃO (sem escala)

lat. -20,8595924 · lon. -43,4811516


ponto GPS enviado tomado como centro do lote — auditar

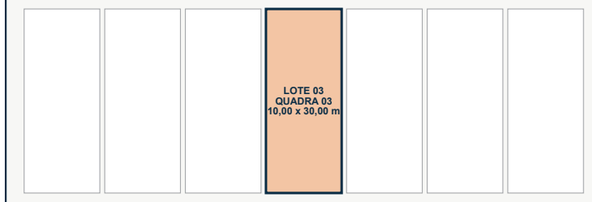

LEGENDA

- Curva de nível — terreno natural (a cada 1,00 m; cota SRTM)
- Curva de nível — terreno acabado (regrade do projeto)
- Limite do lote (compromisso C/V)
- Projeção da cobertura (carport, capa, varanda)
- Paredes do térreo
- Pedra: muro da frente, pilares e arrimos
- FASE 2 — subsolo gourmet, deck, piscina, escada
- Rampa da garagem (concreto desativado)
- Caminho de pedestres (piso intertravado)

PERFIL ESQUEMÁTICO DO LOTE — corte AA (PL-004), escala 1:200

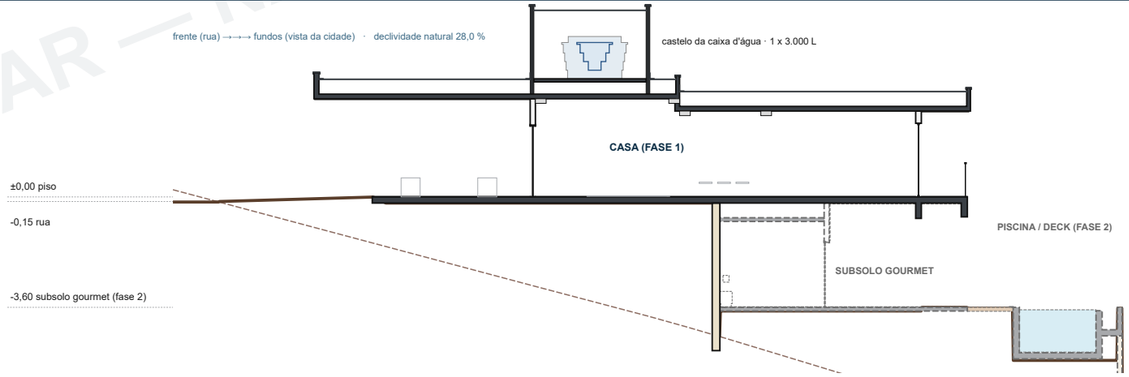

REV.	DATA	DESCRIÇÃO	POR
R04	**08/10/2026**	**Emissão do executivo (Cleber): cotas 2 casas, cobertura EX-003, caixa 1 x 3.000 L e porta PC1**	**KMZERO**
R04	07/10/2026	Revisão 4 (Ana Paula): ilha clara, banheiros e pendentes da suíte	KMZERO
R03	07/10/2026	Revisão 3 (Cleber): entrada pela sala, cozinha nos fundos com a varanda	KMZERO
R02	06/10/2026	Revisão 2 (Cleber): varanda 1,50, subsolo gourmet aterrado, gourmet nos fundos, portas, interiores	KMZERO
R01	06/10/2026	Revisão 1 (Cleber): recuos 1,50, cozinha em U, piso +0,15, cobertura, subsolo gourmet	KMZERO
R00	29/09/2026	Emissão inicial — estudo preliminar	KMZERO

KMZERO | ENGENHARIA · ARQUITETURA

EMPREENDIMENTO	LOCAL	ETAPA
RESIDÊNCIA ANA PAULA	Rio Espera / MG	**ESTUDO PRELIMINAR**

CONTEÚDO DA PRANCHA

IMPLANTAÇÃO E SITUAÇÃO

DESENHO	RESPONSÁVEL TÉCNICO	REGISTRO PROFISSIONAL
KMZERO	Kleber Vieira Martins · Arquitetura	sem ART/RRT — estudo preliminar

REVISÃO	DATA	ESCALA	UNIDADE	CÓDIGO DA PRANCHA
R04	07/10/2026	1:150	metro (m)	**AP-ARQ-PL-001**

Direitos autorais reservados à KMZERO. Cliente: Ana Paula.