
PLANTA BAIXA — TÉRREO

ESCALA 1:75 · cortada a 1,20 m acima do piso acabado

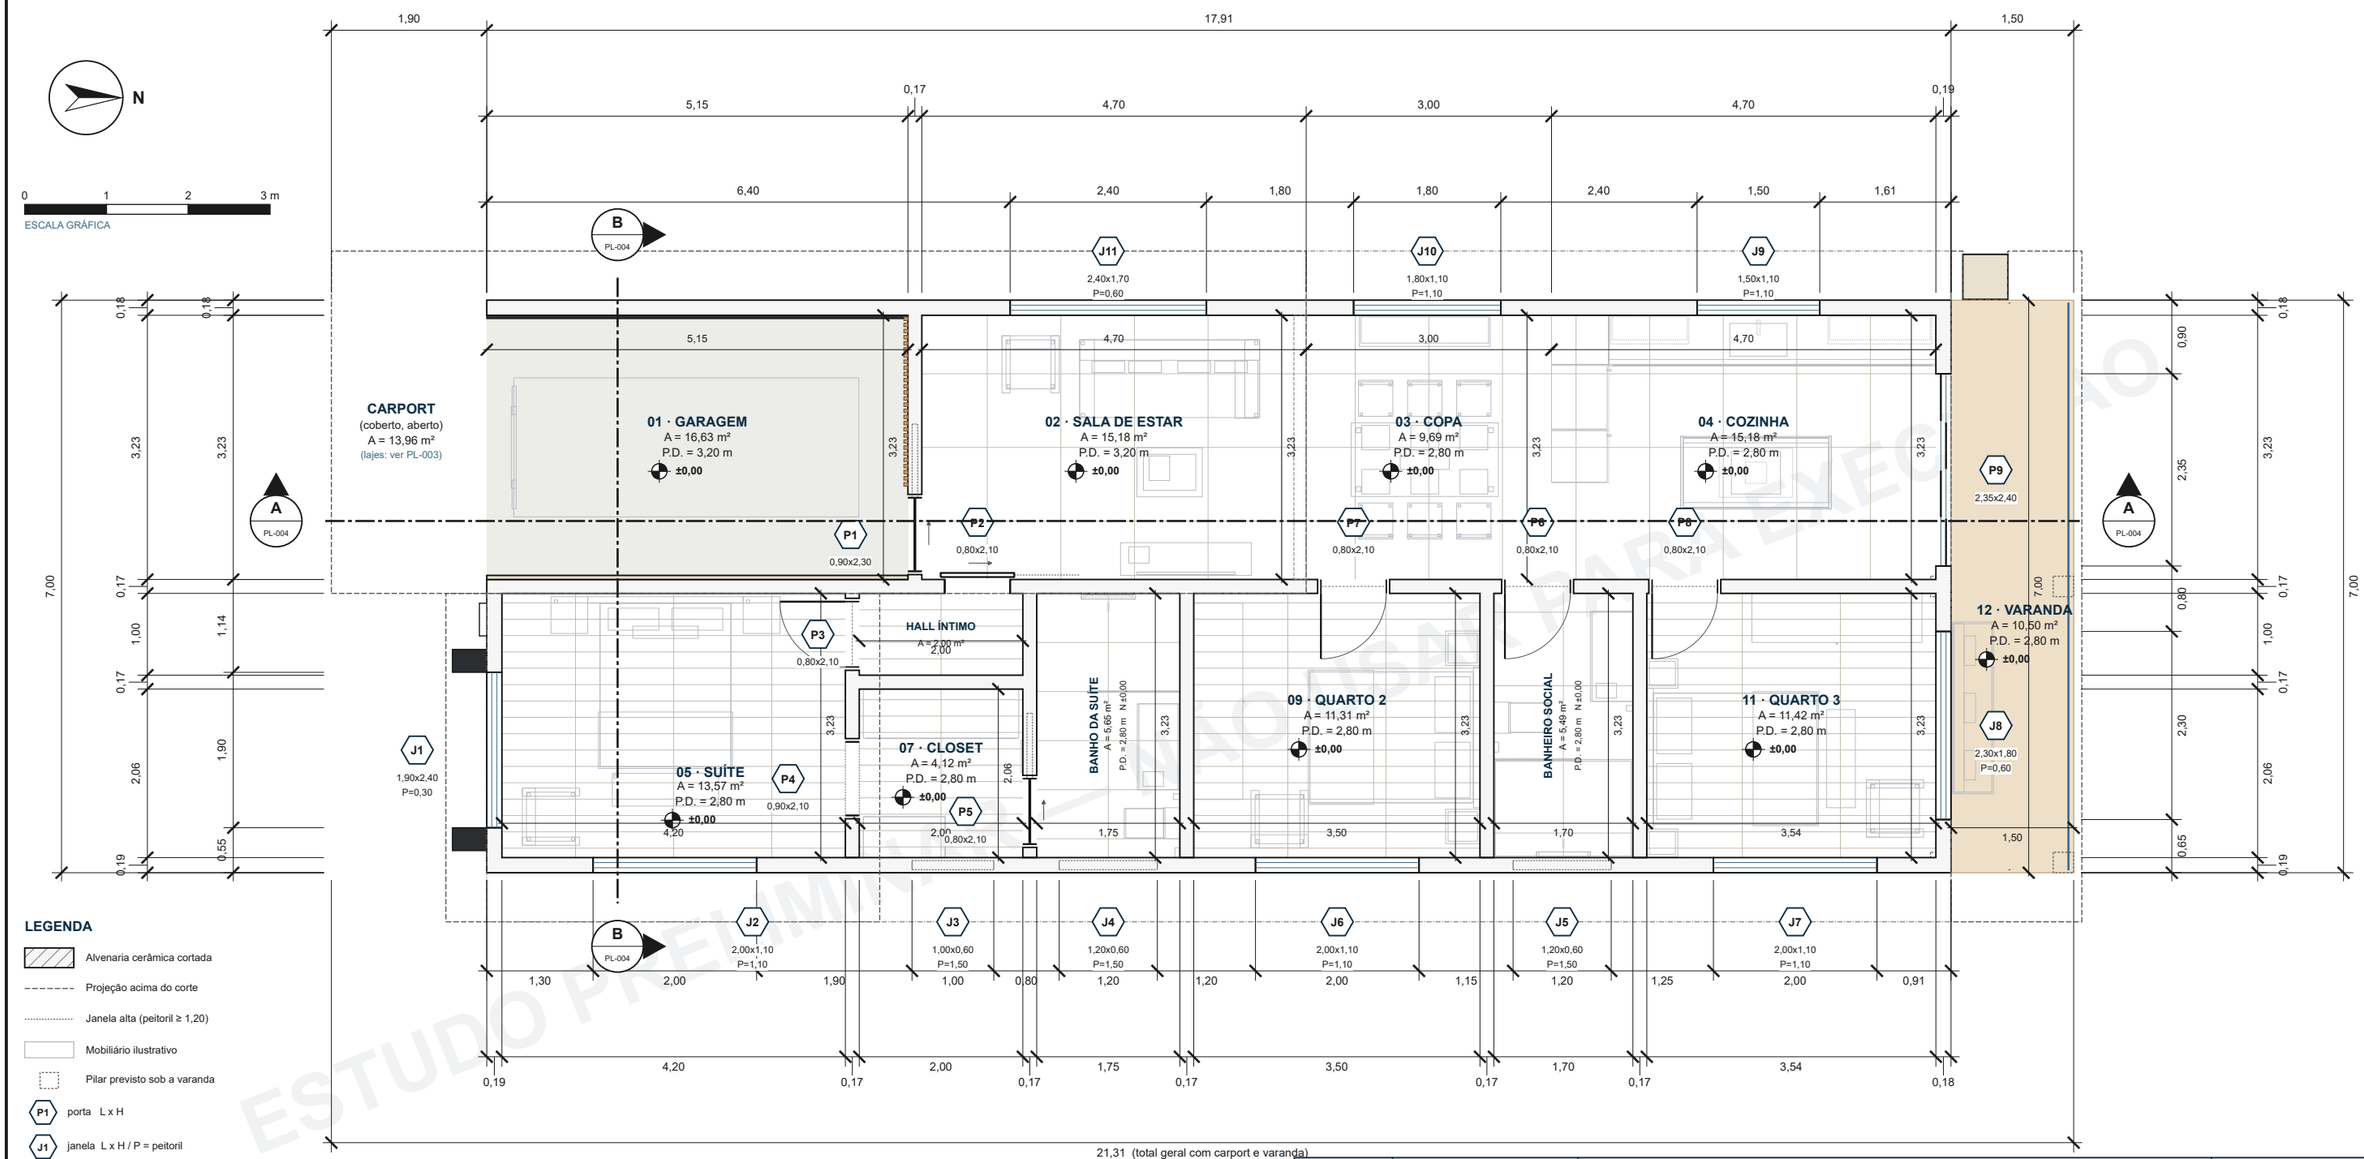

LEGENDA

- Alvenaria cerâmica cortada
- Projeção acima do corte
- Janela alta (peitoril ≥ 1,20)
- Mobiliário ilustrativo
- Pilar previsto sob a varanda
- P1 — porta L x H
- J1 — janela L x H / P = peitoril
- ±0,00 = 754,15 m SRTM
- Beiral (projeção da laje)
- Paginação do piso (juntas)

QUADRO DE AMBIENTES (Q01)

Nº	Ambiente	Área (m²)	P.D. (m)	Piso	Nível
01	Garagem	16,63	3,20	concreto desempenado	±0,00
02	Sala de estar	15,18	3,20	Porcel. marmorizado 90 x 90 polido	±0,00
03	Copa	9,69	2,80	Porcel. marmorizado 90 x 90 polido	±0,00
04	Cozinha	15,18	2,80	Porcel. marmorizado 90 x 90 polido	±0,00
05	Suíte	13,57	2,80	Porcel. amadeirado 20 x 120	±0,00
06	Hall íntimo	2,00	2,80	Porcel. amadeirado 20 x 120	±0,00
07	Closet	4,12	2,80	Porcel. amadeirado 20 x 120	±0,00
08	Banho da suíte	5,65	2,80	Porcel. travertino 60 x 120	±0,00
09	Quarto 2	11,31	2,80	Porcel. amadeirado 20 x 120	±0,00
10	Banheiro social	5,49	2,80	Porcel. marmorizado 90 x 90 polido	±0,00
11	Quarto 3	11,42	2,80	Porcel. amadeirado 20 x 120	±0,00
12	Varanda (coberta)	10,50	2,80	deck de madeira	±0,00
	ÁREA INTERNA DOS AMBIENTES (01-11)	110,24			

QUADRO DE ÁREAS (Q05)

Descrição	Área (m²)	% lote
Terreno (lote 03, quadra 03: 10,00 x 30,00 m)	300,00	100,00
Área interna útil (ambientes 01-11)	110,24	36,7
Paredes (P-02 ext. / P-01 int.)	15,10	5,0
Casa: paredes ext. (7,00 x 17,91)	125,34	41,8
Carport (fora da casa)	13,96	4,7
Varanda coberta (7,00 x 1,50)	10,50	3,5
ÁREA CONSTRUÍDA COBERTA	149,80	49,9
Projeção da cobertura (com beirais)	169,58	56,5
Taxa de ocupação (projeção / lote)	56,5 %	

AVISO: Estudo preliminar: topografia SRTM (30 m) e lote do compromisso de C/V, sem levantamento; não serve para fundação, contenção, terraplenagem ou aprovação legal.

REV.	DATA	DESCRIÇÃO	POR
R04	**08/10/2026**	**Emissão do executivo (Cleber): cotas 2 casas, cobertura EX-003, caixa 1 x 3.000 L e porta PC1**	**KMZERO**
R04	07/10/2026	Revisão 4 (Ana Paula): ilha clara, banheiros e pendentes da suíte	KMZERO
R03	07/10/2026	Revisão 3 (Cleber): entrada pela sala, cozinha nos fundos com a varanda	KMZERO
R02	06/10/2026	Revisão 2 (Cleber): varanda 1,50, subsolo gourmet aterrado, gourmet nos fundos, portas, interiores	KMZERO
R01	06/10/2026	Revisão 1 (Cleber): recuos 1,50, cozinha em U, piso +0,15, cobertura, subsolo gourmet	KMZERO
R00	29/09/2026	Emissão inicial — estudo preliminar	KMZERO

KMZERO | ENGENHARIA · ARQUITETURA

EMPREENDIMENTO	LOCAL	ETAPA
RESIDÊNCIA ANA PAULA	Rio Espera / MG	**ESTUDO PRELIMINAR**

CONTEÚDO DA PRANCHA

PLANTA BAIXA DO TÉRREO

DESENHO	RESPONSÁVEL TÉCNICO	REGISTRO PROFISSIONAL
KMZERO	Kleber Vieira Martins · Arquitetura	sem ART/RRT — estudo preliminar

REVISÃO	DATA	ESCALA	UNIDADE	CÓDIGO DA PRANCHA
R04	07/10/2026	1:75	metro (m)	**AP-ARQ-PL-002**

Direitos autorais reservados à KMZERO. Cliente: Ana Paula.

ESTUDO PRELIMINAR