

PLANTA DE COBERTURA

ESCALA 1:75 · telhado embutido de fibrocimento 6 mm, i = 12 %, atrás da platibanda com rufo e calha

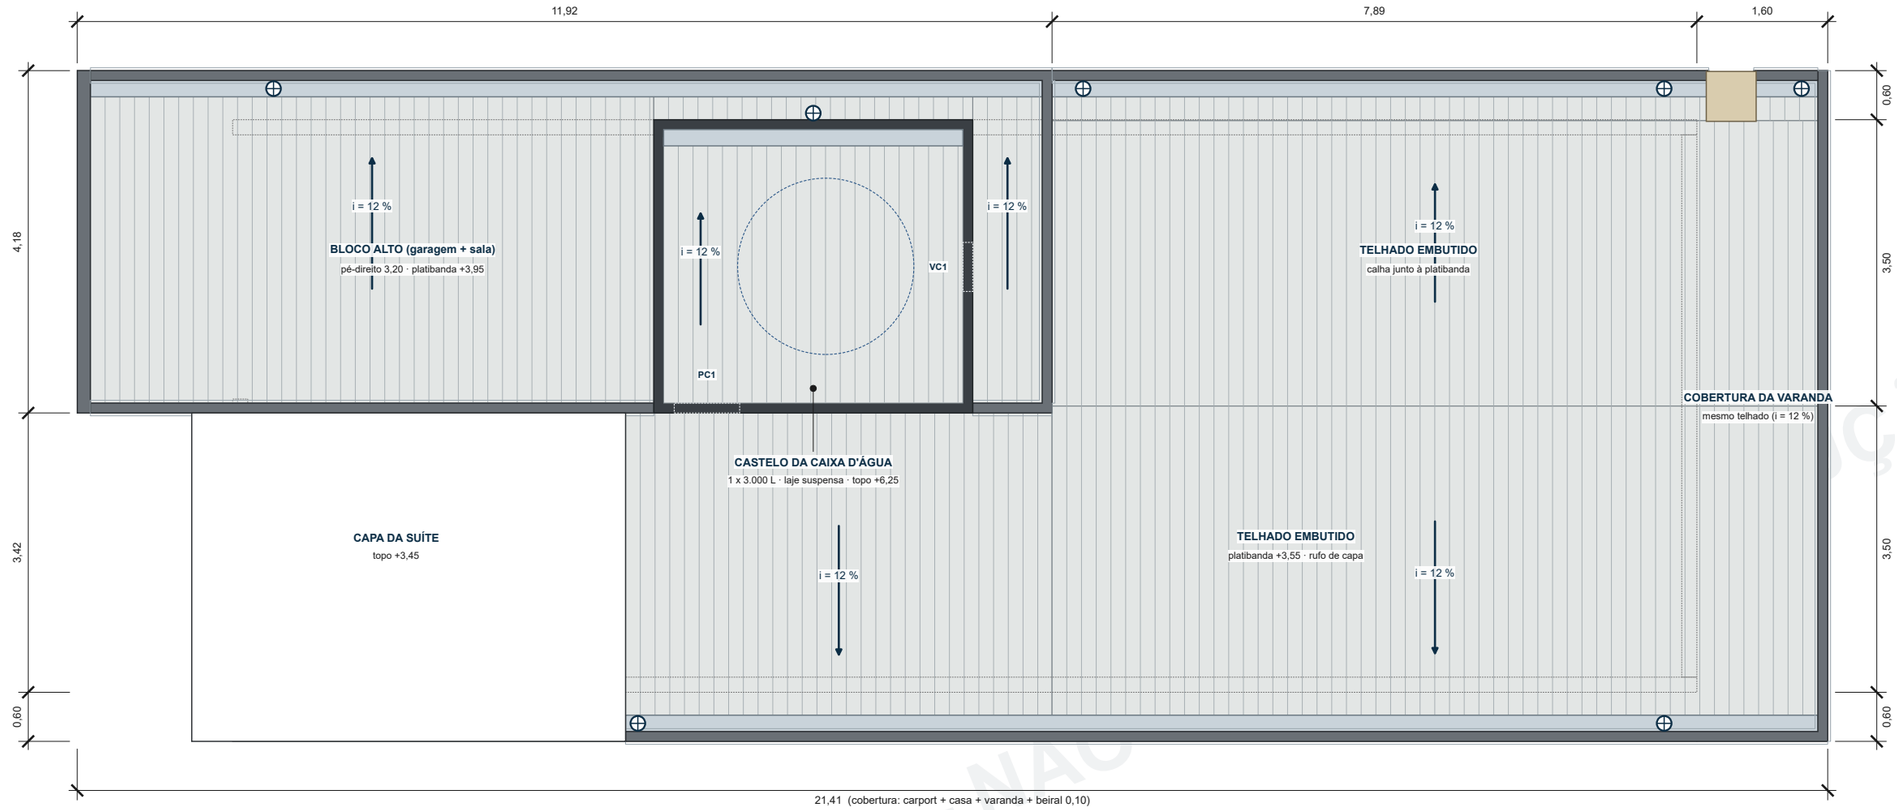

PLANTA DO SUBSOLO GOURMET E ÁREA DA PISCINA — FASE 2

ESCALA 1:100 · cortada a 1,20 m acima do piso do subsolo (-3,60); obra posterior

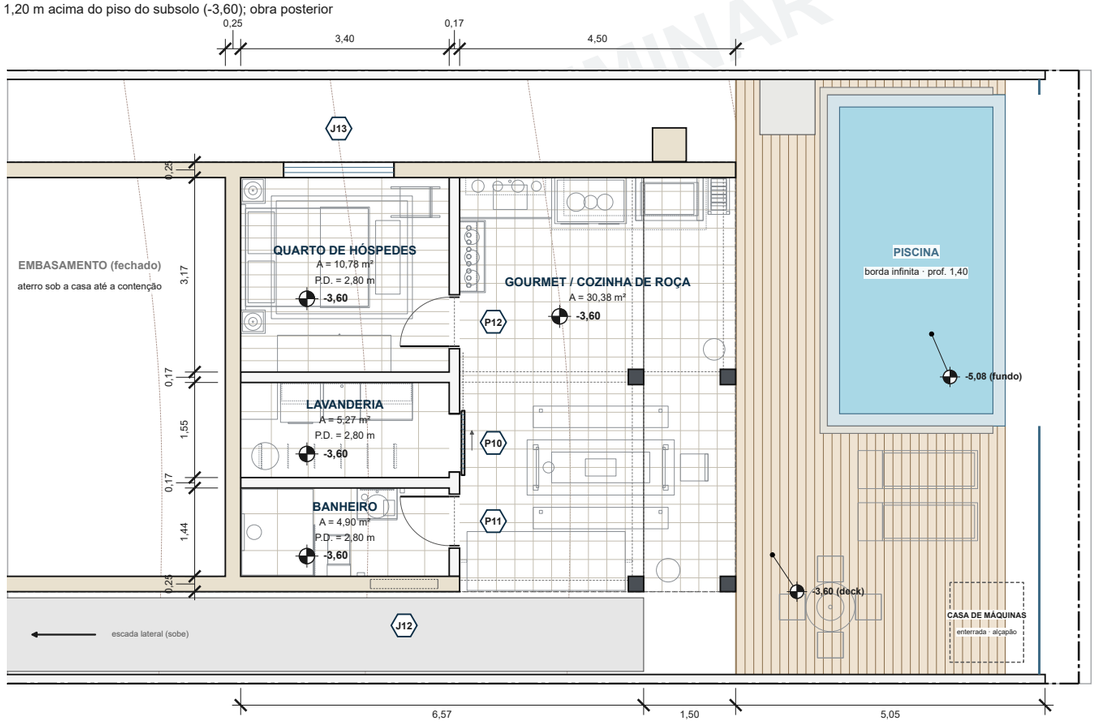

escala gráfica do subsolo gourmet (1:100)

0 1 2 3 4 5 m

ESCALA GRÁFICA

N

NOTAS E HIPÓTESES

1. Cobertura: fibrocimento 6 mm com i = 12 % em duas águas (cumeeira sobre a parede do meio), atrás de platibanda de 0,60 m com rufo de capa e pingadeira; calhas em U (20 x 10) junto às platibandas laterais, rufo de encosto no bloco alto e 6 condutores ø100 aparentes nas laterais (caixa de areia no pé).
2. Bloco alto (garagem + sala de estar) com pé-direito 3,20 e laje própria; sobre a sala de estar, castelo da caixa d'água (1 x 3.000 L, porta PC1 de metal vazado a leste, veneziana VC1 ao norte) com laje suspensa, platibanda e rufo de capa; telhado do castelo escondido, i = 12 % para oeste, com calha e descida na face oeste (para o telhado do bloco alto).
3. Beiral de 0,60 m em todo o perímetro sem outro detalhe; capa da suíte e laje do carport mantêm o desenho da R00.
4. Subsolo gourmet (FASE 2, sobre aterro, -3,60): quarto de hóspedes 10,78 m², lavanderia 5,27 m², banheiro 4,90 m², gourmet / cozinha de roça 30,38 m². Contenção a 6,57 m do fundo da casa; faixa da frente com 3,40 m; gourmet aberta com pé-direito 3,40; paredes externas em pedra até a laje do térreo; tijolinho e forro de madeira na gourmet.
5. Escada lateral: 21 degraus em 2 lances com 1 patamar (espelho 0,17, piso 0,29), do térreo ao subsolo gourmet (desnível 3,60 m).

REV.	DATA	DESCRIÇÃO	POR
R04	**08/10/2026**	**Emissão do executivo (Cleber): cotas 2 casas, cobertura EX-003, caixa 1 x 3.000 L e porta PC1**	**KMZERO**
R04	07/10/2026	Revisão 4 (Ana Paula): ilha clara, banheiros e pendentes da suíte	KMZERO
R03	07/10/2026	Revisão 3 (Cleber): entrada pela sala, cozinha nos fundos com a varanda	KMZERO
R02	06/10/2026	Revisão 2 (Cleber): varanda 1,50, subsolo gourmet aterrado, gourmet nos fundos, portas, interiores	KMZERO
R01	06/10/2026	Revisão 1 (Cleber): recuos 1,50, cozinha em U, piso +0,15, cobertura, subsolo gourmet	KMZERO
R00	29/09/2026	Emissão inicial — estudo preliminar	KMZERO

KMZERO | ENGENHARIA · ARQUITETURA

EMPREENDIMENTO	LOCAL	ETAPA
RESIDÊNCIA ANA PAULA	Rio Espera / MG	**ESTUDO PRELIMINAR**

CONTEÚDO DA PRANCHA

COBERTURA E SUBSOLO GOURMET (FASE 2)

DESENHO	RESPONSÁVEL TÉCNICO	REGISTRO PROFISSIONAL
KMZERO	Kleber Vieira Martins · Arquitetura	sem ART/RRT — estudo preliminar

REVISÃO	DATA	ESCALA	UNIDADE	CÓDIGO DA PRANCHA
R04	07/10/2026	1:75 e 1:100	metro (m)	**AP-ARQ-PL-003**

Direitos autorais reservados à KMZERO. Cliente: Ana Paula.

AVISO: Estudo preliminar: topografia SRTM (30 m) e lote do compromisso de C/V, sem levantamento; não serve para fundação, contenção, terraplenagem ou aprovação legal.