
## FACHADA LESTE (lado direito)

ESCALA 1:150 · observador a leste; frente à esquerda; muros de divisa e arrimos translúcidos

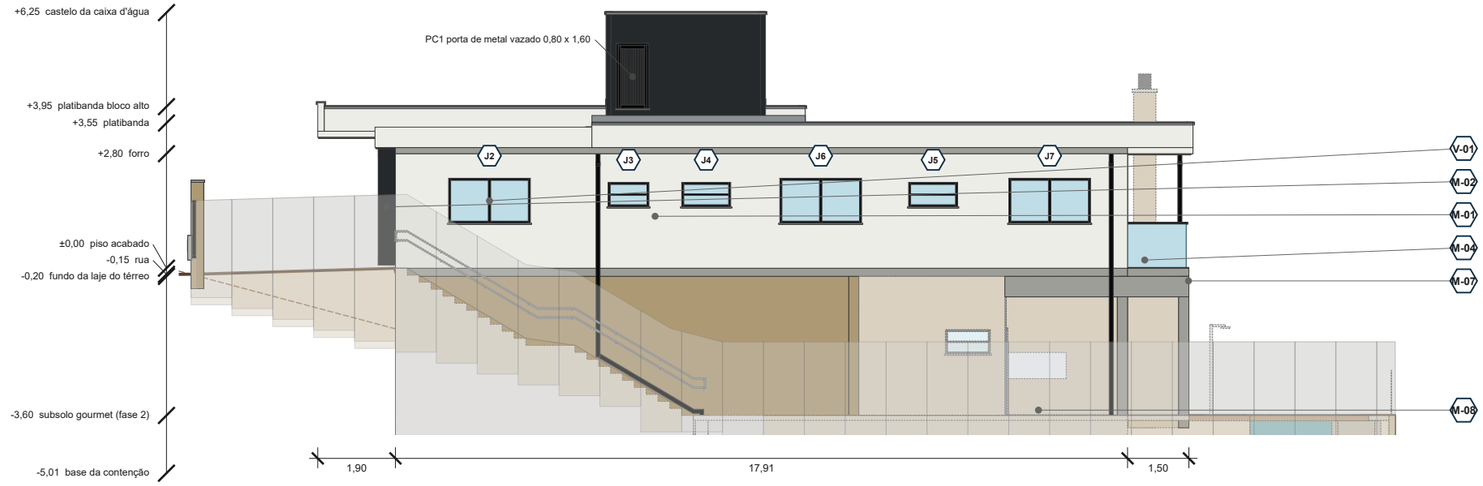


## FACHADA OESTE (lado esquerdo)

ESCALA 1:150 · observador a oeste; fundos à esquerda; recuo de 1,50 m com janelas baixas e peitoril de granito




## QUADRO DE ESQUADRIAS (Q02/Q03)

| Cód. | Descrição | L (m) | H (m) | Peit. (m) | Tipologia · material | Qtd. |
|---|---|---|---|---|---|---|
| P1 | Porta de entrada (correr embutida, para a sala) | 0,90 | 2,30 | 0,00 | correr embutida (kit na parede) · madeira maciça (freijó/imbuia, a definir) | 1 |
| P2 | Porta sala/hall da suíte (correr aparente) | 0,80 | 2,10 | 0,00 | correr aparente · madeira maciça · trilho preto aparente | 1 |
| P3 | Porta suíte (hall) | 0,80 | 2,10 | 0,00 | giro 1 folha · madeira semi-oca ou maciça (a definir) | 1 |
| P4 | Passagem suíte/closet | 0,90 | 2,10 | 0,00 | passagem livre (sem folha) · vão com guarnição de madeira | 1 |
| P5 | Porta banho da suíte (correr embutida) | 0,80 | 2,10 | 0,00 | correr embutida (kit na parede) · madeira maciça (freijó/imbuia, a definir) | 1 |
| P6 | Porta banheiro social | 0,80 | 2,10 | 0,00 | giro 1 folha · madeira semi-oca ou maciça (a definir) | 1 |
| P7 | Porta quarto 2 | 0,80 | 2,10 | 0,00 | giro 1 folha · madeira semi-oca ou maciça (a definir) | 1 |
| P8 | Porta quarto 3 | 0,80 | 2,10 | 0,00 | giro 1 folha · madeira semi-oca ou maciça (a definir) | 1 |
| P9 | Porta de correr de vidro (cozinha/varanda) | 2,35 | 2,40 | 0,00 | correr, folhas de vidro · vidro temperado incolor 8 mm + alumínio preto | 1 |
| J1 | Janela alta da suíte (fachada) | 1,90 | 2,40 | 0,30 | fixa (+ bandeira) · alumínio preto + vidro laminado 8 mm | 1 |
| J2 | Janela suíte | 2,00 | 1,10 | 1,10 | correr 2 folhas · alumínio preto + vidro incolor 6 mm · peitoril de granito | 1 |
| J3 | Janela closet | 1,00 | 0,60 | 1,50 | basculante · alumínio preto + vidro mini-boreal 4 mm · peitoril de granito | 1 |
| J4 | Janela banho suíte | 1,20 | 0,60 | 1,50 | maxim-ar · alumínio preto + vidro mini-boreal 4 mm · peitoril de granito | 1 |
| J5 | Janela banheiro social | 1,20 | 0,60 | 1,50 | maxim-ar · alumínio preto + vidro mini-boreal 4 mm · peitoril de granito | 1 |
| J6 | Janela quarto 2 | 2,00 | 1,10 | 1,10 | correr 2 folhas · alumínio preto + vidro incolor 6 mm · peitoril de granito | 1 |
| J7 | Janela quarto 3 (leste) | 2,00 | 1,10 | 1,10 | correr 2 folhas · alumínio preto + vidro incolor 6 mm · peitoril de granito | 1 |
| J8 | Janela quarto 3 (vista) | 2,30 | 1,80 | 0,60 | correr 2 folhas · alumínio preto + vidro laminado 8 mm · peitoril de granito | 1 |
| J9 | Janela cozinha (sobre a pia) | 1,50 | 1,10 | 1,10 | correr 2 folhas · alumínio preto + vidro incolor 6 mm · peitoril de granito | 1 |
| J10 | Janela copa | 1,80 | 1,10 | 1,10 | correr 2 folhas · alumínio preto + vidro incolor 6 mm · peitoril de granito | 1 |
| J11 | Janela sala | 2,40 | 1,70 | 0,60 | correr 2 folhas + fixo inferior · alumínio preto + vidro laminado 8 mm · peitoril de granitot | 1 |
| PC1 ** | Porta de acesso à caixa d'água | 0,80 | 1,60 | 0,05 (cast.) | giro, abre para fora · metal vazado (alumínio preto + tela inox) | 1 |
| VC1 ** | Veneziana de ventilação do castelo | 0,60 | 0,30 | 1,30 (cast.) | veneziana fixa · alumínio preto | 1 |
| P10 * | Porta lavanderia (correr veneziana) | 0,95 | 2,10 | 0,00 (inf.) | correr veneziana · madeira azul colonial · trilho preto | 1 |
| P11 * | Porta banheiro (inferior) | 0,80 | 2,10 | 0,00 (inf.) | giro 1 folha · madeira pintada azul colonial (gourmet de roça) | 1 |
| P12 * | Porta quarto de hóspedes | 0,80 | 2,10 | 0,00 (inf.) | giro 1 folha · madeira pintada azul colonial (gourmet de roça) | 1 |
| J12 * | Janela banheiro (inferior) | 1,10 | 0,60 | 1,50 (inf.) | maxim-ar · alumínio preto + vidro mini-boreal 4 mm · peitoril de granito | 1 |
| J13 * | Janela quarto de hóspedes | 1,80 | 1,20 | 1,00 (inf.) | correr 2 folhas · alumínio preto + vidro incolor 6 mm · peitoril de granito | 1 |

Fase 1: 10 portas + 12 janelas = 22 vãos (com as 2 do castelo). * subsolo gourmet (fase 2), peitoril medido do piso do subsolo (-3,60).

** castelo da caixa d'água (1 x 3.000 L): peitoril medido do piso do castelo (+3,85); PC1 abre para fora (leste), dobradiças no batente norte; detalhes no AP-ARQ-EX-003.

Portas: altura livre do vão; peitoril = distância do piso acabado (±0,00) à soleira da esquadria.

## LEGENDA DE MATERIAIS

- M-01 — Textura acrílica branca sobre emboço
- M-02 — Pintura acrílica grafite (moldura, frisos, forro da capa)
- M-04 — Pedra natural mineira (embasamento, contenção, pilares do portão, chaminé)
- M-05 — Painel ripado de madeira (garagem e forro do carport/varanda)
- M-06 — Cobogó — elemento vazado 20 x 20 x 9 cm
- M-07 — Concreto aparente / laje (pilares, arrimos e piscina)
- M-08 — Reboco cinza claro (muros de divisa, h = 1,80 m)
- V-01 — Vidro incolor/laminado (esquadrias e guarda-corpo)
- A-01 — Alumínio preto (caixilhos, gradil, portões, corrimão)
- D-01 — Deck de madeira (varanda e área da piscina)
- FASE 2 (subsolo gourmet, deck, piscina): cor esmaecida, traço tracejado

## DECISÕES DA R04 (casa_ana_paula.json)

1. Pedido da Ana Paula (foto de referência): ilha em cor clara. Tampo e laterais em cascata até o piso em porcelanato branco com veios cinza (efeito mármore), frentes no mesmo material; cooktop e coifa de ilha mantidos. A bancada da pia segue em granito cinza.
2. Pedido da Ana Paula: tom claro com acessórios dourados. Paredes em porcelanato branco com veios dourados até o teto, faixa de ripado de madeira entre a bancada e o box, nicho de madeira, deck de madeira no piso do box, piso marmorizado claro; torneira, chuveiro, perfil do box, papeleira, toalheiro e moldura do espelho dourados.
3. Ideia da KMZERO (a Ana Paula ainda não tinha ideia): banho "spa natural". Box em porcelanato travertino até o teto com nicho iluminado, piso em travertino 60 x 120, parede da bancada em verde-musgo, gabinete de madeira com tampo de travertino, espelho redondo com LED por trás e metais em dourado escovado.
4. Pedido da Ana Paula (foto de referência): pendentes de cabeceira com aro oval de cristal iluminado, haste e canopla douradas e cabo fino até o teto.
5. Pedido do Cleber: calha, rufo e descida à mostra e outra cobertura para a caixa d'água. Estudada a telha colonial a 35 %, ficou o fibrocimento, agora a 12 %, ainda escondido pela platibanda de 60 cm. Calhas em U de chapa galvanizada, rufo de capa com pingadeira, rufo de encosto no bloco alto, condutores ø100 em alumínio preto aparentes nas laterais com caixa de areia; castelo da caixa d'água sem o telhadinho, com platibanda, rufo, telhado escondido, calha e descida.
6. Escopo da KMZERO neste projeto: somente arquitetura. Estrutural, contenção, fundações, hidrossanitário e pluvial, elétrico, levantamento e sondagem ficam com terceiros; as posições de calhas, descidas, pilares e arrimos do modelo são indicativas.
7. Emissão do executivo (Cleber), 08/10/2026: cotas com 2 casas, fechando o total nas cadeias; cobertura executiva no AP-ARQ-EX-003 (condutores CP-01 a CP-07); caixa d'água 1 x 3.000 L no castelo de 3,59 × 3,90 m (topo +6,25), porta PC1 0,80 × 1,60 de metal vazado na face leste e veneziana VC1 0,60 × 0,30 ao norte.

**AVISO: Estudo preliminar: topografia SRTM (30 m) e lote do compromisso de C/V, sem levantamento; não serve para fundação, contenção, terraplenagem ou aprovação legal.**

## PENDÊNCIAS PARA A ETAPA SEGUINTE

1. Documento da compra do irmão (o compromisso está no nome do Tiago): recibo, contrato ou cessão
2. Escritura e matrícula individual (só após a conclusão do loteamento)
3. Croqui do loteamento (anexo do compromisso) e pin correto do lote 03, quadra 03
4. Pavimento e redes da Rua 02 no local (contrato prevê bloquete)
5. Código de Obras de Rio Espera: recuos, taxa de ocupação, permeabilidade, altura de muro
6. Cliente escolher porcelanato/acabamentos (loja Tau, em Rio Espera, citada por ela)
7. Validar com a cliente a R04: ilha clara, banheiros, pendentes da suíte e cobertura com calhas e descidas aparentes (entrada pela sala, varanda de 1,50 m e subsolo gourmet aterrado já vistos nas revisões anteriores)
8. Validar o castelo maior da caixa de 3.000 L (3,59 × 3,90 m, topo +6,25, 0,50 m mais alto): ele aparece mais nas vistas da frente
9. Acesso ao telhado até a porta do castelo: escada móvel até a capa da suíte e passarela de tábuas sobre as terças (indicativo; definir com a cliente)
10. Fora do escopo (somente arquitetura): levantamento planialtimétrico, sondagem e projetos complementares — estrutural e contenção, fundações, hidrossanitário e pluvial, elétrico — por terceiros, a partir deste anteprojeto

## HIPÓTESES DESTAS PRANCHAS

1. Sentido de abertura das portas de giro indicativo; mobiliário e automóvel ilustrativos (a cliente define o layout).
2. Térreo em ±0,00 (0,15 acima da rua); bloco alto (garagem + sala de estar) com pé-direito 3,20; subsolo gourmet a -3,60 (fase 2).
3. Cotas em metro com 2 casas (Padrão KMZERO); nas cadeias a soma fecha o total (posição acumulada arredondada): a parede externa P-02 sai 0,18 ou 0,19.
4. Cobertura: telhado embutido de fibrocimento (i = 12 %), platibanda de 0,60 m com rufo, calhas em U e condutores ø100 aparentes nas laterais — dimensionar no projeto pluvial.
5. Castelo da caixa d'água: 1 x 3.000 L, porta PC1 de metal vazado (leste), veneziana VC1 (norte); carga cheia indicativa ~3.120 kgf para o projeto estrutural (terceiros).
6. Recuos laterais de 1,50 m: janelas baixas permitidas nas duas laterais (Código Civil art. 1.301); conferir o Código de Obras.
7. Escalas: PL-003 cobertura 1:75, subsolo gourmet 1:100; PL-004 AA 1:100, BB 1:50; PL-005 frente 1:75, fundos 1:100; PL-006 1:150.

| REV. | DATA | DESCRIÇÃO | POR |
|---|---|---|---|
| **R04** | **08/10/2026** | **Emissão do executivo (Cleber): cotas 2 casas, cobertura EX-003, caixa 1 x 3.000 L e porta PC1** | **KMZERO** |
| R04 | 07/10/2026 | Revisão 4 (Ana Paula): ilha clara, banheiros e pendentes da suíte | KMZERO |
| R03 | 07/10/2026 | Revisão 3 (Cleber): entrada pela sala, cozinha nos fundos com a varanda | KMZERO |
| R02 | 06/10/2026 | Revisão 2 (Cleber): varanda 1,50, subsolo gourmet aterrado, gourmet nos fundos, portas, interiores | KMZERO |
| R01 | 06/10/2026 | Revisão 1 (Cleber): recuos 1,50, cozinha em U, piso +0,15, cobertura, subsolo gourmet | KMZERO |
| R00 | 29/09/2026 | Emissão inicial — estudo preliminar | KMZERO |

**KMZERO** | ENGENHARIA · ARQUITETURA

| EMPREENDIMENTO | LOCAL | ETAPA |
|---|---|---|
| **RESIDÊNCIA ANA PAULA** | Rio Espera / MG | **ESTUDO PRELIMINAR** |

CONTEÚDO DA PRANCHA

**FACHADAS LATERAIS · ESQUADRIAS · NOTAS**

| DESENHO | RESPONSÁVEL TÉCNICO | REGISTRO PROFISSIONAL |
|---|---|---|
| **KMZERO** | Kleber Vieira Martins · Arquitetura | sem ART/RRT — estudo preliminar |

| REVISÃO | DATA | ESCALA | UNIDADE | CÓDIGO DA PRANCHA |
|---|---|---|---|---|
| **R04** | 07/10/2026 | 1:150 (fachadas) | metro (m) | **AP-ARQ-PL-006** |

Direitos autorais reservados à KMZERO. Cliente: Ana Paula.