
IMPLANTAÇÃO E SITUAÇÃO

ESCALA 1:150 · norte para cima · cotas de nível em metros

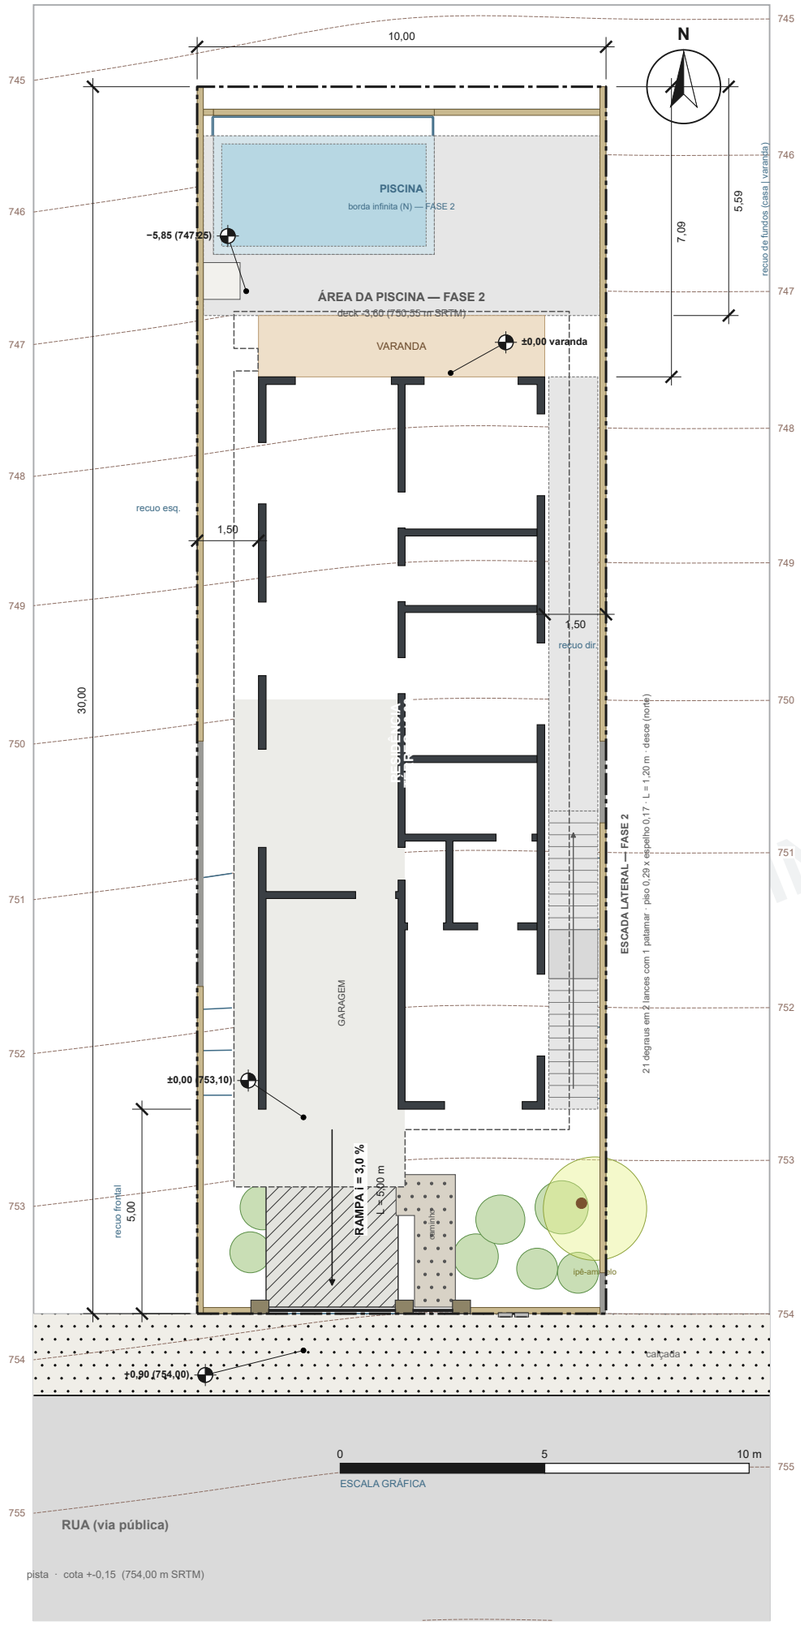

QUADRO DE DADOS DO LOTE E DA EDIFICAÇÃO

Parâmetro	Valor (calculado do modelo)
Terreno (lote 03, quadra 03, compromisso C/V)	10,00 x 30,00 m = 300,00 m²
Área construída coberta (fase 1)	149,80 m² (casa 125,34 + carport 13,96 + varanda 10,50)
Projeção da cobertura	169,58 m² (com beirais, capa da suíte e laje da varanda)
Taxa de ocupação	56,5 % (projeção / lote)
Coef. de aproveitamento	0,50 (área construída / lote; 1 pavimento)
Permeabilidade estimada — fase 1	111,10 m² = 37,0 % (jardim/gramado)
Permeabilidade estimada — fases 1+2	46,98 m² = 15,7 % (deck, piscina e escada impermeáveis)
Recuos (frontal | esq. | dir.)	5,00 | 1,50 | 1,50 m (frontal: carport avança 1,90 m)
Recuo de fundos (casa | varanda)	7,09 | 5,59 m
Altura da edificação	castelo da caixa d'água +6,25 m acima do piso (térreo + subsolo gourmet, fase 2)
Declividade natural do terreno	28,0 % para o norte (SRTM 30 m)
Rampa da garagem	3,0 % subindo da rua (piso 0,15 acima da rua; limite 20 %)
Vaga de garagem	1 carro, vaga 2,50 x 5,00 m (garagem 3,23 x 5,15 m)
Subsolo gourmet (fase 2)	20,94 m² fechados + gourmet aberta

TABELA DE NÍVEIS (Q08)

Nível (Q08)	Relativo	Cota SRTM (m)	Observação
Rua (pista/calçada)	-0,15	754,00	entrada do lote
Piso acabado (garagem, casa, varanda)	±0,00	754,15	referência ±0,00
Forro do corpo baixo	+2,80	756,95	pé-direito 2,80 m
Forro do bloco alto (garagem + sala de estar)	+3,20	757,35	pé-direito 3,20 m
Topo da platibanda (corpo baixo)	+3,55	757,70	telhado embutido atrás
Topo da platibanda (bloco alto)	+3,95	758,10	
Castelo da caixa d'água (topo)	+6,25	760,40	1 x 3.000 L
Subsolo gourmet e piscina (fase 2)	-3,60	750,55	desnível de 3,60 m
Base da contenção (indicativa)	-5,01	749,14	projeto de contenção


AVISO — ESTUDO PRELIMINAR

Estudo preliminar: topografia SRTM (30 m) e lote do compromisso de C/V, sem levantamento; não serve para fundação, contenção, terraplenagem ou aprovação legal.

CROQUI DE SITUAÇÃO (sem escala)

lat. -20,8595924 · lon. -43,4811516


ponto GPS enviado tomado como centro do lote — auditar

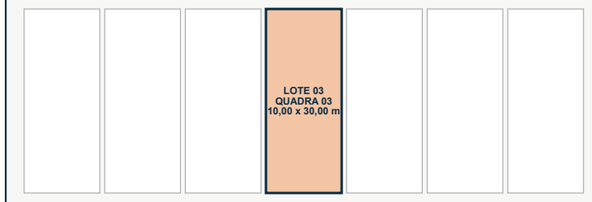

LEGENDA

- Curva de nível — terreno natural (a cada 1,00 m; cota SRTM)
- Curva de nível — terreno acabado (regrade do projeto)
- Limite do lote (compromisso C/V)
- Projeção da cobertura (carport, capa, varanda)
- Paredes do térreo
- Pedra: muro da frente, pilares e arrimos
- FASE 2 — subsolo gourmet, deck, piscina, escada
- Rampa da garagem (concreto desativado)
- Caminho de pedestres (piso intertravado)

PERFIL ESQUEMÁTICO DO LOTE — corte AA (PL-004), escala 1:200

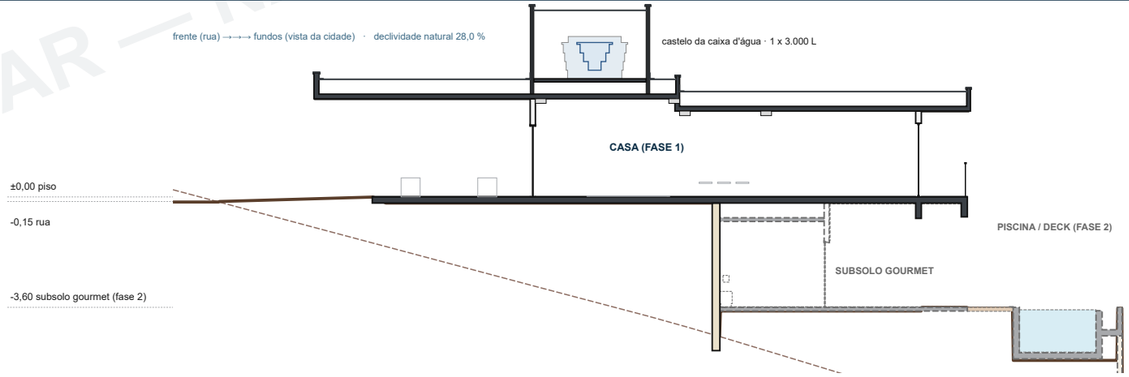

REV.	DATA	DESCRIÇÃO	POR
R04	**08/10/2026**	**Emissão do executivo (Cleber): cotas 2 casas, cobertura EX-003, caixa 1 x 3.000 L e porta PC1**	**KMZERO**
R04	07/10/2026	Revisão 4 (Ana Paula): ilha clara, banheiros e pendentes da suíte	KMZERO
R03	07/10/2026	Revisão 3 (Cleber): entrada pela sala, cozinha nos fundos com a varanda	KMZERO
R02	06/10/2026	Revisão 2 (Cleber): varanda 1,50, subsolo gourmet aterrado, gourmet nos fundos, portas, interiores	KMZERO
R01	06/10/2026	Revisão 1 (Cleber): recuos 1,50, cozinha em U, piso +0,15, cobertura, subsolo gourmet	KMZERO
R00	29/09/2026	Emissão inicial — estudo preliminar	KMZERO

KMZERO | ENGENHARIA · ARQUITETURA

EMPREENDIMENTO	LOCAL	ETAPA
RESIDÊNCIA ANA PAULA	Rio Espera / MG	**ESTUDO PRELIMINAR**

CONTEÚDO DA PRANCHA

IMPLANTAÇÃO E SITUAÇÃO


DESENHO	RESPONSÁVEL TÉCNICO	REGISTRO PROFISSIONAL
KMZERO	Kleber Vieira Martins · Arquitetura	sem ART/RRT — estudo preliminar

REVISÃO	DATA	ESCALA	UNIDADE	CÓDIGO DA PRANCHA
R04	07/10/2026	1:150	metro (m)	**AP-ARQ-PL-001**

Direitos autorais reservados à KMZERO. Cliente: Ana Paula.

PLANTA BAIXA — TÉRREO

ESCALA 1:75 · cortada a 1,20 m acima do piso acabado

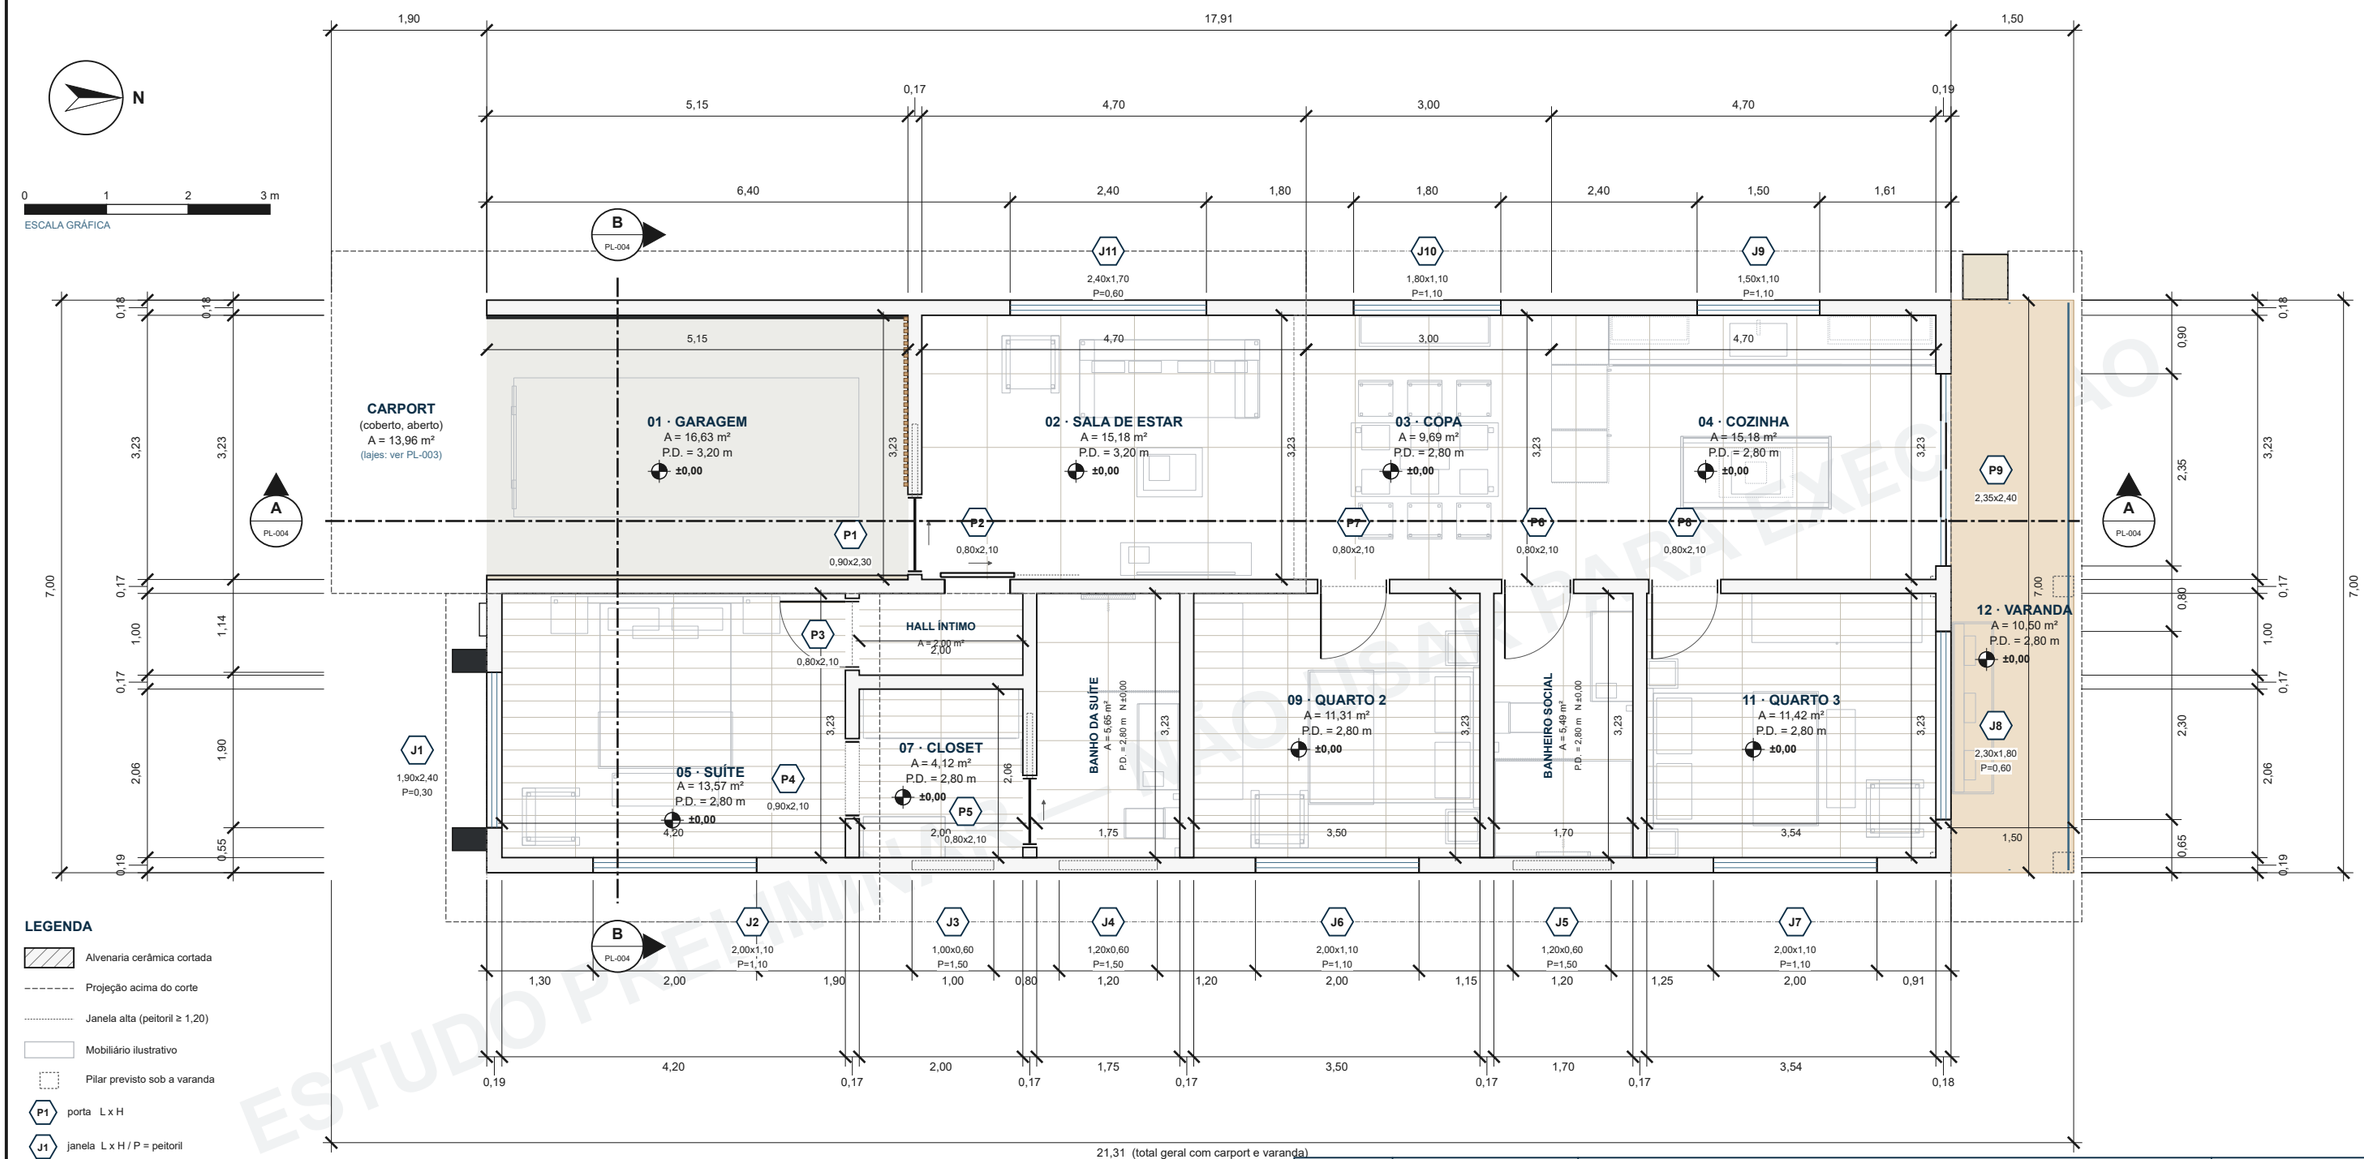

LEGENDA

- Alvenaria cerâmica cortada
- Projeção acima do corte
- Janela alta (peitoril ≥ 1,20)
- Mobiliário ilustrativo
- Pilar previsto sob a varanda
- P1 — porta L x H
- J1 — janela L x H / P = peitoril
- ±0,00 = 754,15 m SRTM
- Beiral (projeção da laje)
- Paginação do piso (juntas)

QUADRO DE AMBIENTES (Q01)

Nº	Ambiente	Área (m²)	P.D. (m)	Piso	Nível
01	Garagem	16,63	3,20	concreto desempenado	±0,00
02	Sala de estar	15,18	3,20	Porcel. marmorizado 90 x 90 polido	±0,00
03	Copa	9,69	2,80	Porcel. marmorizado 90 x 90 polido	±0,00
04	Cozinha	15,18	2,80	Porcel. marmorizado 90 x 90 polido	±0,00
05	Suíte	13,57	2,80	Porcel. amadeirado 20 x 120	±0,00
06	Hall íntimo	2,00	2,80	Porcel. amadeirado 20 x 120	±0,00
07	Closet	4,12	2,80	Porcel. amadeirado 20 x 120	±0,00
08	Banho da suíte	5,65	2,80	Porcel. travertino 60 x 120	±0,00
09	Quarto 2	11,31	2,80	Porcel. amadeirado 20 x 120	±0,00
10	Banheiro social	5,49	2,80	Porcel. marmorizado 90 x 90 polido	±0,00
11	Quarto 3	11,42	2,80	Porcel. amadeirado 20 x 120	±0,00
12	Varanda (coberta)	10,50	2,80	deck de madeira	±0,00
	ÁREA INTERNA DOS AMBIENTES (01-11)	110,24			

QUADRO DE ÁREAS (Q05)

Descrição	Área (m²)	% lote
Terreno (lote 03, quadra 03: 10,00 x 30,00 m)	300,00	100,00
Área interna útil (ambientes 01-11)	110,24	36,7
Paredes (P-02 ext. / P-01 int.)	15,10	5,0
Casa: paredes ext. (7,00 x 17,91)	125,34	41,8
Carport (fora da casa)	13,96	4,7
Varanda coberta (7,00 x 1,50)	10,50	3,5
ÁREA CONSTRUÍDA COBERTA	149,80	49,9
Projeção da cobertura (com beirais)	169,58	56,5
Taxa de ocupação (projeção / lote)	56,5 %	

AVISO: Estudo preliminar: topografia SRTM (30 m) e lote do compromisso de C/V, sem levantamento; não serve para fundação, contenção, terraplenagem ou aprovação legal.

REV.	DATA	DESCRIÇÃO	POR
R04	**08/10/2026**	**Emissão do executivo (Cleber): cotas 2 casas, cobertura EX-003, caixa 1 x 3.000 L e porta PC1**	**KMZERO**
R04	07/10/2026	Revisão 4 (Ana Paula): ilha clara, banheiros e pendentes da suíte	KMZERO
R03	07/10/2026	Revisão 3 (Cleber): entrada pela sala, cozinha nos fundos com a varanda	KMZERO
R02	06/10/2026	Revisão 2 (Cleber): varanda 1,50, subsolo gourmet aterrado, gourmet nos fundos, portas, interiores	KMZERO
R01	06/10/2026	Revisão 1 (Cleber): recuos 1,50, cozinha em U, piso +0,15, cobertura, subsolo gourmet	KMZERO
R00	29/09/2026	Emissão inicial — estudo preliminar	KMZERO

KMZERO | ENGENHARIA · ARQUITETURA

EMPREENDIMENTO	LOCAL	ETAPA
RESIDÊNCIA ANA PAULA	Rio Espera / MG	**ESTUDO PRELIMINAR**

CONTEÚDO DA PRANCHA

PLANTA BAIXA DO TÉRREO

DESENHO	RESPONSÁVEL TÉCNICO	REGISTRO PROFISSIONAL
KMZERO	Kleber Vieira Martins · Arquitetura	sem ART/RRT — estudo preliminar


REVISÃO	DATA	ESCALA	UNIDADE	CÓDIGO DA PRANCHA
R04	07/10/2026	1:75	metro (m)	**AP-ARQ-PL-002**

Direitos autorais reservados à KMZERO. Cliente: Ana Paula.

ESTUDO PRELIMINAR


PLANTA DE COBERTURA

ESCALA 1:75 · telhado embutido de fibrocimento 6 mm, i = 12 %, atrás da platibanda com rufo e calha

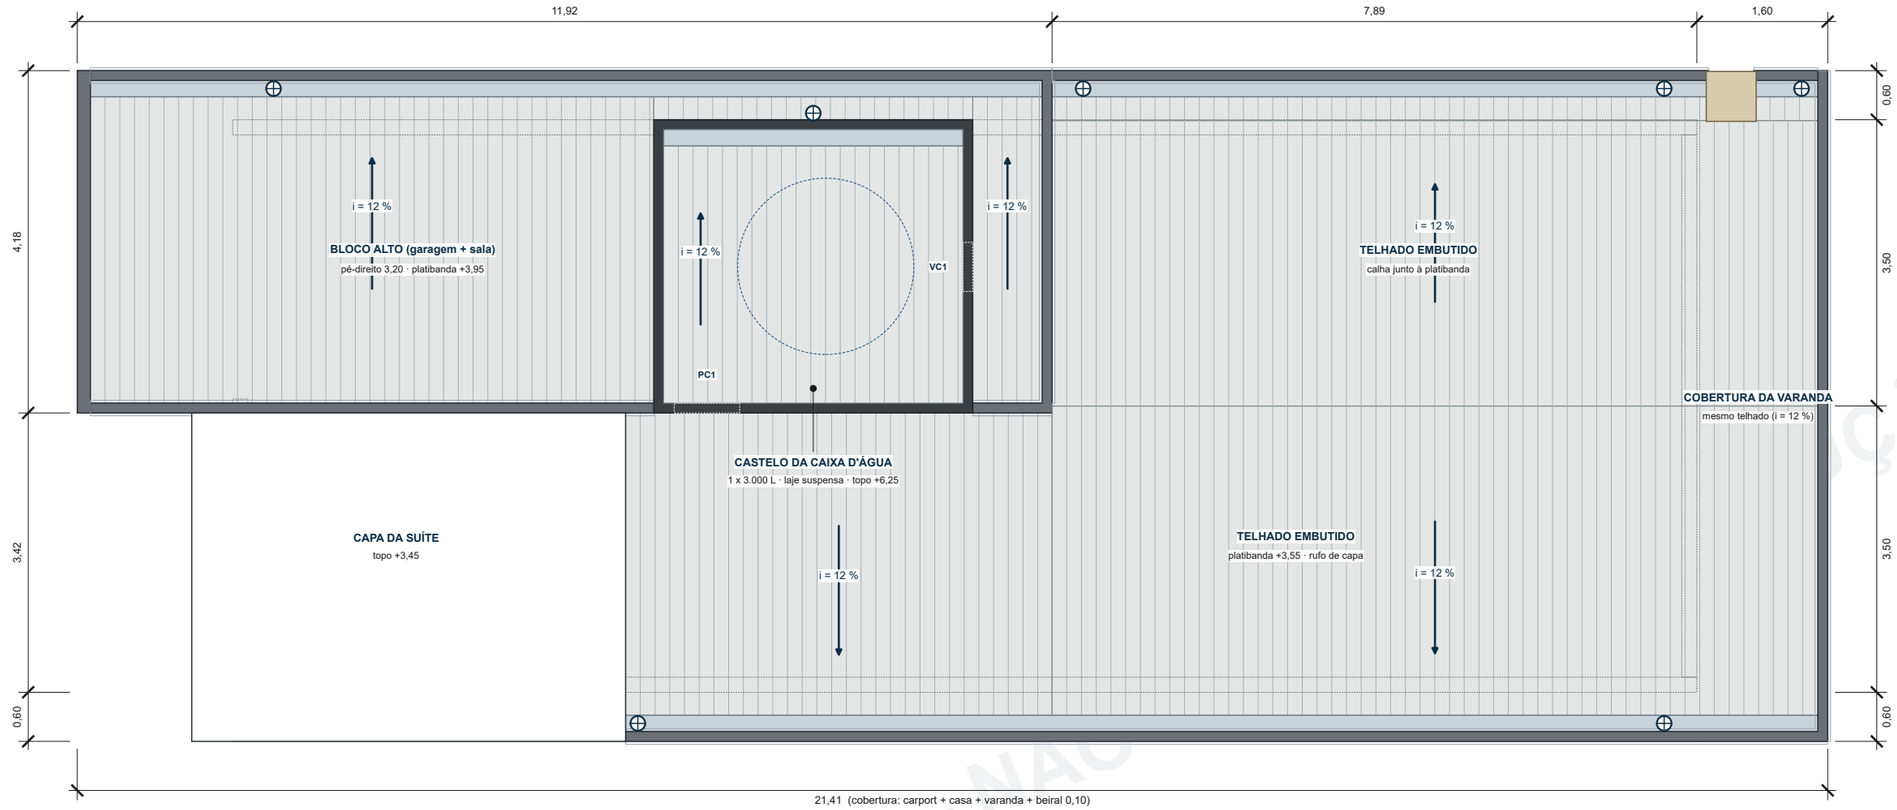

PLANTA DO SUBSOLO GOURMET E ÁREA DA PISCINA — FASE 2

ESCALA 1:100 · cortada a 1,20 m acima do piso do subsolo (-3,60); obra posterior

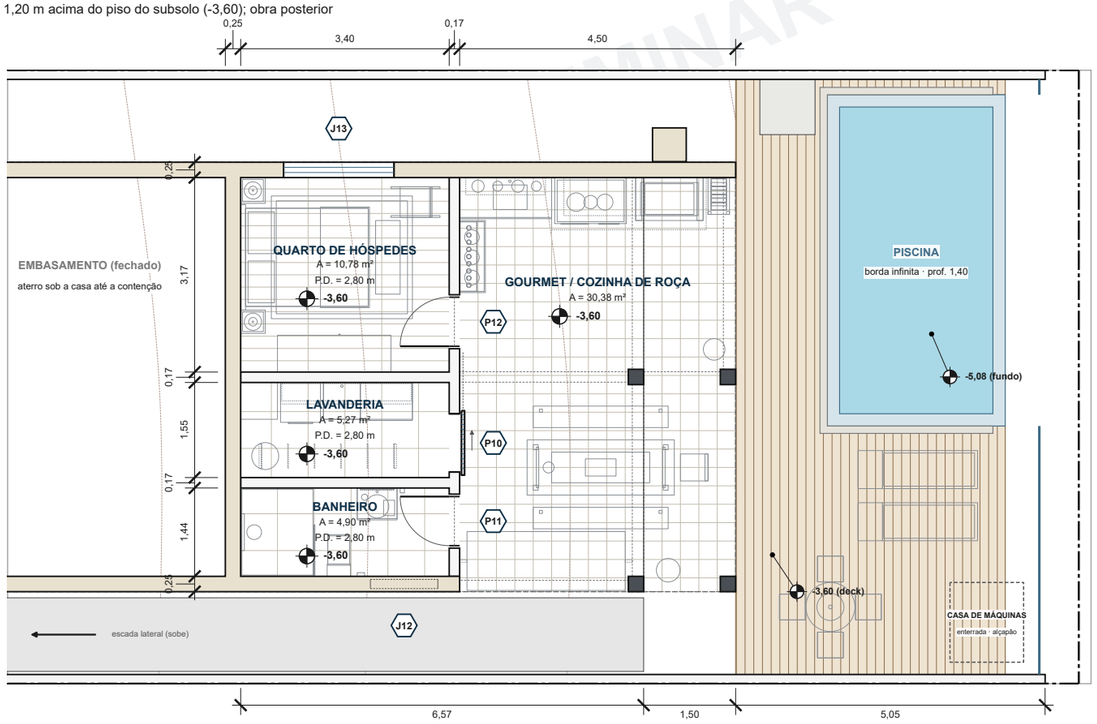

escala gráfica do subsolo gourmet (1:100)

0 1 2 3 4 5 m

ESCALA GRÁFICA

N

NOTAS E HIPÓTESES

1. Cobertura: fibrocimento 6 mm com i = 12 % em duas águas (cumeeira sobre a parede do meio), atrás de platibanda de 0,60 m com rufo de capa e pingadeira; calhas em U (20 x 10) junto às platibandas laterais, rufo de encosto no bloco alto e 6 condutores ø100 aparentes nas laterais (caixa de areia no pé).
2. Bloco alto (garagem + sala de estar) com pé-direito 3,20 e laje própria; sobre a sala de estar, castelo da caixa d'água (1 x 3.000 L, porta PC1 de metal vazado a leste, veneziana VC1 ao norte) com laje suspensa, platibanda e rufo de capa; telhado do castelo escondido, i = 12 % para oeste, com calha e descida na face oeste (para o telhado do bloco alto).
3. Beiral de 0,60 m em todo o perímetro sem outro detalhe; capa da suíte e laje do carport mantêm o desenho da R00.
4. Subsolo gourmet (FASE 2, sobre aterro, -3,60): quarto de hóspedes 10,78 m², lavanderia 5,27 m², banheiro 4,90 m², gourmet / cozinha de roça 30,38 m². Contenção a 6,57 m do fundo da casa; faixa da frente com 3,40 m; gourmet aberta com pé-direito 3,40; paredes externas em pedra até a laje do térreo; tijolinho e forro de madeira na gourmet.
5. Escada lateral: 21 degraus em 2 lances com 1 patamar (espelho 0,17, piso 0,29), do térreo ao subsolo gourmet (desnível 3,60 m).

REV.	DATA	DESCRIÇÃO	POR
R04	**08/10/2026**	**Emissão do executivo (Cleber): cotas 2 casas, cobertura EX-003, caixa 1 x 3.000 L e porta PC1**	**KMZERO**
R04	07/10/2026	Revisão 4 (Ana Paula): ilha clara, banheiros e pendentes da suíte	KMZERO
R03	07/10/2026	Revisão 3 (Cleber): entrada pela sala, cozinha nos fundos com a varanda	KMZERO
R02	06/10/2026	Revisão 2 (Cleber): varanda 1,50, subsolo gourmet aterrado, gourmet nos fundos, portas, interiores	KMZERO
R01	06/10/2026	Revisão 1 (Cleber): recuos 1,50, cozinha em U, piso +0,15, cobertura, subsolo gourmet	KMZERO
R00	29/09/2026	Emissão inicial — estudo preliminar	KMZERO

KMZERO | ENGENHARIA · ARQUITETURA

EMPREENDIMENTO	LOCAL	ETAPA
RESIDÊNCIA ANA PAULA	Rio Espera / MG	**ESTUDO PRELIMINAR**

CONTEÚDO DA PRANCHA

COBERTURA E SUBSOLO GOURMET (FASE 2)

DESENHO	RESPONSÁVEL TÉCNICO	REGISTRO PROFISSIONAL
KMZERO	Kleber Vieira Martins · Arquitetura	sem ART/RRT — estudo preliminar


REVISÃO	DATA	ESCALA	UNIDADE	CÓDIGO DA PRANCHA
R04	07/10/2026	1:75 e 1:100	metro (m)	**AP-ARQ-PL-003**

Direitos autorais reservados à KMZERO. Cliente: Ana Paula.

AVISO: Estudo preliminar: topografia SRTM (30 m) e lote do compromisso de C/V, sem levantamento; não serve para fundação, contenção, terraplenagem ou aprovação legal.


CORTE AA — LONGITUDINAL

ESCALA 1:100 · frente (rua) → fundos
visada para oeste; plano a 2,70 m do eixo x da casa

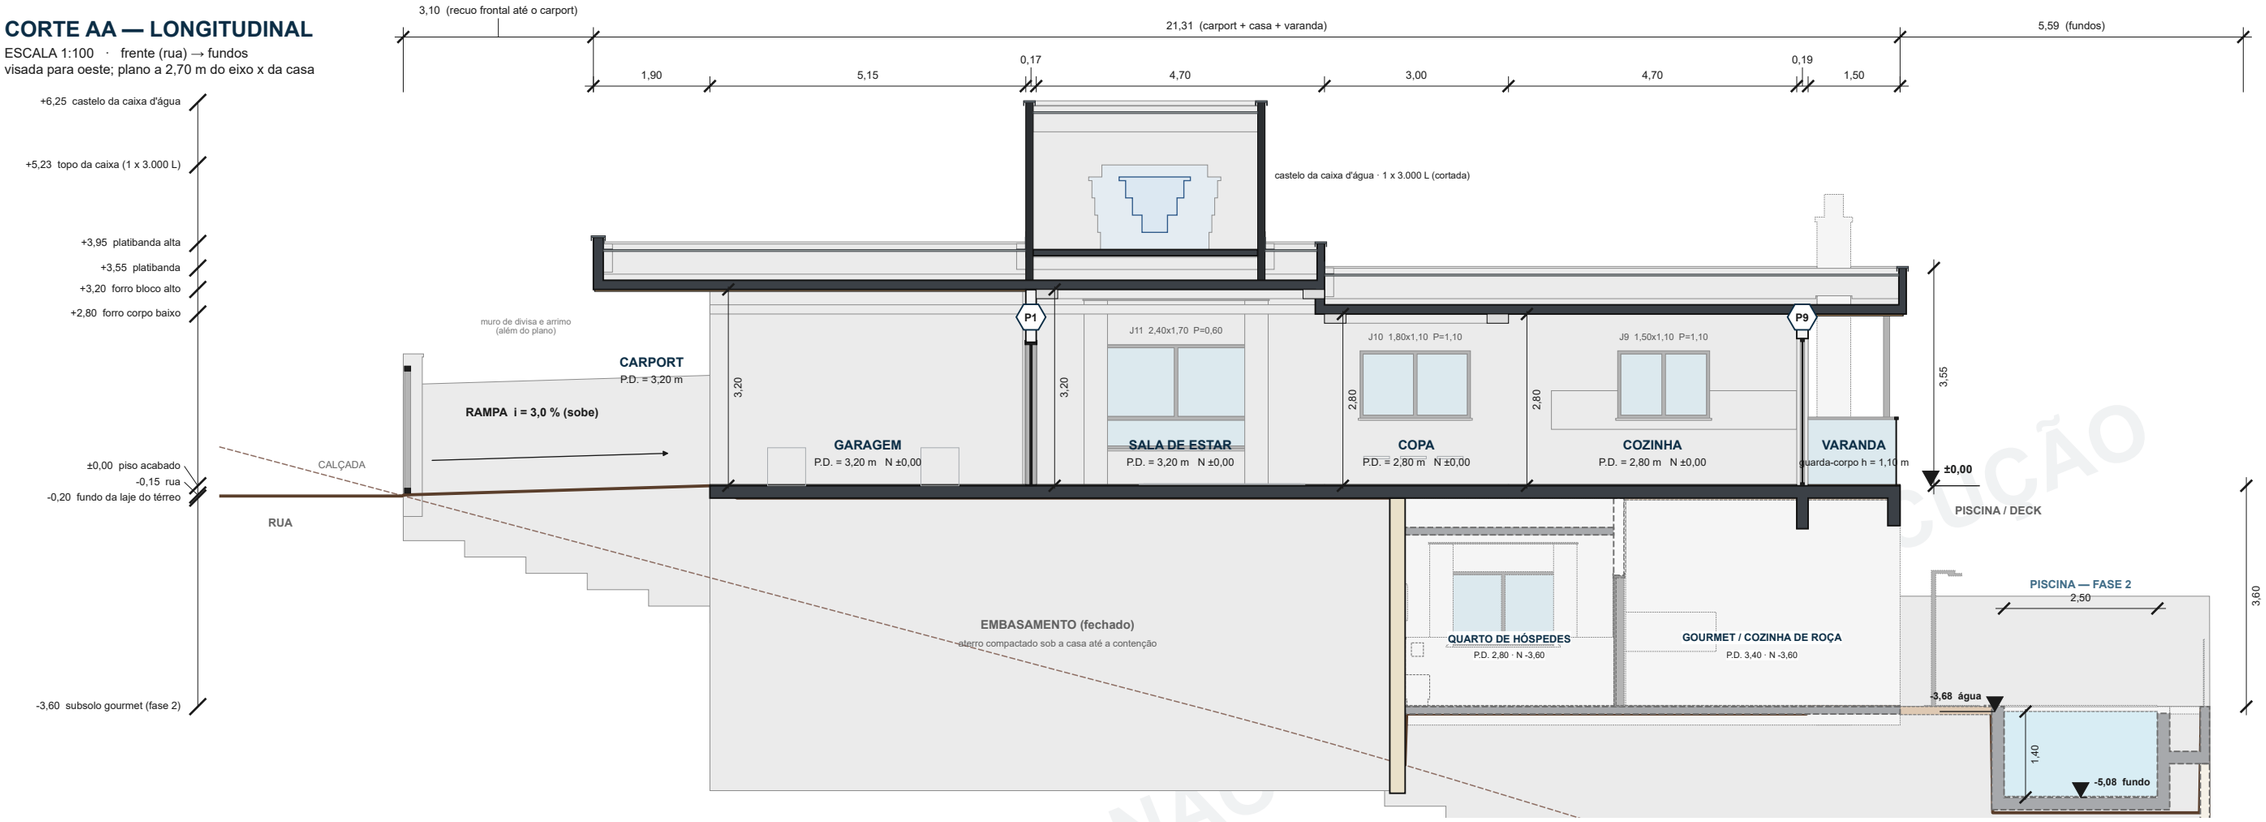

CORTE BB — TRANSVERSAL

ESCALA 1:50 · pela suíte (janela J2) e carport; visada para o norte; plano a 1,60 m da frente da casa

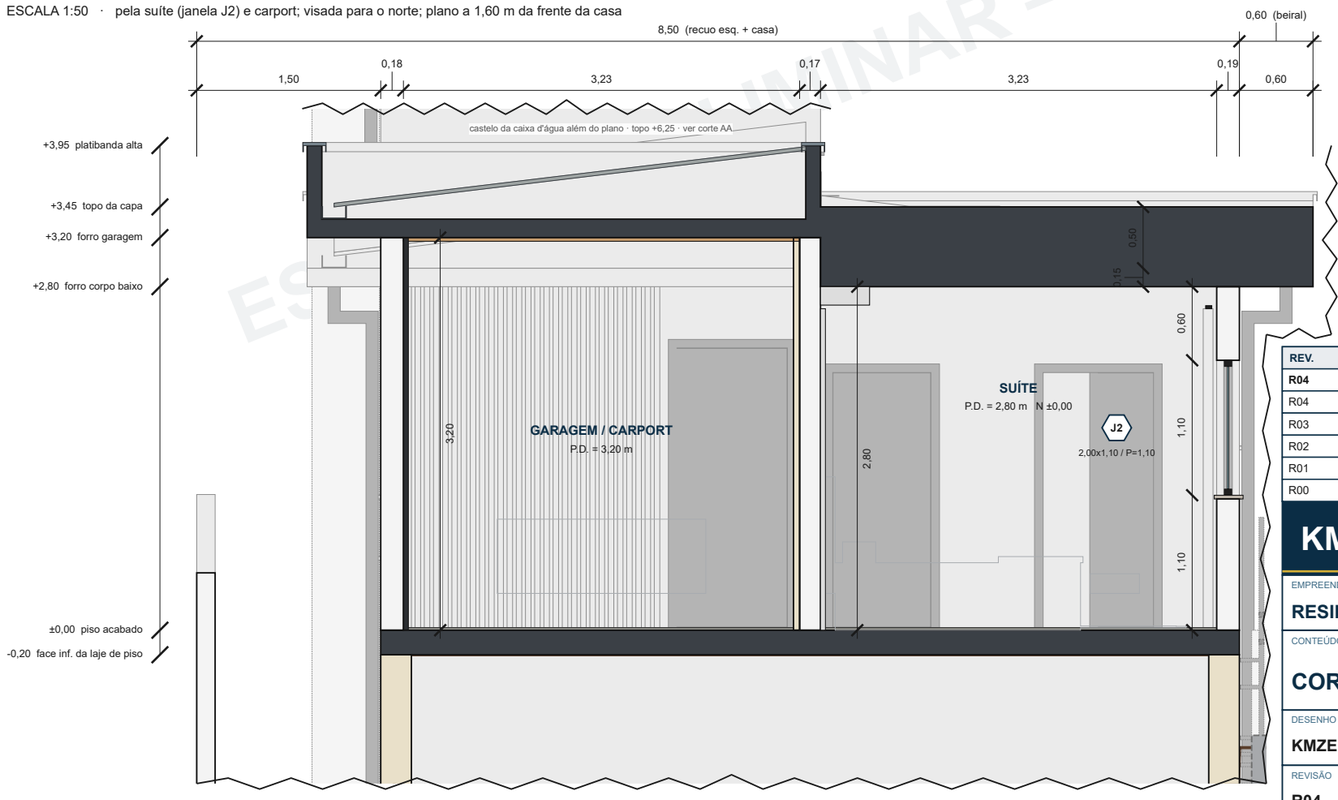

LEGENDA DOS CORTES

- Alvenaria cerâmica (P-02 externa · P-01 interna; espessuras nas cotas)
- Concreto armado (laje, capa, platibanda, pilar)
- Pedra mineira (embasamento, contenção, arrimos, chaminé)
- Forro / painel de madeira
- Esquadria (alumínio preto) e vidro
- Elementos além do plano de corte (cinza claro)
- FASE 2: traço tracejado e cor esmaecida
- Terreno natural (SRTM 30 m)
- Terreno acabado (regrade do projeto)
- Caixa d'água de polietileno (cortada)

NOTAS E HIPÓTESES

1. Cortes gerados por interseção dos sólidos do modelo com o plano; posição dos planos na planta PL-002.
2. Corte AA em 1:100 (o desenvolvimento de 30 m do lote não cabe em 1:75 no A3). Corte BB em 1:50, parcial: cortado abaixo do piso, logo depois do beiral leste e acima da platibanda alta (quebras; o castelo inteiro está no AA).
3. Corte AA passa pela garagem e pela sala de estar (bloco alto; o castelo e a caixa de 1 x 3.000 L, sobre a sala, aparecem cortados), copa, cozinha, varanda e, embaixo, pelo quarto de hóspedes e pela gourmet do subsolo (sobre aterro).
4. Terreno natural = SRTM 30 m (plano de 28,0 %). Contenção do subsolo gourmet a 6,57 m do fundo da casa; fundação e contenção por projeto específico.
5. Níveis relativos ao piso acabado (±0,00 = 754,15 m SRTM, 15 cm acima da rua). FASE 2 em traço tracejado.

REV.	DATA	DESCRIÇÃO	POR
R04	**08/10/2026**	**Emissão do executivo (Cleber): cotas 2 casas, cobertura EX-003, caixa 1 x 3.000 L e porta PC1**	**KMZERO**
R04	07/10/2026	Revisão 4 (Ana Paula): ilha clara, banheiros e pendentes da suíte	KMZERO
R03	07/10/2026	Revisão 3 (Cleber): entrada pela sala, cozinha nos fundos com a varanda	KMZERO
R02	06/10/2026	Revisão 2 (Cleber): varanda 1,50, subsolo gourmet aterrado, gourmet nos fundos, portas, interiores	KMZERO
R01	06/10/2026	Revisão 1 (Cleber): recuos 1,50, cozinha em U, piso +0,15, cobertura, subsolo gourmet	KMZERO
R00	29/09/2026	Emissão inicial — estudo preliminar	KMZERO

KMZERO | ENGENHARIA · ARQUITETURA

EMPREENDIMENTO	LOCAL	ETAPA
RESIDÊNCIA ANA PAULA	Rio Espera / MG	**ESTUDO PRELIMINAR**

CONTEÚDO DA PRANCHA

CORTES AA E BB

DESENHO	RESPONSÁVEL TÉCNICO	REGISTRO PROFISSIONAL
KMZERO	Kleber Vieira Martins · Arquitetura	sem ART/RRT — estudo preliminar

REVISÃO	DATA	ESCALA	UNIDADE	CÓDIGO DA PRANCHA
R04	07/10/2026	AA 1:100 · BB 1:50	metro (m)	**AP-ARQ-PL-004**

AVISO: Estudo preliminar: topografia SRTM (30 m) e lote do compromisso de C/V, sem levantamento; não serve para fundação, contenção, terraplenagem ou aprovação legal.

Direitos autorais reservados à KMZERO. Cliente: Ana Paula.

FACHADA FRENTE (SUL)

ESCALA 1:75 · vista da rua; muro, gradil e portões incluídos



FACHADA FUNDOS (NORTE)

ESCALA 1:100 · vista da cidade; subsolo gourmet, deck e piscina em FASE 2



LEGENDA DE MATERIAIS

M-01	Textura acrílica branca sobre emboço
M-02	Pintura acrílica grafite (moldura, frisos, forro da capa)
M-04	Pedra natural mineira (embasamento, contenção, pilares do portão, chaminé)
M-05	Painel ripado de madeira (garagem e forro do carport/varanda)
M-06	Cobogó — elemento vazado 20 x 20 x 9 cm
M-07	Concreto aparente / laje (pilares, arrimos e piscina)
M-08	Reboco cinza claro (muros de divisa, h = 1,80 m)
V-01	Vidro incolor/laminado (esquadrias e guarda-corpo)
A-01	Alumínio preto (caixilhos, gradil, portões, corrimão)
D-01	Deck de madeira (varanda e área da piscina)
	FASE 2 (subsolo gourmet, deck, piscina): cor esmaecida, traço tracejado

NOTAS E HIPÓTESES

1. Fachadas geradas por projeção ortogonal dos sólidos do modelo (cores planas do JSON de materiais).
2. Frente: muro baixo de pedra com gradil de lâminas verticais vazadas e portões (basculante de veículos e social de giro) em alumínio preto brilhante.
3. Desnível: bloco alto (garagem + sala de estar, pé-direito 3,20) com o castelo da caixa d'água acima (1 x 3.000 L; veneziana VC1 nos fundos, porta PC1 de metal vazado na face leste); corpo baixo com telhado embutido e beiral de 0,60 m.
4. Fundos: subsolo gourmet (FASE 2, sobre aterro) com gourmet aberta na largura toda sob a casa e a varanda, paredes externas em pedra; chaminé de pedra à direita (oeste), ao lado da varanda.
5. Fachada da frente: janela J1 ampliada (1,90 x 2,40) emoldurada em grafite; cobogó ao lado; painel ripado ao fundo da garagem.
6. M-06 = cobogó, conforme pedido para esta prancha (no Padrão KMZERO M-06 é ACM/painel metálico: ajustar a legenda do Padrão).

AVISO: Estudo preliminar: topografia SRTM (30 m) e lote do compromisso de C/V, sem levantamento; não serve para fundação, contenção, terraplenagem ou aprovação legal.

REV.	DATA	DESCRIÇÃO	POR
R04	**08/10/2026**	**Emissão do executivo (Cleber): cotas 2 casas, cobertura EX-003, caixa 1 x 3.000 L e porta PC1**	**KMZERO**
R04	07/10/2026	Revisão 4 (Ana Paula): ilha clara, banheiros e pendentes da suíte	KMZERO
R03	07/10/2026	Revisão 3 (Cleber): entrada pela sala, cozinha nos fundos com a varanda	KMZERO
R02	06/10/2026	Revisão 2 (Cleber): varanda 1,50, subsolo gourmet aterrado, gourmet nos fundos, portas, interiores	KMZERO
R01	06/10/2026	Revisão 1 (Cleber): recuos 1,50, cozinha em U, piso +0,15, cobertura, subsolo gourmet	KMZERO
R00	29/09/2026	Emissão inicial — estudo preliminar	KMZERO

KMZERO | ENGENHARIA · ARQUITETURA

EMPREENDIMENTO **RESIDÊNCIA ANA PAULA**	LOCAL Rio Espera / MG	ETAPA **ESTUDO PRELIMINAR**

CONTEÚDO DA PRANCHA

FACHADAS FRENTE E FUNDOS

DESENHO **KMZERO**	RESPONSÁVEL TÉCNICO Kleber Vieira Martins · Arquitetura	REGISTRO PROFISSIONAL sem ART/RRT — estudo preliminar


REVISÃO **R04**	DATA 07/10/2026	ESCALA 1:75 e 1:100	UNIDADE metro (m)	CÓDIGO DA PRANCHA **AP-ARQ-PL-005**

Direitos autorais reservados à KMZERO. Cliente: Ana Paula.

NÃO USAR PARA EXECUÇÃO

FACHADA LESTE (lado direito)

ESCALA 1:150 · observador a leste; frente à esquerda; muros de divisa e arrimos translúcidos

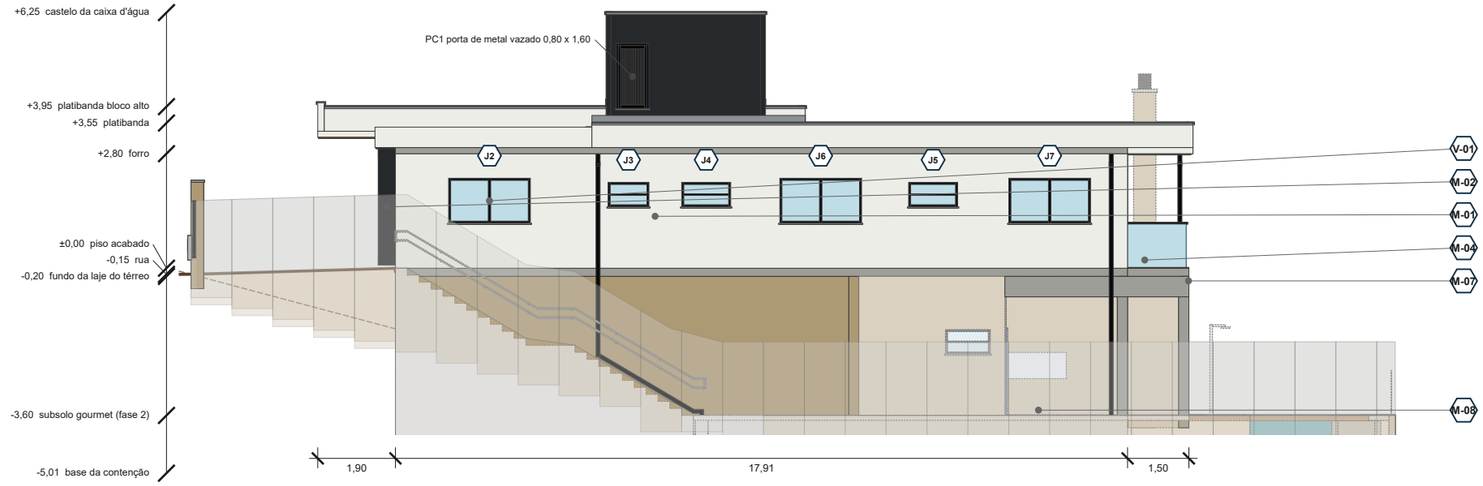

FACHADA OESTE (lado esquerdo)

ESCALA 1:150 · observador a oeste; fundos à esquerda; recuo de 1,50 m com janelas baixas e peitoril de granito

QUADRO DE ESQUADRIAS (Q02/Q03)

Cód.	Descrição	L (m)	H (m)	Peit. (m)	Tipologia · material	Qtd.
P1	Porta de entrada (correr embutida, para a sala)	0,90	2,30	0,00	correr embutida (kit na parede) · madeira maciça (freijó/imbuia, a definir)	1
P2	Porta sala/hall da suíte (correr aparente)	0,80	2,10	0,00	correr aparente · madeira maciça · trilho preto aparente	1
P3	Porta suíte (hall)	0,80	2,10	0,00	giro 1 folha · madeira semi-oca ou maciça (a definir)	1
P4	Passagem suíte/closet	0,90	2,10	0,00	passagem livre (sem folha) · vão com guarnição de madeira	1
P5	Porta banho da suíte (correr embutida)	0,80	2,10	0,00	correr embutida (kit na parede) · madeira maciça (freijó/imbuia, a definir)	1
P6	Porta banheiro social	0,80	2,10	0,00	giro 1 folha · madeira semi-oca ou maciça (a definir)	1
P7	Porta quarto 2	0,80	2,10	0,00	giro 1 folha · madeira semi-oca ou maciça (a definir)	1
P8	Porta quarto 3	0,80	2,10	0,00	giro 1 folha · madeira semi-oca ou maciça (a definir)	1
P9	Porta de correr de vidro (cozinha/varanda)	2,35	2,40	0,00	correr, folhas de vidro · vidro temperado incolor 8 mm + alumínio preto	1
J1	Janela alta da suíte (fachada)	1,90	2,40	0,30	fixa (+ bandeira) · alumínio preto + vidro laminado 8 mm	1
J2	Janela suíte	2,00	1,10	1,10	correr 2 folhas · alumínio preto + vidro incolor 6 mm · peitoril de granito	1
J3	Janela closet	1,00	0,60	1,50	basculante · alumínio preto + vidro mini-boreal 4 mm · peitoril de granito	1
J4	Janela banho suíte	1,20	0,60	1,50	maxim-ar · alumínio preto + vidro mini-boreal 4 mm · peitoril de granito	1
J5	Janela banheiro social	1,20	0,60	1,50	maxim-ar · alumínio preto + vidro mini-boreal 4 mm · peitoril de granito	1
J6	Janela quarto 2	2,00	1,10	1,10	correr 2 folhas · alumínio preto + vidro incolor 6 mm · peitoril de granito	1
J7	Janela quarto 3 (leste)	2,00	1,10	1,10	correr 2 folhas · alumínio preto + vidro incolor 6 mm · peitoril de granito	1
J8	Janela quarto 3 (vista)	2,30	1,80	0,60	correr 2 folhas · alumínio preto + vidro laminado 8 mm · peitoril de granito	1
J9	Janela cozinha (sobre a pia)	1,50	1,10	1,10	correr 2 folhas · alumínio preto + vidro incolor 6 mm · peitoril de granito	1
J10	Janela copa	1,80	1,10	1,10	correr 2 folhas · alumínio preto + vidro incolor 6 mm · peitoril de granito	1
J11	Janela sala	2,40	1,70	0,60	correr 2 folhas + fixo inferior · alumínio preto + vidro laminado 8 mm · peitoril de granitot	1
PC1 **	Porta de acesso à caixa d'água	0,80	1,60	0,05 (cast.)	giro, abre para fora · metal vazado (alumínio preto + tela inox)	1
VC1 **	Veneziana de ventilação do castelo	0,60	0,30	1,30 (cast.)	veneziana fixa · alumínio preto	1
P10 *	Porta lavanderia (correr veneziana)	0,95	2,10	0,00 (inf.)	correr veneziana · madeira azul colonial · trilho preto	1
P11 *	Porta banheiro (inferior)	0,80	2,10	0,00 (inf.)	giro 1 folha · madeira pintada azul colonial (gourmet de roça)	1
P12 *	Porta quarto de hóspedes	0,80	2,10	0,00 (inf.)	giro 1 folha · madeira pintada azul colonial (gourmet de roça)	1
J12 *	Janela banheiro (inferior)	1,10	0,60	1,50 (inf.)	maxim-ar · alumínio preto + vidro mini-boreal 4 mm · peitoril de granito	1
J13 *	Janela quarto de hóspedes	1,80	1,20	1,00 (inf.)	correr 2 folhas · alumínio preto + vidro incolor 6 mm · peitoril de granito	1

Fase 1: 10 portas + 12 janelas = 22 vãos (com as 2 do castelo). * subsolo gourmet (fase 2), peitoril medido do piso do subsolo (-3,60).

** castelo da caixa d'água (1 x 3.000 L): peitoril medido do piso do castelo (+3,85); PC1 abre para fora (leste), dobradiças no batente norte; detalhes no AP-ARQ-EX-003.

Portas: altura livre do vão; peitoril = distância do piso acabado (±0,00) à soleira da esquadria.

LEGENDA DE MATERIAIS

- M-01 — Textura acrílica branca sobre emboço
- M-02 — Pintura acrílica grafite (moldura, frisos, forro da capa)
- M-04 — Pedra natural mineira (embasamento, contenção, pilares do portão, chaminé)
- M-05 — Painel ripado de madeira (garagem e forro do carport/varanda)
- M-06 — Cobogó — elemento vazado 20 x 20 x 9 cm
- M-07 — Concreto aparente / laje (pilares, arrimos e piscina)
- M-08 — Reboco cinza claro (muros de divisa, h = 1,80 m)
- V-01 — Vidro incolor/laminado (esquadrias e guarda-corpo)
- A-01 — Alumínio preto (caixilhos, gradil, portões, corrimão)
- D-01 — Deck de madeira (varanda e área da piscina)
- FASE 2 (subsolo gourmet, deck, piscina): cor esmaecida, traço tracejado

DECISÕES DA R04 (casa_ana_paula.json)

1. Pedido da Ana Paula (foto de referência): ilha em cor clara. Tampo e laterais em cascata até o piso em porcelanato branco com veios cinza (efeito mármore), frentes no mesmo material; cooktop e coifa de ilha mantidos. A bancada da pia segue em granito cinza.
2. Pedido da Ana Paula: tom claro com acessórios dourados. Paredes em porcelanato branco com veios dourados até o teto, faixa de ripado de madeira entre a bancada e o box, nicho de madeira, deck de madeira no piso do box, piso marmorizado claro; torneira, chuveiro, perfil do box, papeleira, toalheiro e moldura do espelho dourados.
3. Ideia da KMZERO (a Ana Paula ainda não tinha ideia): banho "spa natural". Box em porcelanato travertino até o teto com nicho iluminado, piso em travertino 60 x 120, parede da bancada em verde-musgo, gabinete de madeira com tampo de travertino, espelho redondo com LED por trás e metais em dourado escovado.
4. Pedido da Ana Paula (foto de referência): pendentes de cabeceira com aro oval de cristal iluminado, haste e canopla douradas e cabo fino até o teto.
5. Pedido do Cleber: calha, rufo e descida à mostra e outra cobertura para a caixa d'água. Estudada a telha colonial a 35 %, ficou o fibrocimento, agora a 12 %, ainda escondido pela platibanda de 60 cm. Calhas em U de chapa galvanizada, rufo de capa com pingadeira, rufo de encosto no bloco alto, condutores ø100 em alumínio preto aparentes nas laterais com caixa de areia; castelo da caixa d'água sem o telhadinho, com platibanda, rufo, telhado escondido, calha e descida.
6. Escopo da KMZERO neste projeto: somente arquitetura. Estrutural, contenção, fundações, hidrossanitário e pluvial, elétrico, levantamento e sondagem ficam com terceiros; as posições de calhas, descidas, pilares e arrimos do modelo são indicativas.
7. Emissão do executivo (Cleber), 08/10/2026: cotas com 2 casas, fechando o total nas cadeias; cobertura executiva no AP-ARQ-EX-003 (condutores CP-01 a CP-07); caixa d'água 1 x 3.000 L no castelo de 3,59 × 3,90 m (topo +6,25), porta PC1 0,80 × 1,60 de metal vazado na face leste e veneziana VC1 0,60 × 0,30 ao norte.

AVISO: Estudo preliminar: topografia SRTM (30 m) e lote do compromisso de C/V, sem levantamento; não serve para fundação, contenção, terraplenagem ou aprovação legal.

PENDÊNCIAS PARA A ETAPA SEGUINTE

1. Documento da compra do irmão (o compromisso está no nome do Tiago): recibo, contrato ou cessão
2. Escritura e matrícula individual (só após a conclusão do loteamento)
3. Croqui do loteamento (anexo do compromisso) e pin correto do lote 03, quadra 03
4. Pavimento e redes da Rua 02 no local (contrato prevê bloquete)
5. Código de Obras de Rio Espera: recuos, taxa de ocupação, permeabilidade, altura de muro
6. Cliente escolher porcelanato/acabamentos (loja Tau, em Rio Espera, citada por ela)
7. Validar com a cliente a R04: ilha clara, banheiros, pendentes da suíte e cobertura com calhas e descidas aparentes (entrada pela sala, varanda de 1,50 m e subsolo gourmet aterrado já vistos nas revisões anteriores)
8. Validar o castelo maior da caixa de 3.000 L (3,59 × 3,90 m, topo +6,25, 0,50 m mais alto): ele aparece mais nas vistas da frente
9. Acesso ao telhado até a porta do castelo: escada móvel até a capa da suíte e passarela de tábuas sobre as terças (indicativo; definir com a cliente)
10. Fora do escopo (somente arquitetura): levantamento planialtimétrico, sondagem e projetos complementares — estrutural e contenção, fundações, hidrossanitário e pluvial, elétrico — por terceiros, a partir deste anteprojeto

HIPÓTESES DESTAS PRANCHAS

1. Sentido de abertura das portas de giro indicativo; mobiliário e automóvel ilustrativos (a cliente define o layout).
2. Térreo em ±0,00 (0,15 acima da rua); bloco alto (garagem + sala de estar) com pé-direito 3,20; subsolo gourmet a -3,60 (fase 2).
3. Cotas em metro com 2 casas (Padrão KMZERO); nas cadeias a soma fecha o total (posição acumulada arredondada): a parede externa P-02 sai 0,18 ou 0,19.
4. Cobertura: telhado embutido de fibrocimento (i = 12 %), platibanda de 0,60 m com rufo, calhas em U e condutores ø100 aparentes nas laterais — dimensionar no projeto pluvial.
5. Castelo da caixa d'água: 1 x 3.000 L, porta PC1 de metal vazado (leste), veneziana VC1 (norte); carga cheia indicativa ~3.120 kgf para o projeto estrutural (terceiros).
6. Recuos laterais de 1,50 m: janelas baixas permitidas nas duas laterais (Código Civil art. 1.301); conferir o Código de Obras.
7. Escalas: PL-003 cobertura 1:75, subsolo gourmet 1:100; PL-004 AA 1:100, BB 1:50; PL-005 frente 1:75, fundos 1:100; PL-006 1:150.

REV.	DATA	DESCRIÇÃO	POR
R04	**08/10/2026**	**Emissão do executivo (Cleber): cotas 2 casas, cobertura EX-003, caixa 1 x 3.000 L e porta PC1**	**KMZERO**
R04	07/10/2026	Revisão 4 (Ana Paula): ilha clara, banheiros e pendentes da suíte	KMZERO
R03	07/10/2026	Revisão 3 (Cleber): entrada pela sala, cozinha nos fundos com a varanda	KMZERO
R02	06/10/2026	Revisão 2 (Cleber): varanda 1,50, subsolo gourmet aterrado, gourmet nos fundos, portas, interiores	KMZERO
R01	06/10/2026	Revisão 1 (Cleber): recuos 1,50, cozinha em U, piso +0,15, cobertura, subsolo gourmet	KMZERO
R00	29/09/2026	Emissão inicial — estudo preliminar	KMZERO

KMZERO | ENGENHARIA · ARQUITETURA

EMPREENDIMENTO	LOCAL	ETAPA
RESIDÊNCIA ANA PAULA	Rio Espera / MG	**ESTUDO PRELIMINAR**

CONTEÚDO DA PRANCHA

FACHADAS LATERAIS · ESQUADRIAS · NOTAS

DESENHO	RESPONSÁVEL TÉCNICO	REGISTRO PROFISSIONAL
KMZERO	Kleber Vieira Martins · Arquitetura	sem ART/RRT — estudo preliminar

REVISÃO	DATA	ESCALA	UNIDADE	CÓDIGO DA PRANCHA
R04	07/10/2026	1:150 (fachadas)	metro (m)	**AP-ARQ-PL-006**

Direitos autorais reservados à KMZERO. Cliente: Ana Paula.